LOT 1728 · RIVIERA PALMERAIE · COCODY, ABIDJAN

Maison à patio et trois maisons en duplex

Option C v4 · dossier de présentation · esquisse



Villa : 275,56 m² clos
4 chambres dont nounou, bureau, cuisine africaine, toit-terrasse sous pergola

Locatif : 3 maisons de 108,00 m²
duplex 2 chambres, jardin, toit-terrasse sous pergola

492,6 M FCFA TTC
villa et locatif, ratios Éco-données ÷ 2

7 novembre 2026 · Projet personnel · Image : rendu d'ambiance généré par IA (Higgsfield) à partir de la maquette.

SYNTHÈSE

Votre markup, appliqué à la trame

Les trames de votre markup du 7 novembre sont reprises telles quelles, avec deux ajustements pour tenir dans la bande de 18 m : stationnement de 4,50 m au Nord et passages de 1,00 m à l'Est et au fond. La villa garde son patio au cœur ; l'étage se dessine en L (salon familial et deux chambres sur la rue, chambre principale au fond) ; l'escalier monte à un toit-terrasse sous pergola, bordé d'une jardinière de firecracker plants qui retombe sur la double peau Nord. Au fond, un mur végétalisé. Au Sud, trois maisons en duplex, chacune avec son jardin, son stationnement et sa pergola.

275,56 m²
villa close (RDC 149,01, étage 126,55)

110 m²
toit-terrasse sous pergola de la villa

324,00 m²
locatif : 3 duplex de 108 m², jardins et pergolas

269,0 M
villa, total TTC, FCFA

223,5 M
locatif, total TTC, FCFA

Trame retenue (m)


Villa, en X : recul Ouest 3,5 · 3 · 3,5 · 3,5 · 2 · 3,5 · passage 1.
Villa, en Y : stationnement 4,5 · bande avant 1,2 · 5,5 · 5,8 · passage 1 · mur végétalisé.
Étage, en Y : 1,2 (loggia-rangement) · 5,5 · 2,6 (SdB, dressing) · 3,2 (chambre principale).
Locatif : allée 2 · 6 · 6 · 6 en X ; jardins 3 · 5,5 · 3,5 · stationnement 3 en Y.

Ce qui change

- Bureau au RDC, chambre 3 supprimée : 4 chambres dont la nounou
- Étage en L, galerie vitrée sur le patio au lieu de la passerelle
- Niveau pergola, jardinière continue, mur végétalisé
- Double peau Nord en deux variantes
- Locatif : 3 maisons duplex au lieu de 6 logements

Représentation

- Plans aux conventions Capitude : aplats à 45 % par usage, légende, trame d'axes, murs noirs
- Blocs Archibooks de la base : portes, arbres, sols, eau, végétation et personnages de coupe
- Rendus réalistes générés par IA à partir des maquettes, en dernière partie

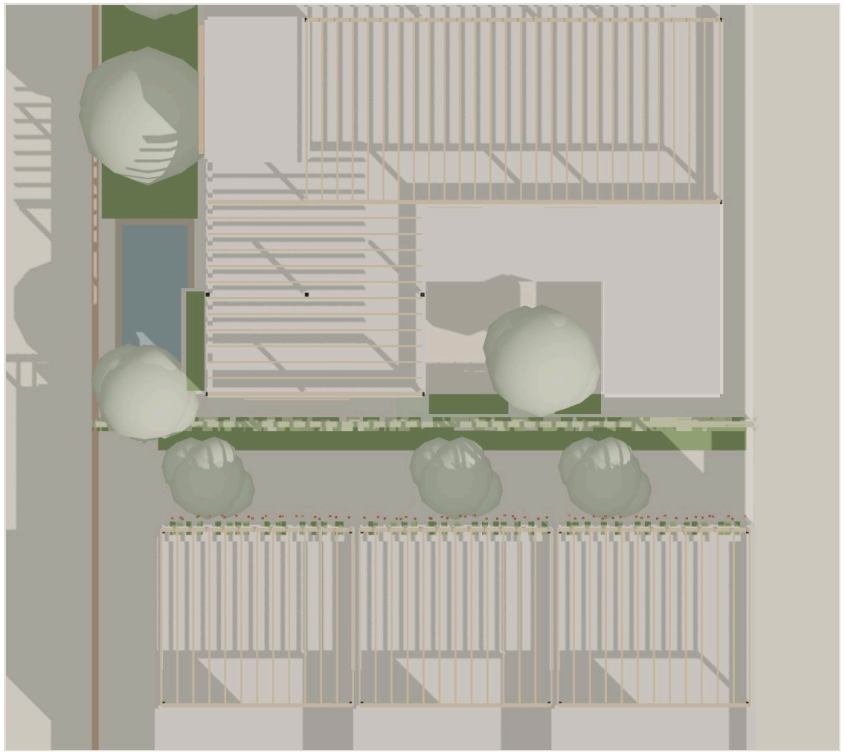

Vue de dessus de la maquette, Nord en haut : villa, patio et pergola au Nord, trois maisons au Sud, mur végétalisé entre les deux.

1 · SITE ET IMPLANTATION

Une parcelle d’angle de 20 × 33 m, deux bandes

- Lot 1728, îlot 174, Djorogobité 1 : 660 m² à l’angle de deux voies en terre, au Nord et à l’Ouest.
- Villa sur la bande Nord de 20 × 18 m : stationnement de 3 places sur la rue Nord (4,50 m), guérite, local GE et niche à compteurs à l’angle Nord-Ouest, portillon de service et séchoir au Nord-Est.
- Locatif sur la bande Sud de 20 × 15 m : allée piétonne de 2 m le long de la rue Ouest, trois maisons de 6 × 9 m, jardins privés au Nord contre le mur végétalisé, stationnement au Sud.
- Climat lagunaire (5° N) : soleil presque au zénith, pignons Est et Ouest exposés, vents de Sud-Ouest, averses violentes.
- À confirmer : reculs, emprise, hauteur (le niveau pergola n’est pas un étage clos), vues droites à 1,90 m vers l’Est, accès du stationnement locatif.

Matière de Palinda Kannangara, représentation Capitude

Palinda Kannangara Architects : Casa Lineal et Casa Estudio (Sri Lanka)

Deux maisons tropicales humides sur petites parcelles, organisées autour d'un patio planté, comme l'option C. Leur matière (béton brut coffré planches, moellons, brique ajourée, bois, ciment poli) se trouve à Abidjan et vieillit bien sous la pluie. Climat proche : Colombo est à 7° N, Abidjan à 5° N, mêmes moussons et mêmes pluies d'orage.

Double peau Nord semi-perforée	Devant la loggia-rangement de 1,2 m de l'étage, sur toute la façade sur rue ; deux variantes (brique, résille béton)
Béton brut coffré planches	Nez de dalle, corniches à goutte d'eau, édicule d'escalier
Moellons de pierre	Rez-de-chaussée sur les deux rues, guérite, socle de la clôture (Casa Lineal)
Toit habité	Toit-terrasse sous pergola bois, jardinière continue de firecracker plants sur la façade Nord (Casa Estudio : toiture-jardin habitée)
Patio et galerie	Galerie vitrée de l'étage sur le patio, écrans en lattes de bois, bio-bassin au pied de l'arbre (Casa Lineal)
Jardin d'entrée, bassin, séjour	Bio-bassin devant le coulissant du salon dans la bande Ouest (séquence de Casa Lineal)
Limites végétales	Mur végétalisé en fond de parcelle, clôture en brique ajourée : la maison plonge dans la verdure

Variante 2 de la double peau : Typologie urbaine 8 (Capitude), « claustra en résille triangulée en nu extérieur, devant une loggia filante ». Les images des planches ne sont pas consultées : la lecture repose sur les données et les légendes de la base.

Règles graphiques appliquées (table regles_agents)

GRAPHISME-APLATS-LEGENDE-TRAME	Aplats pastel à 45 % par usage, légende sur chaque plan, trame d'axes 1-6 / A-E en périphérie
GRAPHISME-OPACITES	Murs, cotes, textes noirs opaques ; végétation 45-65 %, sols 55-70 %, mobilier 80 %, eau 30 %
GRAPHISME-ELCROQUIS-EXTERIEURS	Sols différenciés et recadrés au contour, strates végétales, bassins
BLOCS-ARCHIBOOKS	Portes, arbres, textures et eau issus du bucket privé, maîtres inchangés, SHA-256 contrôlés
PAYSAGE-TROPICAL-COMPOSITION	Arbres variés selon leur rôle : repère du patio, ombre Ouest, angle des rues, fond de parcelle
VEGETATION / PERSONNAGES-COUPES	Blocs veg_coupe_* et personnages pers_tt / pers_pmd dans les coupes

Blocs Archibooks utilisés

porte_battante_90, porte_double · arbre_frangipanier, arbre_feuilles_ovales, arbre_touffes_frisees, arbre_feuillage_dense · texture_paves, texture_pierre_bandes, texture_granulat_fin, texture_couvre_sol, texture_massif_tropical, texture_pas_irreguliers, texture_eau · veg_coupe_petit_feuillu_dense, veg_coupe_palmier_retombant, veg_coupe_fougeres, veg_coupe_grandes_feuilles, veg_coupe_bosquet_etage · pers_tt_02, pers_tt_03, pers_pmd_042, pers_pmd_108.

Absents du catalogue (signalés) : appareils sanitaires, lits, canapés, tables, plans de cuisine, voitures, cadre et cartouche. Ils sont dessinés ici en symboles neutres provisoires, à remplacer quand la bibliothèque les aura.

Enchaînements, distances et salles d’eau

Distances de parcours, de porte à porte

Parcours	Distance	Passage
Portillon → porte d’entrée	5,72 m	sous le passage couvert, à l’écart des voitures
Porte d’entrée → salon	7,41 m	par le hall ; WC visiteurs au passage
Cuisine → table de la SAM	4,32 m	porte directe
Cuisine → cuisine africaine	5,62 m	par la buanderie-sas
Portillon de service → cuisine africaine	7,21 m	livraisons sans traverser la maison
Chambre nounou → cuisine	12,40 m	par le passage Est et la buanderie
Bureau → hall	11,12 m	par la terrasse et la SAM
Escalier → salon familial	3,21 m	arrivée directe dans le salon familial
Chambre principale → chambre 1	11,05 m	par le dressing, le salon familial et la galerie
Chambre principale → chambre 2	14,06 m	galerie de 1,20 m vitrée sur le patio


Circulations closes (hall, escaliers, galerie) : 42,80 m², soit 16 % de la surface close, dans la fourchette des villas de la base (13 % ABYA 2 à 27 % Anthurium).

Salles d’eau

Pièce	Dimensions	m²	Disposition
SE ch.1	2,00 × 2,15	4,30	lanière, porte depuis la chambre, jour haut sur la loggia
SE ch.2	2,00 × 2,15	4,30	dos à dos avec la SE ch.1 (une gaine)
SdB parentale	3,00 × 2,60	7,80	par le dressing : douche à l’italienne, double vasque, WC
SE nounou	3,50 × 1,40	4,90	lanière, jours hauts sur le patio et le passage Est
WC visiteurs	3,00 × 1,30	3,90	depuis le hall, sous l’escalier, jour haut à l’Ouest


> Invités, famille et service ne se croisent pas : la rue mène au salon par le hall sans voir le service ; le personnel entre par le portillon de service et rejoint la cuisine par la buanderie-sas ; la nounou a sa porte sur le passage Est. À l’étage, le salon familial distribue la suite au fond du L et, par la galerie vitrée sur le patio, les chambres 1 et 2.

Rez-de-chaussée · 149,01 m² clos

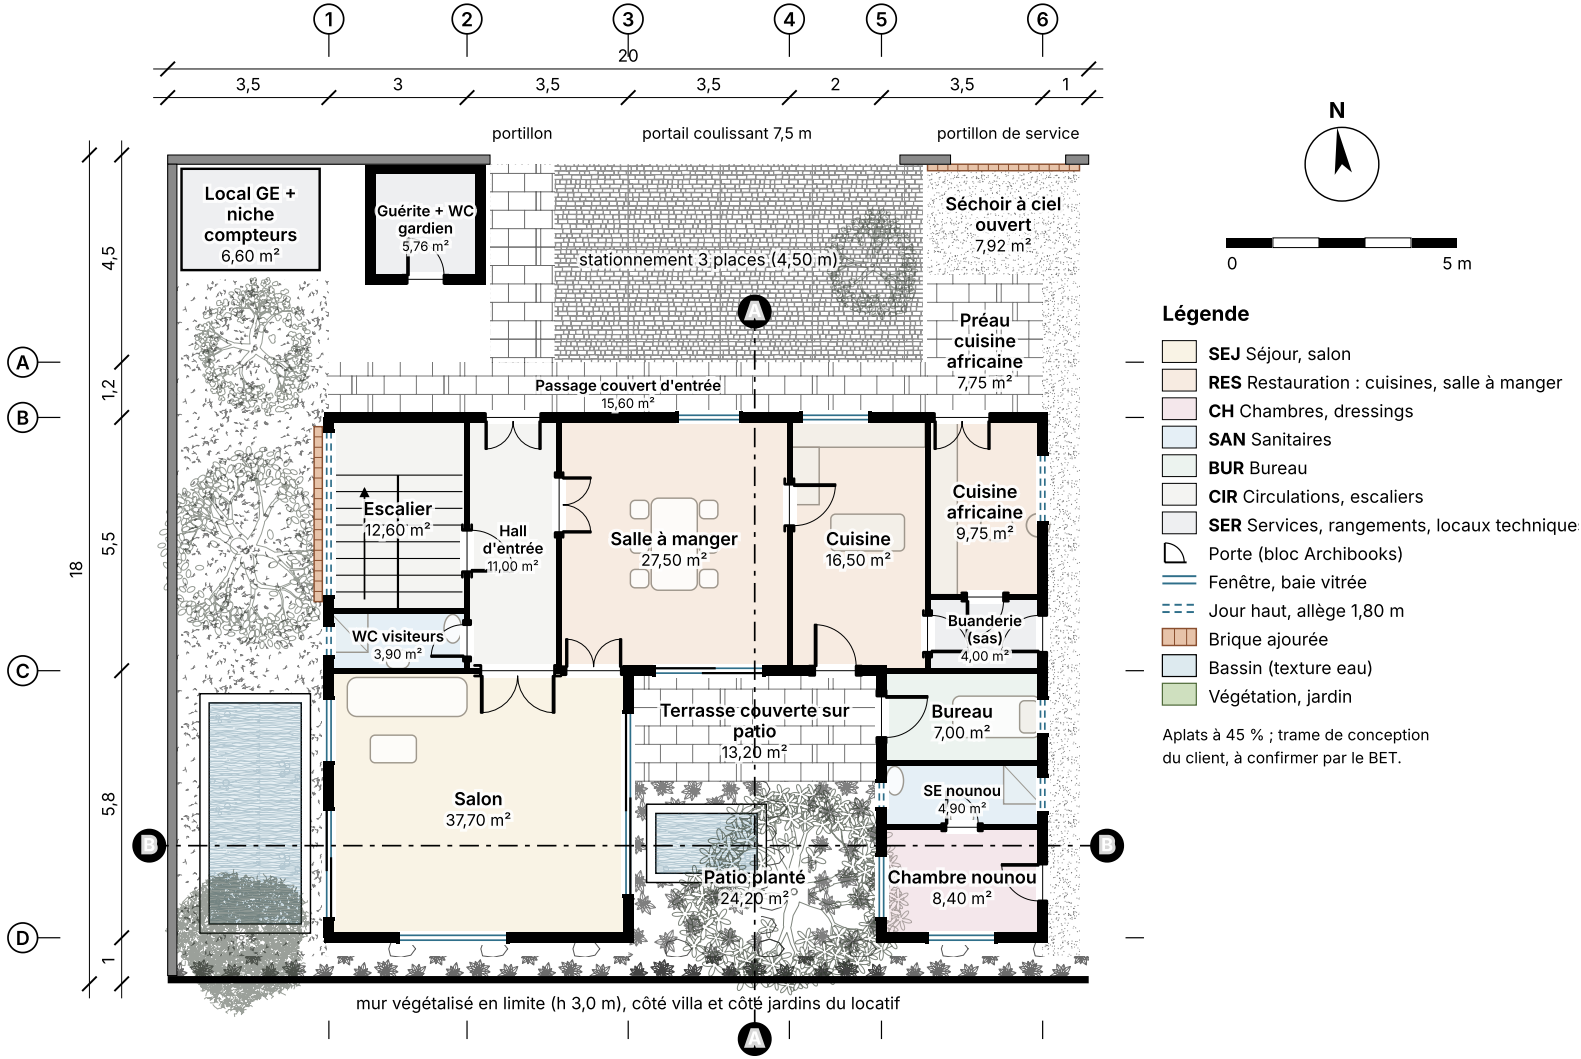

Lot 1728 · Riviera Palmeraie Villa à patio, option C v4	**Plan rez-de-chaussée** Villa, option C v4	Échelle graphique (1:100 en A3) Esquisse · indice B · 07-11-2026	Blocs et conventions : Capitude Archibooks (bucket privé)

Étage · 126,55 m² clos

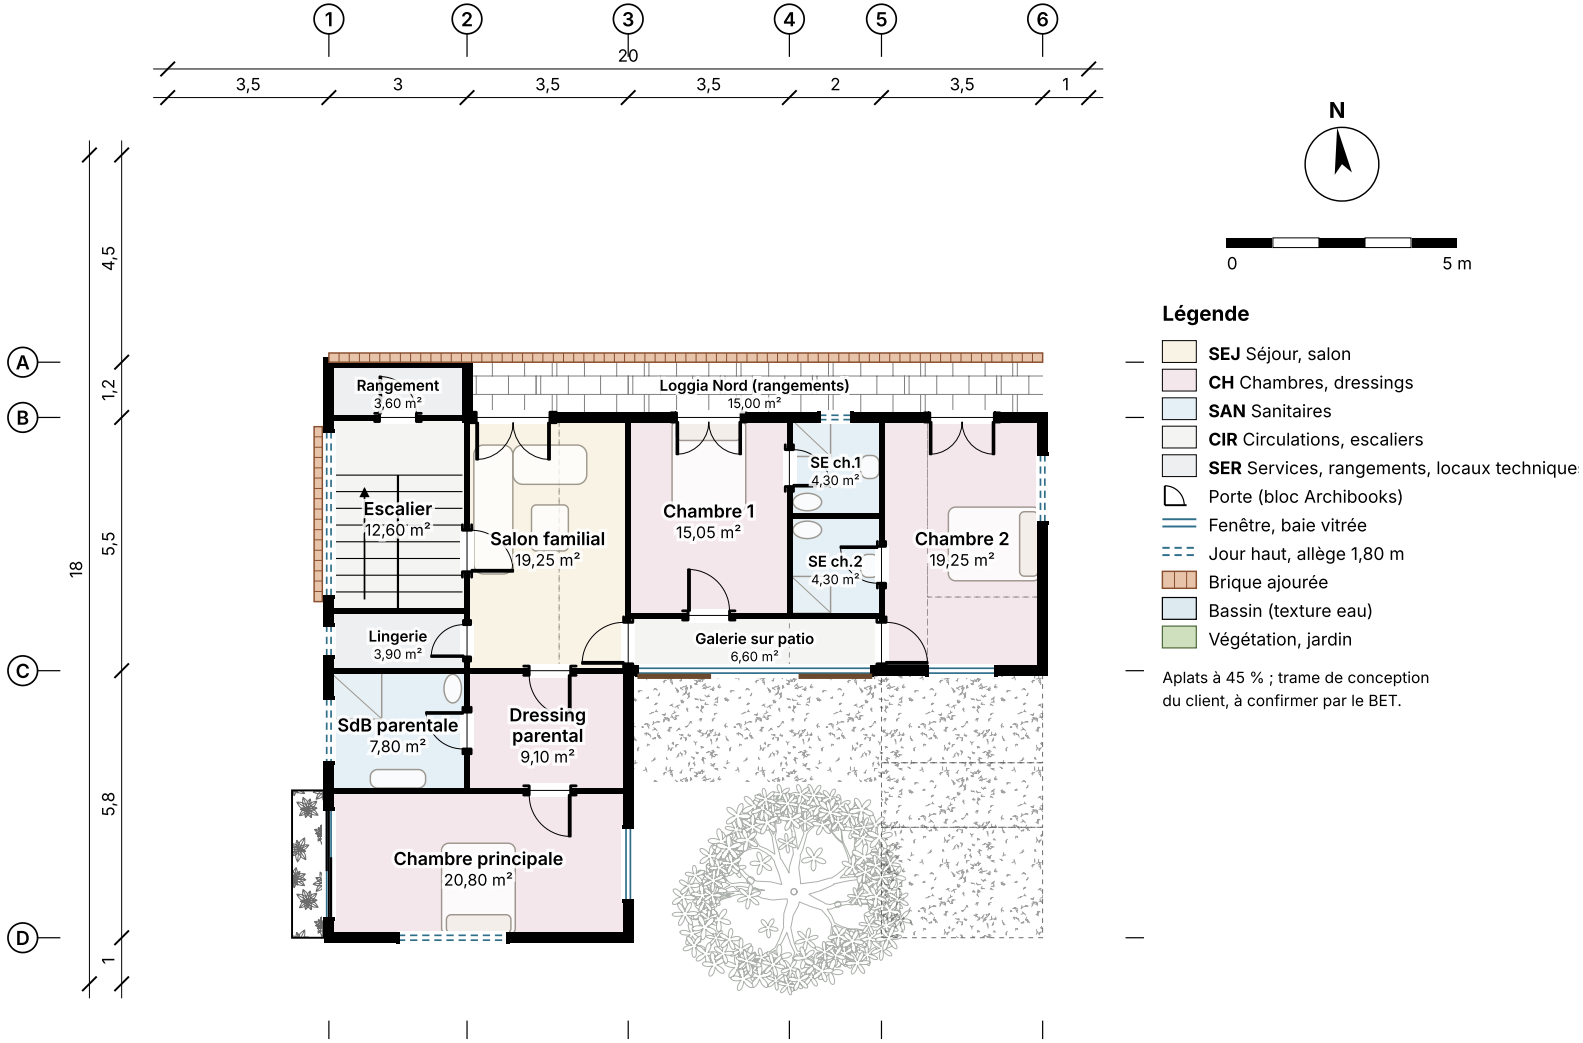


Légende

- **SEJ** Séjour, salon
- **CH** Chambres, dressings
- **SAN** Sanitaires
- **CIR** Circulations, escaliers
- **SER** Services, rangements, locaux technique
- Porte (bloc Archibooks)
- Fenêtre, baie vitrée
- Jour haut, allège 1,80 m
- Brique ajourée
- Bassin (texture eau)
- Végétation, jardin

Aplats à 45 % ; trame de conception du client, à confirmer par le BET.

Lot 1728 · Riviera Palmeraie Villa à patio, option C v4	**Plan étage** Villa, option C v4	Échelle graphique (1:100 en A3) Esquisse · indice B · 07-11-2026	Blocs et conventions : Capitude Archibooks (bucket privé)


Niveau pergola · toit-terrasse de 110 m² sous pergola

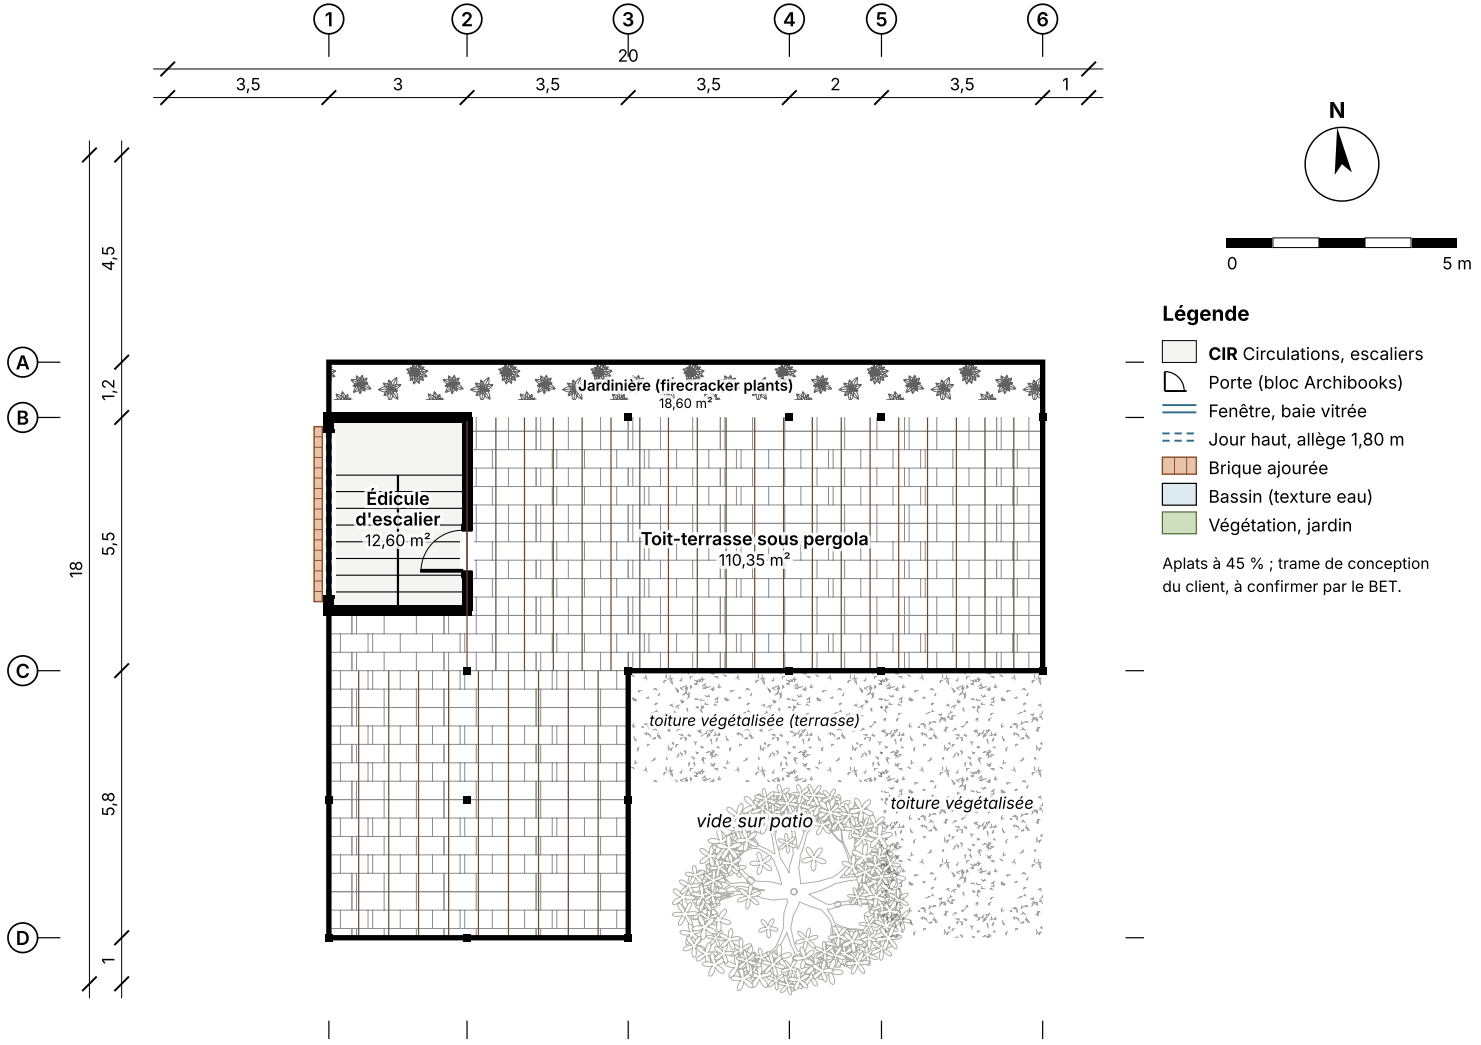

Lot 1728 · Riviera Palmeraie Villa à patio, option C v4	**Plan niveau pergola** Villa, option C v4	Échelle graphique (1:100 en A3) Esquisse · indice B · 07-11-2026	Blocs et conventions : Capitude Archibooks (bucket privé)

Coupes AA et BB

Coupe AA, Nord-Sud : SAM, chambre 1, terrasse, patio et mur végétalisé (vue vers l'Ouest)

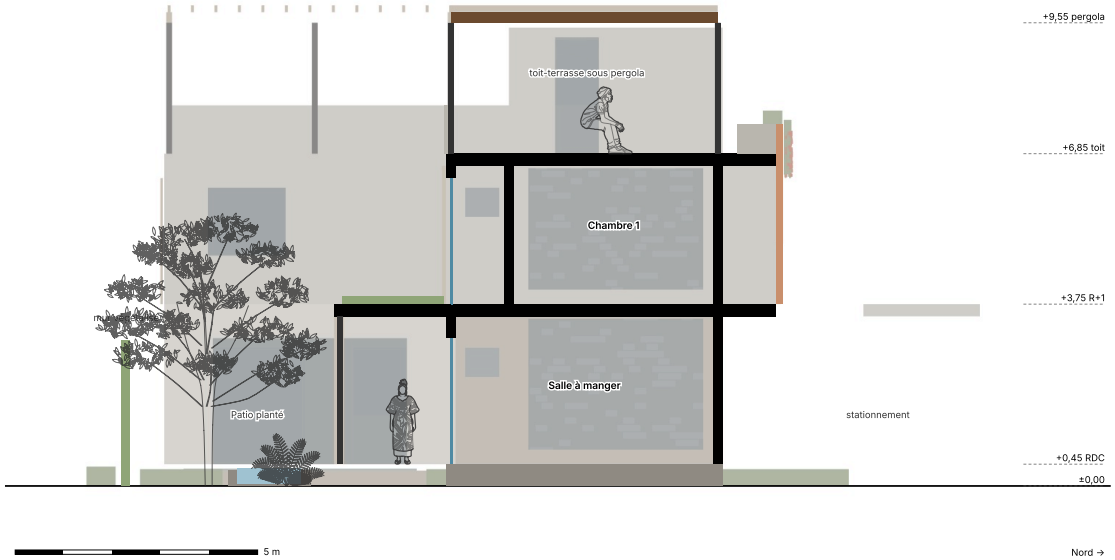

Coupe BB, Est-Ouest : bio-bassin, salon, chambre principale, patio, chambre nounou (vue vers le Nord)




Socle à +0,45 m. Étage à 3,30 m : 3,05 m sous plafond au RDC, 2,85 m à l'étage. Toit-terrasse à +6,85 m, acrotère de 1,00 m, pergola à +9,55 m.

En noir les murs et dalles coupés, en bleu les vitrages, en terre cuite la double peau ; au-delà, la maquette. Végétation et personnages : blocs Archibooks de coupe.


La double peau semi-perforée : deux propositions

Façade Nord, variante 1 : brique semi-perforée

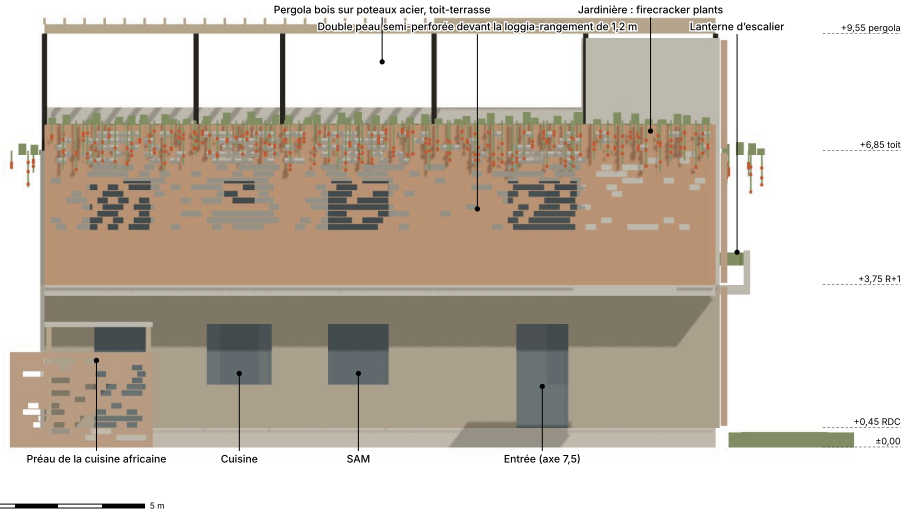

V1 · Brique de terre cuite semi-perforée (Casa Estudio, Capitude). Allège pleine de 1,10 m, puis perforations aléatoires plus serrées dans l'axe des baies ; brique locale de 22 × 10,5 × 6 cm posée en panneresse, joints creux. Laisse passer l'air et la lumière, cache la loggia.

Façade Nord, variante 2 : résille de béton triangulée

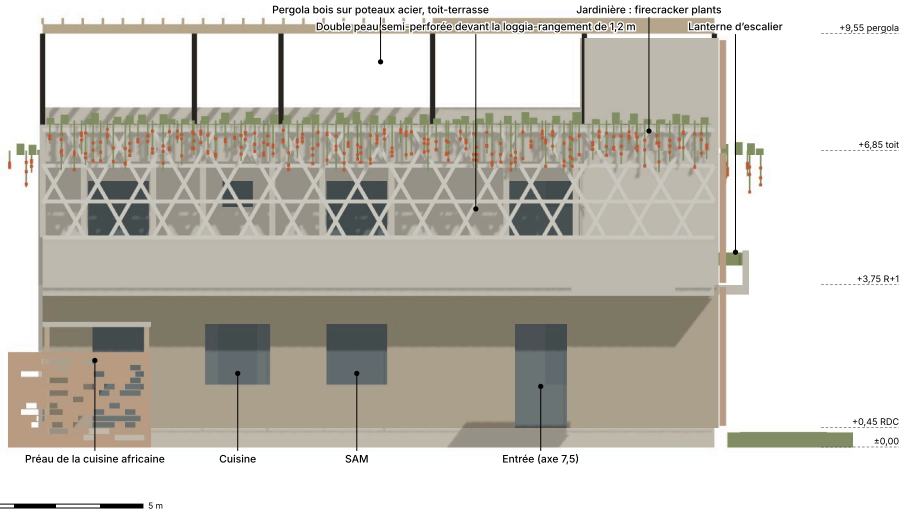

V2 · Résille de béton triangulée (Typologie urbaine 8, Capitude). Allège pleine de 1,10 m en béton brut, puis résille préfabriquée en triangles de 1,0 m sur des montants alignés sur les axes des baies. Plus ouverte, plus graphique ; ombres portées très dessinées.




V1 : arrivée depuis la rue Nord, rendu d'ambiance IA.




V2 : même vue, résille de béton, rendu d'ambiance IA.

Façades Ouest, Sud et Est


Façade Ouest, sur la rue latérale

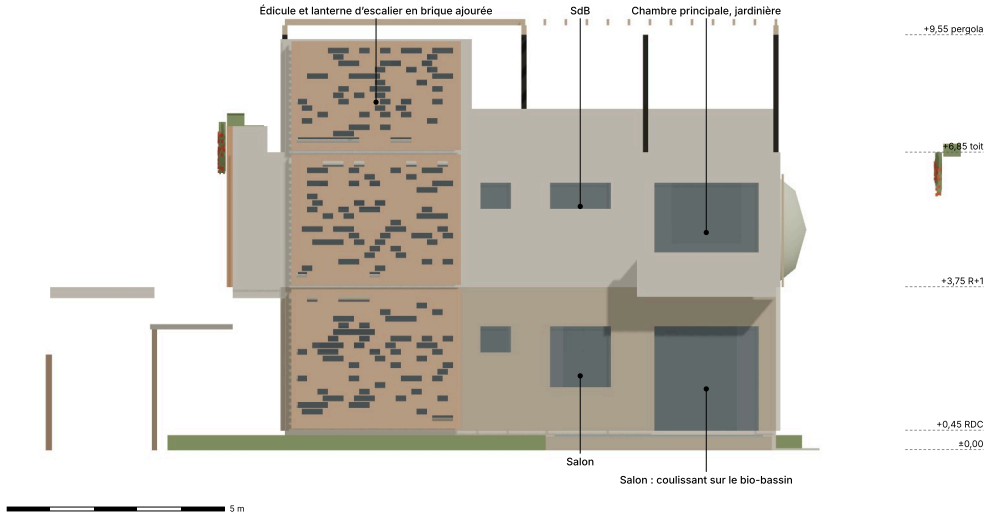

Façade Sud, sur le mur végétalisé

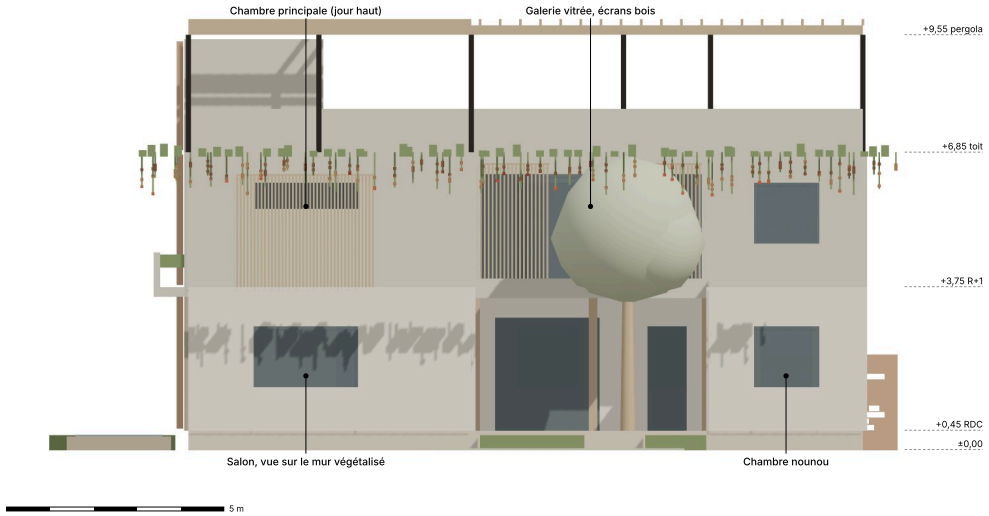

Façade Est, en limite à 1 m

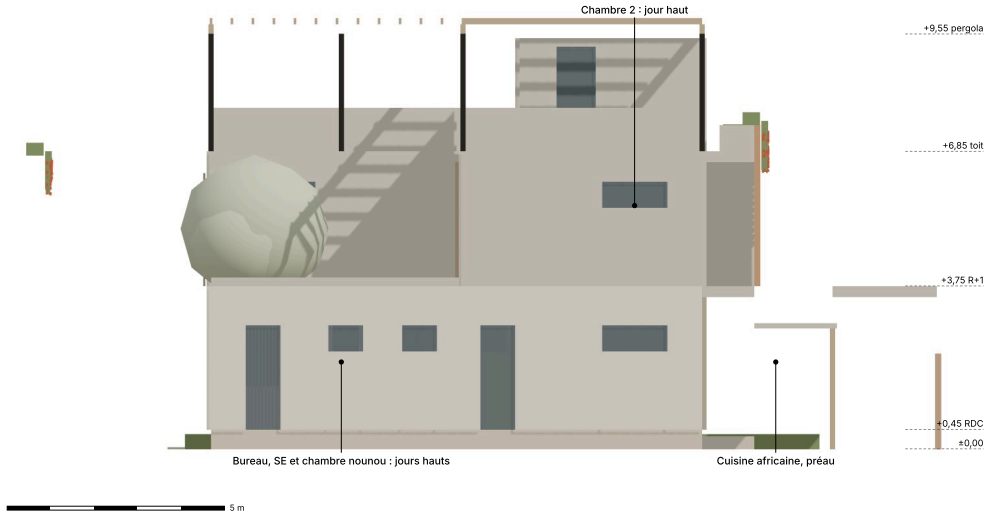

Alignements. Axes verticaux communs aux niveaux (Nord 7,5 / 11,75 / 14,5 / 17,25 ; Ouest 7,8 / 12,5 / 15,4) ; linteaux à 2,40 m ; allèges à 1,00 m (fenêtres) et 1,80 m (jours hauts).

Est à 1 m de la limite : jours hauts seulement. **Sud** sur le mur végétalisé : la chambre principale garde un jour haut au-dessus du lit. **Ouest** : la lanterne d'escalier en brique monte jusqu'à l'édicule du toit.

Élévations tirées de la maquette 3D, clôtures et arbres masqués, lumière conventionnelle à 45°.

La maison plongée dans la verdure



Le patio à 8 h 30 : terrasse couverte, frangipanier, bio-bassin, galerie vitrée à écrans bois, mur végétalisé au fond.



Le toit-terrasse sous la pergola, jardinière de firecracker plants sur la façade Nord.

Mur végétalisé

En limite villa / locatif sur 20 m, 3 m de haut : treillis inox, jardinières et goutte-à-goutte, plantes grimpantes et retombantes ; il ferme le patio au Sud et donne aux jardins des maisons une vue verte.

Firecracker plants

Russelia equisetiformis : tiges fines retombantes, fleurs tubulaires rouge orangé presque toute l'année, plein soleil, peu d'eau. Jardinière continue de 15,5 m en tête de la façade Nord, et sur chaque maison.

Patio et bassins

Frangipanier repère, sous-strate tropicale, pas japonais vers le fond, bio-bassin à recirculation ; bio-bassin Ouest devant le coulissant du salon. Pas d'eau stagnante (moustiques) : pompe et plantes épuratrices.

8 · VUES

Depuis la rue et l’angle des deux voies




Depuis le carrefour Nord-Ouest, 16 h 30 : clôture en moellons et brique ajourée, lanterne d’escalier, pergola.



Arrivée par temps gris d’août, variante 1 de la double peau.

Rendus d’ambiance générés par IA (Higgsfield, Nano Banana Pro) à partir des maquettes de volumes : la géométrie est imposée, les matières, la végétation et les personnages sont interprétés. Images indicatives.

Axonométries

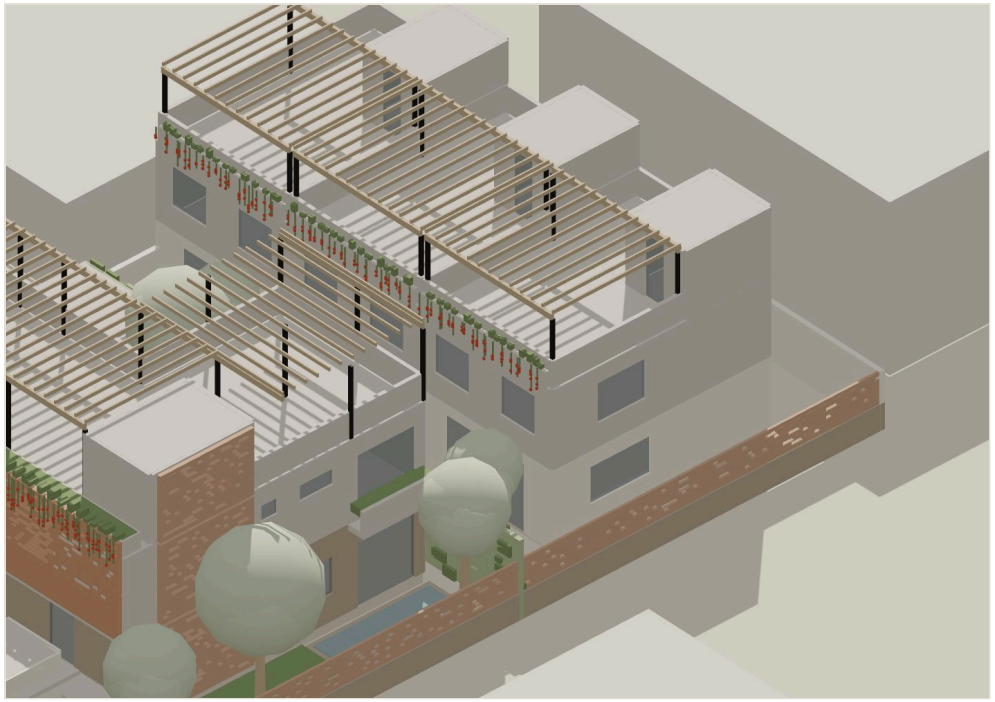



Ensemble depuis le Nord-Ouest : villa, patio, pergolas et trois maisons au fond.



Les trois maisons depuis le Sud-Ouest : stationnement, édicules et pergolas.

Trois maisons duplex · rez-de-chaussée

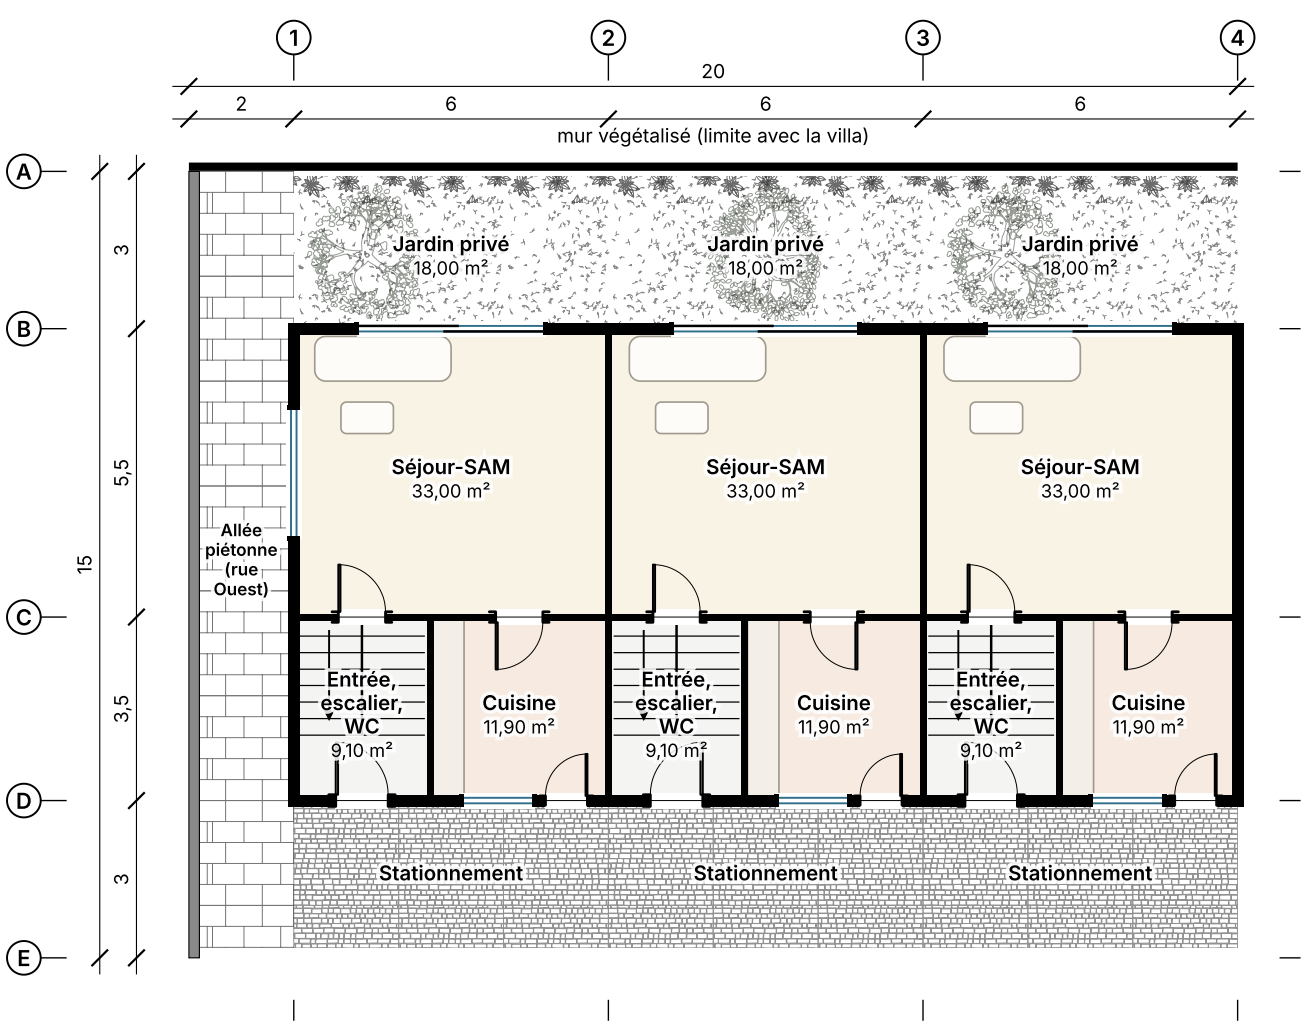

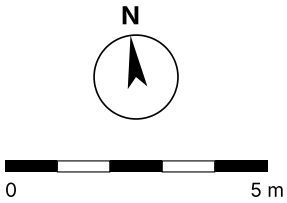


Légende

- **SEJ** Séjour, salon
- **RES** Restauration : cuisines, salle à manger
- **CIR** Circulations, escaliers
- Porte (bloc Archibooks)
- Fenêtre, baie vitrée
- Jour haut, allège 1,80 m
- Brique ajourée
- Bassin (texture eau)
- Végétation, jardin

Aplats à 45 % ; trame de conception du client, à confirmer par le BET.


Lot 1728 · Riviera Palmeraie Villa à patio, option C v4	**Plan du rez-de-chaussée** Locatif, 3 maisons	Échelle graphique (1:100 en A3) Esquisse · indice B · 07-11-2026	Blocs et conventions : Capitude Archibooks (bucket privé)

Trois maisons duplex · étage

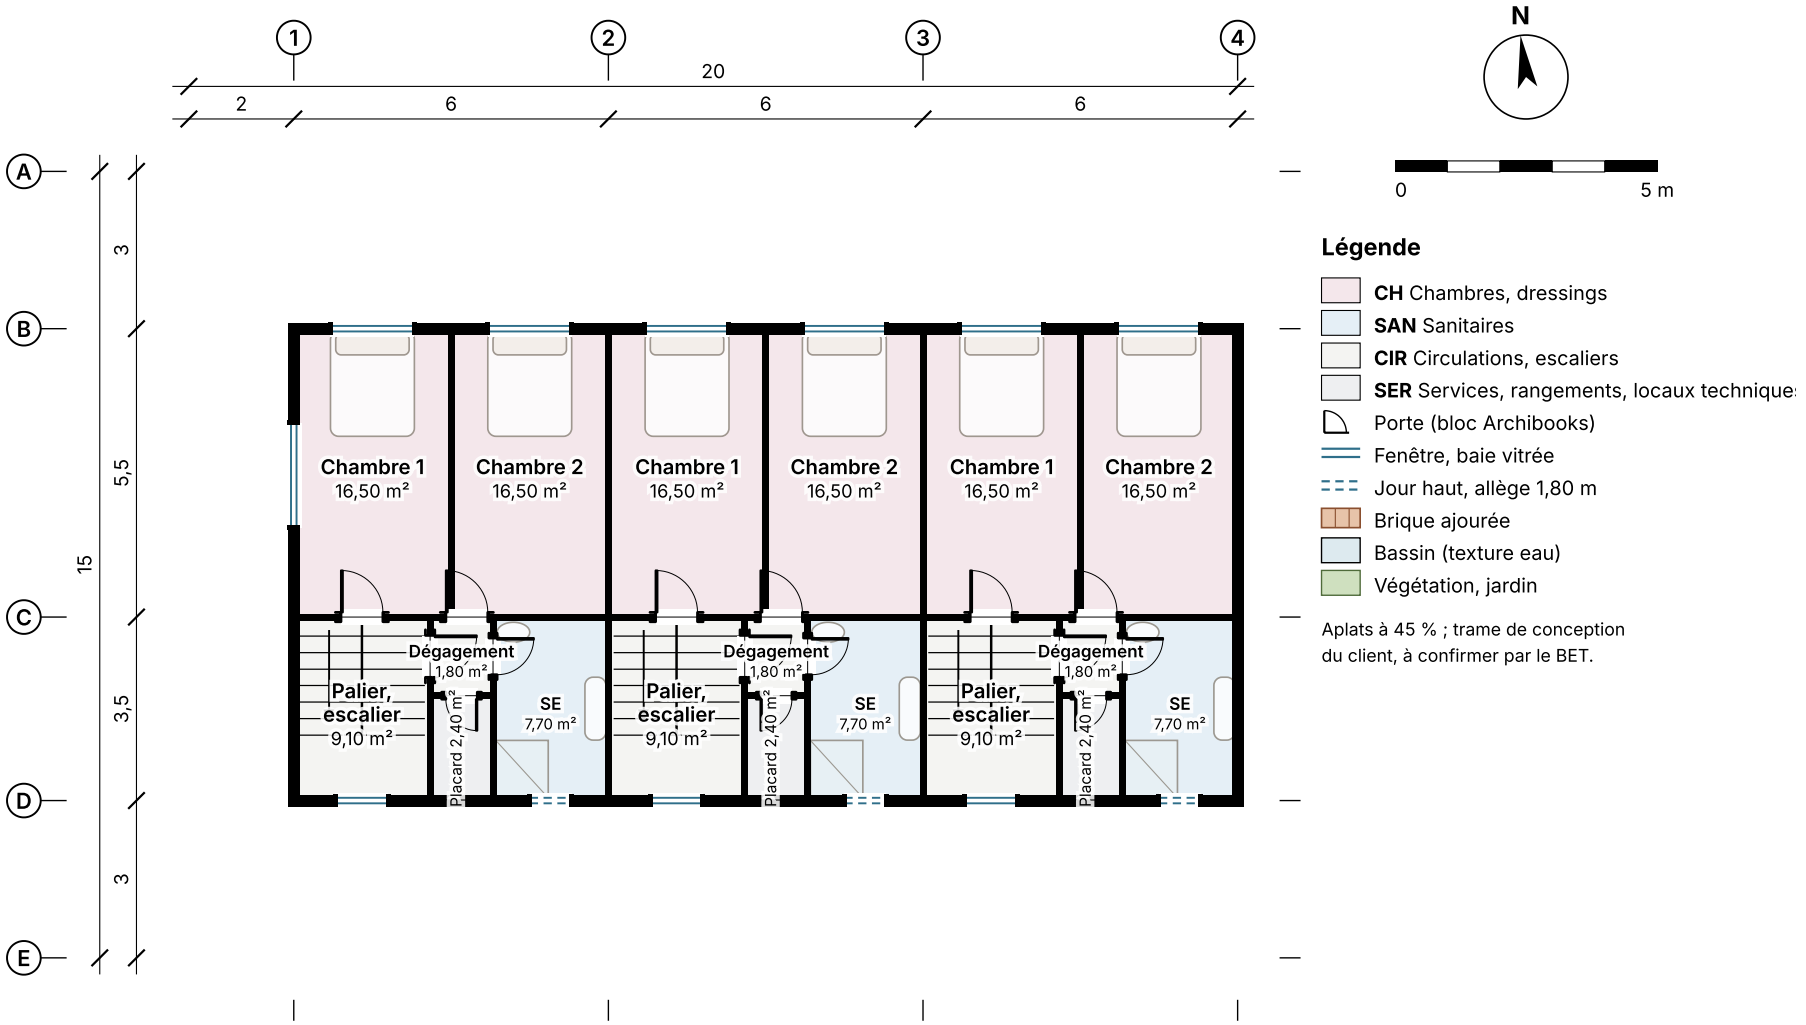

Lot 1728 · Riviera Palmeraie Villa à patio, option C v4	**Plan étage** Locatif, 3 maisons	Échelle graphique (1:100 en A3) Esquisse · indice B · 07-11-2026	Blocs et conventions : Capitude Archibooks (bucket privé)


Trois maisons duplex · niveau pergola

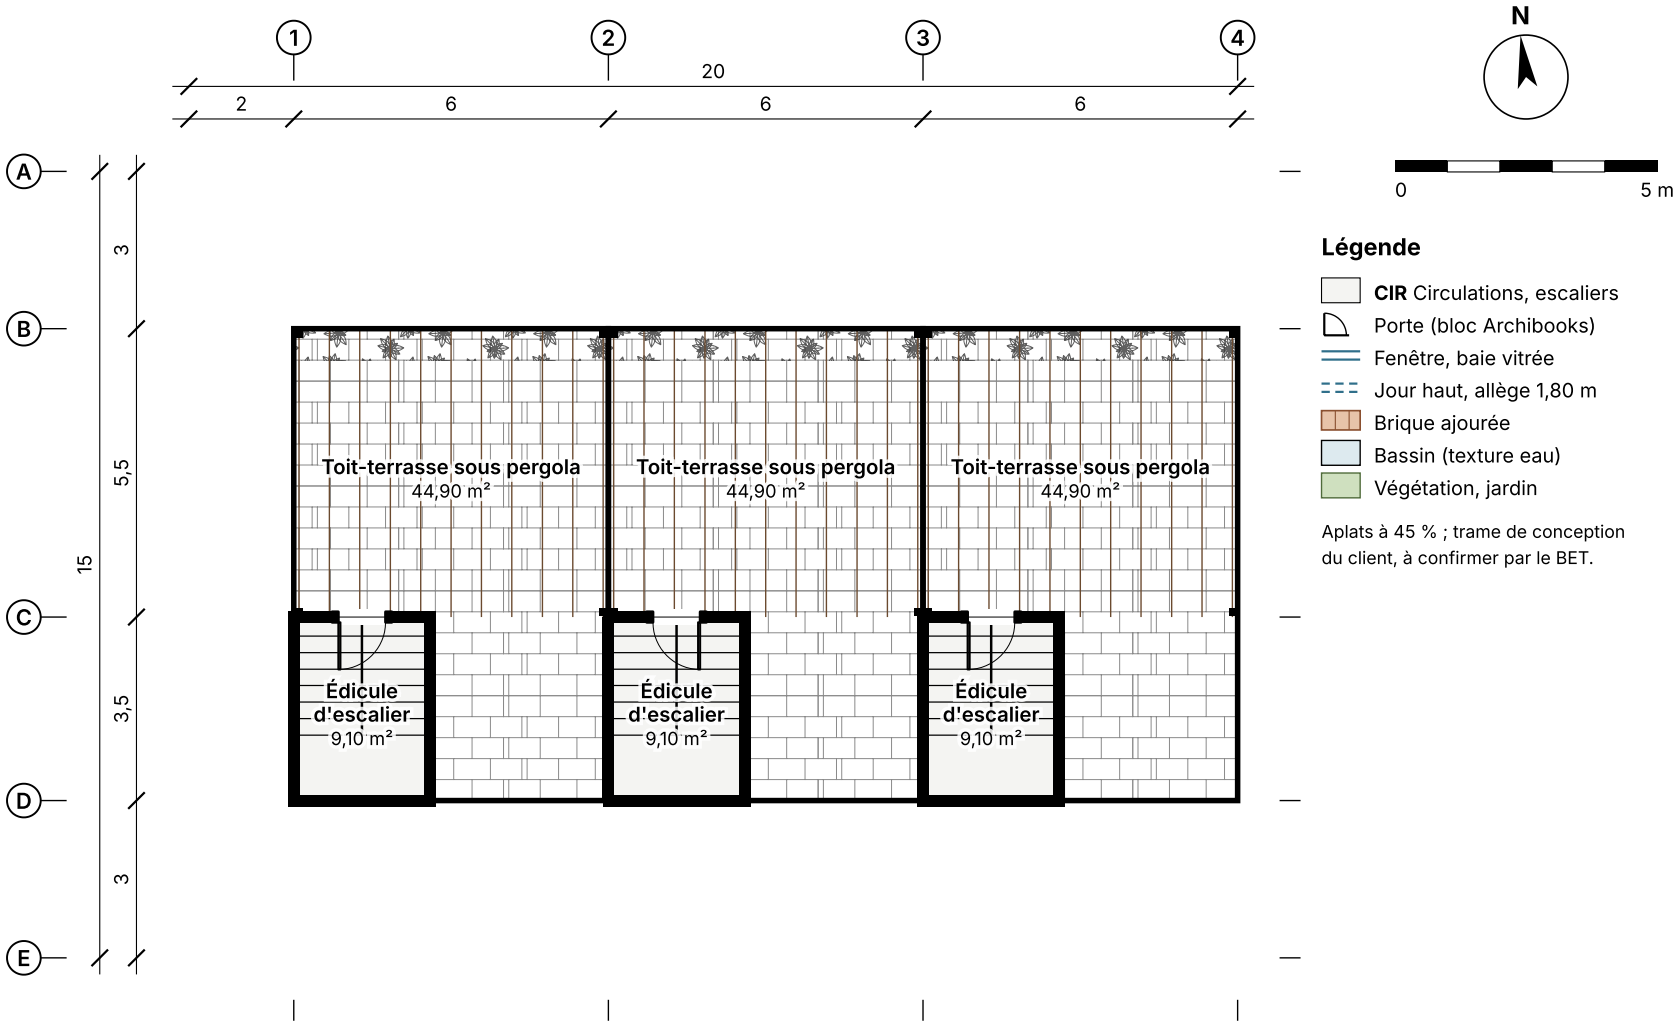

Lot 1728 · Riviera Palmeraie Villa à patio, option C v4	**Plan niveau pergola** Locatif, 3 maisons	Échelle graphique (1:100 en A3) Esquisse · indice B · 07-11-2026	Blocs et conventions : Capitude Archibooks (bucket privé)

Coupe et programme des maisons

Coupe CC, Nord-Sud sur la maison 2 : jardin, séjour, cuisine, chambre, SE, toit-terrasse

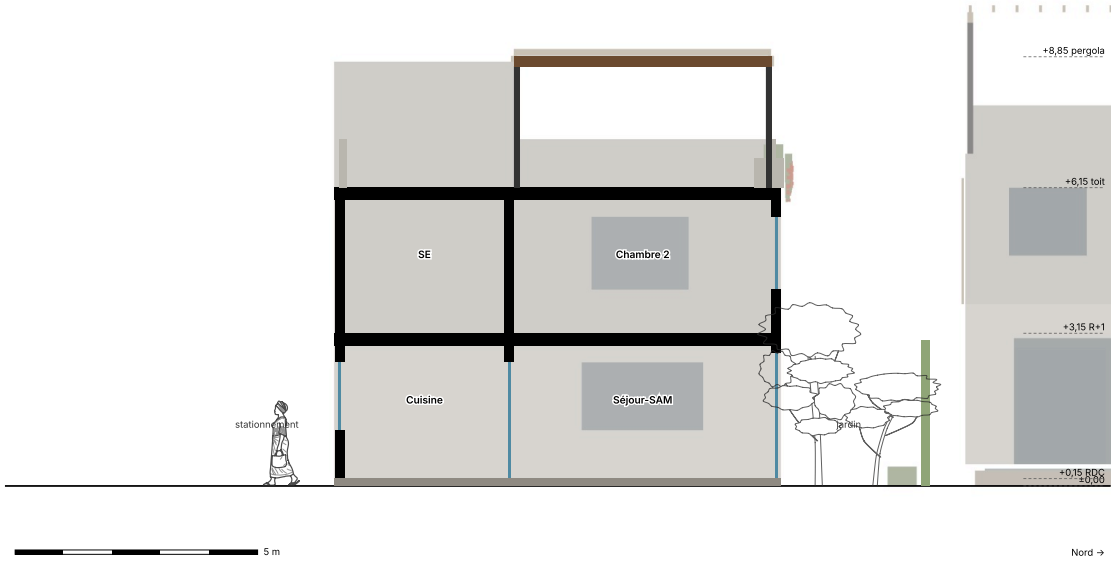

Une maison de 6 × 9 m sur deux niveaux

- RDC : séjour-SAM de 33 m² ouvert sur le jardin privé de 18 m², cuisine de 11,9 m² avec porte de service, entrée, escalier et WC.
- Étage : deux chambres de 16,5 m², SE de 7,7 m², placard, dégagement.
- Toit-terrasse de 45 m² sous pergola, jardinière de firecracker plants sur la façade Nord.
- Stationnement : une place par maison dans la bande de 3 m au Sud, accès par la rue Ouest.

> **À arbitrer** : en 3 m de large, les trois places sont en enfilade et se bloquent. Variantes : places sur la rue Ouest, ou bande portée à 5,5 m au détriment des cuisines.

Loyer de marché retenu pour un duplex 2 chambres avec jardin et toit-terrasse : **450 000 FCFA/mois** nu (hypothèse à valider avec deux agences). Le business plan (document 3) sera mis à jour sur cette base.

Tableau des surfaces de la villa · 275,56 m² clos

Pièce	Usage	m²
Rez-de-chaussée		
Guérite + WC gardien	SER	5,76
Local GE + niche compteurs (hors clos)	ext.	6,60
Passage couvert d'entrée (hors clos)	ext.	15,60
Escalier	CIR	12,60
WC visiteurs	SAN	3,90
Hall d'entrée	CIR	11,00
Salle à manger	RES	27,50
Cuisine	RES	16,50
Cuisine africaine	RES	9,75
Buanderie (sas)	SER	4,00
Salon	SEJ	37,70
Terrasse couverte sur patio (hors clos)	ext.	13,20
Patio planté (hors clos)	ext.	24,20
Bureau	BUR	7,00
SE nounou	SAN	4,90
Chambre nounou	CH	8,40
Préau cuisine africaine (hors clos)	ext.	7,75
Séchoir à ciel ouvert (hors clos)	ext.	7,92
Surface close rez-de-chaussée		**149,01**

Pièce	Usage	m²
Étage		
Rangement	SER	3,60
Loggia Nord (rangements) (hors clos)	ext.	15,00
Escalier	CIR	12,60
Lingerie	SER	3,90
Salon familial	SEJ	19,25
Chambre 1	CH	15,05
SE ch.1	SAN	4,30
SE ch.2	SAN	4,30
Galerie sur patio	CIR	6,60
Chambre 2	CH	19,25
SdB parentale	SAN	7,80
Dressing parental	CH	9,10
Chambre principale	CH	20,80
Jardinière Ouest (hors clos)	ext.	2,56
Surface close étage		**126,55**
Niveau pergola (toit-terrasse)		
Édicule d'escalier	CIR	12,60
Toit-terrasse sous pergola (hors clos)	ext.	110,35
Jardinière (firecracker plants) (hors clos)	ext.	18,60

Locatif et récapitulatif

Une maison (× 3) · 108,00 m² clos

Pièce	Usage	m²
Rez-de-chaussée		
M1 Séjour-SAM	SEJ	33,00
M1 Entrée, escalier, WC	CIR	9,10
M1 Cuisine	RES	11,90
M1 Jardin privé (hors clos)	ext.	18,00
M1 Stationnement (hors clos)	ext.	18,00
Allée piétonne (rue Ouest) (hors clos)	ext.	30,00
Surface close rez-de-chaussée		**54,00**
Étage		
M1 Chambre 1	CH	16,50
M1 Chambre 2	CH	16,50
M1 Palier, escalier	CIR	9,10
M1 Dégagement	CIR	1,80
M1 Placard	SER	2,40
M1 SE	SAN	7,70
Surface close étage		**54,00**
Niveau pergola (toit-terrasse)		
M1 Édicule d'escalier	CIR	9,10
M1 Toit-terrasse sous pergola (hors clos)	ext.	44,90

Récapitulatif	m²
Villa, surface close	275,56
Villa, emprise (hors guérite et local GE)	143,25
Villa, extérieurs couverts (passage, loggia, terrasse, préau, jardinière)	54,11
Villa, toit-terrasse sous pergola	110,35
Locatif, surface close (3 maisons)	324,00
Locatif, emprise	162,00
Locatif, toits-terrasses (3 × 44,9)	134,70
Total clos de l'opération	**599,56**

Villa, option C v4 : estimation par pièce et par poste

Ratios par type de pièce de la base Éco-données (Pavillon Akpo 2022, Résidences Anthurium 2021, Les Flamboyants, Villa Cacao 6), **divisés par 2** sur votre consigne ; postes hors base au prix du marché, sans division. Montants en FCFA HT.

Désignation	Ratio ou source	Qté	PU HT	Total HT
Rez-de-chaussée				
Guérite + WC gardien	Réserve / buanderie / cellier	5,76 m²	250 000	1 440 000
Local GE + niche compteurs	Réserve / buanderie / cellier	6,60 m²	250 000	1 650 000
Passage couvert d'entrée	Terrasse couverte / galerie	15,60 m²	175 000	2 730 000
Escalier	Escalier	12,60 m²	300 000	3 780 000
WC visiteurs	Salles d'eau / SdB / WC	3,90 m²	750 000	2 925 000
Hall d'entrée	Circulations (hall, dégagements, palier)	11,00 m²	275 000	3 025 000
Salle à manger	Séjour / SAM / salon	27,50 m²	300 000	8 250 000
Cuisine	Cuisine	16,50 m²	425 000	7 012 500
Cuisine africaine	Cuisine africaine (carrelée, ventilée)	9,75 m²	425 000	4 143 750
Buanderie (sas)	Réserve / buanderie / cellier	4,00 m²	250 000	1 000 000
Salon	Séjour / SAM / salon	37,70 m²	300 000	11 310 000
Terrasse couverte sur patio	Terrasse couverte / galerie	13,20 m²	175 000	2 310 000
Patio planté	Cour de service / séchoir / patio	24,20 m²	42 500	1 028 500
Bureau	Chambres	7,00 m²	300 000	2 100 000
SE nounou	Salles d'eau / SdB / WC	4,90 m²	750 000	3 675 000
Chambre nounou	Chambres	8,40 m²	300 000	2 520 000
Préau cuisine africaine	Terrasse couverte / galerie	7,75 m²	175 000	1 356 250
Séchoir à ciel ouvert	Cour de service / séchoir / patio	7,92 m²	42 500	336 600
Sous-total rez-de-chaussée				**60 592 600**
Étage				
Rangement	Dressing / placards	3,60 m²	425 000	1 530 000
Loggia Nord (rangements)	Balcon d'étage	15,00 m²	225 000	3 375 000
Escalier	Escalier	12,60 m²	300 000	3 780 000
Lingerie	Dressing / placards	3,90 m²	425 000	1 657 500
Salon familial	Séjour / SAM / salon	19,25 m²	300 000	5 775 000
Chambre 1	Chambres	15,05 m²	300 000	4 515 000

Villa, option C v4 : estimation par pièce et par poste

Désignation	Ratio ou source	Qté	PU HT	Total HT
SE ch.1	Salles d'eau / SdB / WC	4,30 m²	750 000	3 225 000
SE ch.2	Salles d'eau / SdB / WC	4,30 m²	750 000	3 225 000
Galerie sur patio	Circulations (hall, dégagements, palier)	6,60 m²	275 000	1 815 000
Chambre 2	Chambres	19,25 m²	300 000	5 775 000
SdB parentale	Salles d'eau / SdB / WC	7,80 m²	750 000	5 850 000
Dressing parental	Dressing / placards	9,10 m²	425 000	3 867 500
Chambre principale	Chambres	20,80 m²	300 000	6 240 000
Jardinière Ouest	Balcon d'étage	2,56 m²	225 000	576 000
Sous-total étage				**51 206 000**
Niveau pergola				
Édicule d'escalier	Escalier	12,60 m²	300 000	3 780 000
Toit-terrasse sous pergola	Toit-jardin accessible	110,35 m²	175 000	19 311 250
Jardinière (firecracker plants)	Espaces verts (aménagement)	18,60 m²	10 000	186 000
Sous-total niveau pergola				**23 277 250**
Aménagements extérieurs et VRD				
Parking, allée et aire de livraison pavés (pavés drainants)	base ÷ 2	60,00 m2	42 500	2 550 000
Jardins plantés (terre végétale, gazon, arbres d'ombrage)	base ÷ 2	70,00 m2	10 000	700 000
Bâche à eau + surpresseur	base ÷ 2	1,00 ens	2 023 538	2 023 538
Réfection clôture existante + portail coulissant + portillon	prix de marché	1,00 ens	3 000 000	3 000 000
Mur séparatif villa / locatif (h 2,5 m) + claustras de la cour de service	prix de marché	8,00 ml	60 000	480 000
Assainissement autonome (fosse + puisard) + branchements CIE / SODECI	prix de marché	1,00 ens	3 500 000	3 500 000
Traitement anti-termites du sol + remblai de plateforme	prix de marché	160,00 m2	8 000	1 280 000
Grilles de défense RDC et étage + moustiquaires	prix de marché	70,00 m2	45 000	3 150 000
Chauffe-eau solaires + attentes climatisation (par logement)	prix de marché	2,50 u	900 000	2 250 000
Cuisine africaine : hotte d'extraction, évier double bac, cage à bouteilles de gaz	prix de marché	1,00 ens	900 000	900 000
Sous-total				**19 833 538**
Plus-values du parti (matières, patio, toiture)				

Villa, option C v4 : estimation par pièce et par poste

Désignation	Ratio ou source	Qté	PU HT	Total HT
Menuiseries bois persiennées (jalousies) / écrans coulissants en lattes	prix de marché	12,00 m2	120 000	1 440 000
Claustras en terre cuite / BTC ajourée (cour de service, façades Ouest, coursive)	prix de marché	32,00 m2	30 000	960 000
Débords de toiture et casquettes (hors clos)	prix de marché	15,00 m2	60 000	900 000
Patio : arbre (frangipanier), massifs, bassin à recirculation, éclairage	prix de marché	1,00 ens	3 000 000	3 000 000
Patio : caniveau grillé périphérique + exutoire	prix de marché	1,00 ens	1 200 000	1 200 000
Double peau en brique de terre cuite à perforations aléatoires (loggia Nord, lanterne d'escalier, balcon Ouest)	prix de marché	57,00 m2	38 000	2 166 000
Plus-value parement en moellons de granite (RDC sur rues, guérite, socle de clôture)	prix de marché	100,00 m2	28 000	2 800 000
Plus-value béton brut coffré planches (nez de dalle, corniches à goutte d'eau, porche)	prix de marché	60,00 m2	15 000	900 000
Toiture végétalisée extensive (substrat 15 cm, drainage, étanchéité anti-racines) + jardinières de rive	prix de marché	33,50 m2	25 000	837 500
Bio-bassin devant le salon (bande Ouest) : margelle pierre, étanchéité, plantes épuratrices	prix de marché	1,00 ens	1 600 000	1 600 000
Écrans en lattes de bois de la passerelle et stores bambou sous débords Ouest	prix de marché	1,00 ens	900 000	900 000
Pergola bois sur poteaux acier, niveau toit-terrasse	prix de marché	110,00 m2	45 000	4 950 000
Jardinière continue en façade (firecracker plants, goutte-à-goutte)	prix de marché	15,50 ml	75 000	1 162 500
Mur végétalisé en limite villa / locatif (treillis inox, jardinières, arrosage)	prix de marché	60,00 m2	55 000	3 300 000
Garde-corps des toits-terrasses (acrotère 1,0 m + lisse)	prix de marché	45,00 ml	35 000	1 575 000
Local GE + niche compteurs (dalle, claustra, porte)	prix de marché	1,00 ens	1 200 000	1 200 000
Sous-total				**28 891 000**
TOTAL TRAVAUX HT				**183 800 388**
Honoraires architecte (conception + suivi)		8,00 %		14 704 031
BET structure / fluides		2,00 %		3 676 008
Étude géotechnique		1,50 %		2 757 006
Bureau de contrôle		1,35 %		2 481 305
Assurances (TRC / dommages)		1,20 %		2 205 605
Imprévus (stade esquisse)		10,00 %		18 380 039
TOTAL GÉNÉRAL HT				**228 004 382**
TVA		18 %		41 040 789
TOTAL GÉNÉRAL TTC				**269 045 171**

Locatif, 3 maisons duplex : estimation

Ratios par type de pièce de la base Éco-données (Pavillon Akpo 2022, Résidences Anthurium 2021, Les Flamboyants, Villa Cacao 6), **divisés par 2** sur votre consigne ; postes hors base au prix du marché, sans division. Montants en FCFA HT.

Désignation	Ratio ou source	Qté	PU HT	Total HT
Rez-de-chaussée				
Séjour-SAM (× 3)	Séjour-cuisine (locatif)	99,00 m²	275 000	27 225 000
Entrée, escalier, WC (× 3)	Dégagement / placard / bureau	27,30 m²	200 000	5 460 000
Cuisine (× 3)	Kitchenette / bande humide	35,70 m²	425 000	15 172 500
Jardin privé (× 3)	Espaces verts (aménagement)	54,00 m²	10 000	540 000
Stationnement (× 3)	Parking et allées pavés	54,00 m²	42 500	2 295 000
Allée piétonne (rue Ouest)	Parking et allées pavés	30,00 m²	42 500	1 275 000
Sous-total rez-de-chaussée				**51 967 500**
Étage				
Chambre 1 (× 3)	Chambre / alcôve (locatif)	49,50 m²	250 000	12 375 000
Chambre 2 (× 3)	Chambre / alcôve (locatif)	49,50 m²	250 000	12 375 000
Palier, escalier (× 3)	Dégagement / placard / bureau	27,30 m²	200 000	5 460 000
Dégagement (× 3)	Dégagement / placard / bureau	5,40 m²	200 000	1 080 000
Placard (× 3)	Dégagement / placard / bureau	7,20 m²	200 000	1 440 000
SE (× 3)	Salle d'eau (locatif)	23,10 m²	500 000	11 550 000
Sous-total étage				**44 280 000**
Niveau pergola				
Édicule d'escalier (× 3)	Escalier	27,30 m²	300 000	8 190 000
Toit-terrasse sous pergola (× 3)	Toit-jardin accessible	134,70 m²	175 000	23 572 500
Sous-total niveau pergola				**31 762 500**
Aménagements extérieurs et VRD				
Bâche à eau + surpresseur	base ÷ 2	1,00 ens	2 023 538	2 023 538

Locatif, 3 maisons duplex : estimation

Désignation	Ratio ou source	Qté	PU HT	Total HT
Réfection clôture existante + portail coulissant + portillon	prix de marché	1,00 ens	3 000 000	3 000 000
Assainissement autonome (fosse + puisard) + branchements CIE / SODECI	prix de marché	1,50 ens	3 500 000	5 250 000
Traitement anti-termites du sol + remblai de plateforme	prix de marché	170,00 m2	8 000	1 360 000
Grilles de défense RDC et étage + moustiquaires	prix de marché	45,00 m2	45 000	2 025 000
Chauffe-eau solaires + attentes climatisation (par logement)	prix de marché	3,00 u	900 000	2 700 000
Sous-total				**16 358 538**
Plus-values du parti (matières, patio, toiture)				
Pergola bois sur poteaux acier, niveau toit-terrasse	prix de marché	99,00 m2	45 000	4 455 000
Jardinière continue en façade (firecracker plants, goutte-à-goutte)	prix de marché	18,00 ml	75 000	1 350 000
Garde-corps des toits-terrasses (acrotère 1,0 m + lisse)	prix de marché	72,00 ml	35 000	2 520 000
Sous-total				**8 325 000**
TOTAL TRAVAUX HT				**152 693 538**
Honoraires architecte (conception + suivi)		8,00 %		12 215 483
BET structure / fluides		2,00 %		3 053 871
Étude géotechnique		1,50 %		2 290 403
Bureau de contrôle		1,35 %		2 061 363
Assurances (TRC / dommages)		1,20 %		1 832 322
Imprévus (stade esquisse)		10,00 %		15 269 354
TOTAL GÉNÉRAL HT				**189 416 334**
TVA		18 %		34 094 940
TOTAL GÉNÉRAL TTC				**223 511 274**

Points à valider

À arbitrer avec vous

- Double peau : V1 brique semi-perforée ou V2 résille de béton
- Stationnement du locatif : places en enfilade ou sur la rue Ouest
- Ajustements de trame : stationnement 4,50 m, passages de 1 m
- Escalier ouvert vers le toit ou édicule fermé (pluie)

Technique et règlement

- Le niveau pergola n'est pas un étage clos : à confirmer au cahier des charges (hauteur, R+1)
- Étanchéité du toit-terrasse et des jardinières, arrosage goutte-à-goutte, trop-pleins
- Mur végétalisé mitoyen : convention avec le locatif, accès d'entretien
- Étude de sol G2, assainissement, cote d'inondation

Coût et bibliothèque

- Ratio ÷ 2 au bas de la fourchette : consultation par lots dès l'APS
- Postes au prix du marché de la villa : 28,9 M FCFA HT, à confirmer par devis
- Blocs à ajouter à Archibooks : sanitaires, lits, canapés, cuisines, voitures, cartouche