OPTION C · FAÇADES

Une écriture tirée d'ABYA 2 : une dalle qui fait de l'ombre, du bois qui filtre, de la terre qui ajoure

Pourquoi ABYA 2

Seule villa R+1 ivoirienne de la base dont les façades sont documentées (4 élévations, coupes, axonométrie, vues) ; même climat lagunaire ; mêmes hauteurs (étage +3,50 et toiture +6,60, contre +3,75 et +6,85 ici) ; vocabulaire simple et économique : une dalle, des poteaux, des persiennes, un claustra.

Toiture-ombrière débordante	Une seule dalle mince en béton blanc sur tout l'étage, débord de 1,6 m à l'Ouest, 1,2 m au Nord, 0,8 m à l'Est.
Persiennes bois coulissantes	Devant les baies de l'étage au Nord, à l'Est et au Sud : intimité côté rue, ventilation volets fermés.
Garde-corps à barreaudage	Portes-fenêtres du salon familial et de la chambre 2, comme les balcons d'ABYA 2.
Claustra de briques ajourées	Pour tout ce qui sert : cage d'escalier, aile de service, clôture. Ici en BTC, la terre du brief.
Séjour vitré sous débord	Coulissant de 3,2 m du salon à l'Ouest sous la dalle du balcon, baie de 4,0 m au Sud.

Compléments pris dans Capitude

- **CDD Cotonou** : claustra devant la cage d'escalier, qui devient la lanterne de l'angle des deux rues
- **Typologie urbaine 8** : double peau Ouest : le balcon de la suite derrière un claustra pleine hauteur
- **House on Pali Hill** : portail et portillons en planches de bois sur un socle minéral sombre



Arrivée depuis la rue Nord, portail ouvert, 8 h 30 en novembre (maquette de volumes, sans matières). À l'étage, les persiennes coulissantes et le barreaudage ; au rez-de-chaussée en BTC, le porche, la SAM et la cuisine sous une casquette de 0,9 m ; à droite la lanterne d'escalier en claustra et la guérite.

Matériaux

BTC apparents
Murs du rez-de-chaussée, claustras, clôture : terre stabilisée locale

Enduit blanc cassé
Murs de l'étage, sur maçonnerie de parpaings

Béton blanc lisse
Toiture-ombrière, casquettes, nez de dalle


Iroko ou teck
Persiennes coulissantes, portail, portillons, passerelle

Aluminium sombre
Menuiseries vitrées, barreaudage des portes-fenêtres


Socle minéral sombre
Soubassement de la clôture et de la maison (pierre ou laterite)

Élévations Nord et Ouest

Façade Nord, sur la rue d'accès

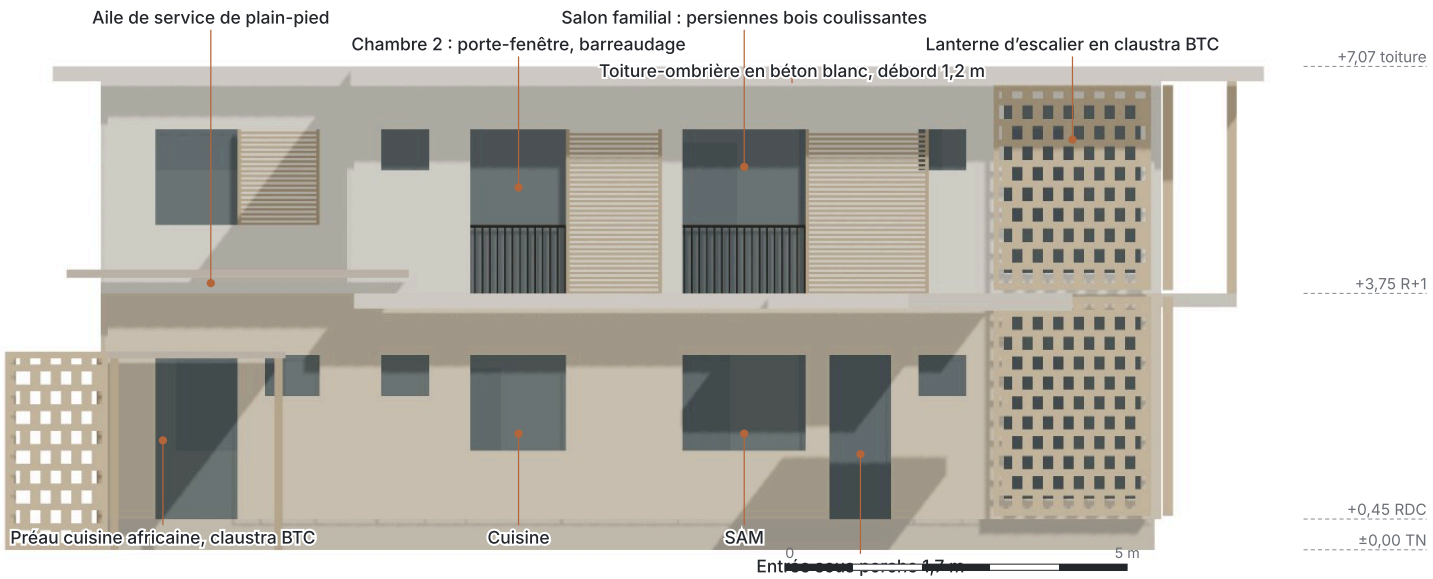

Façade Ouest, sur la rue latérale

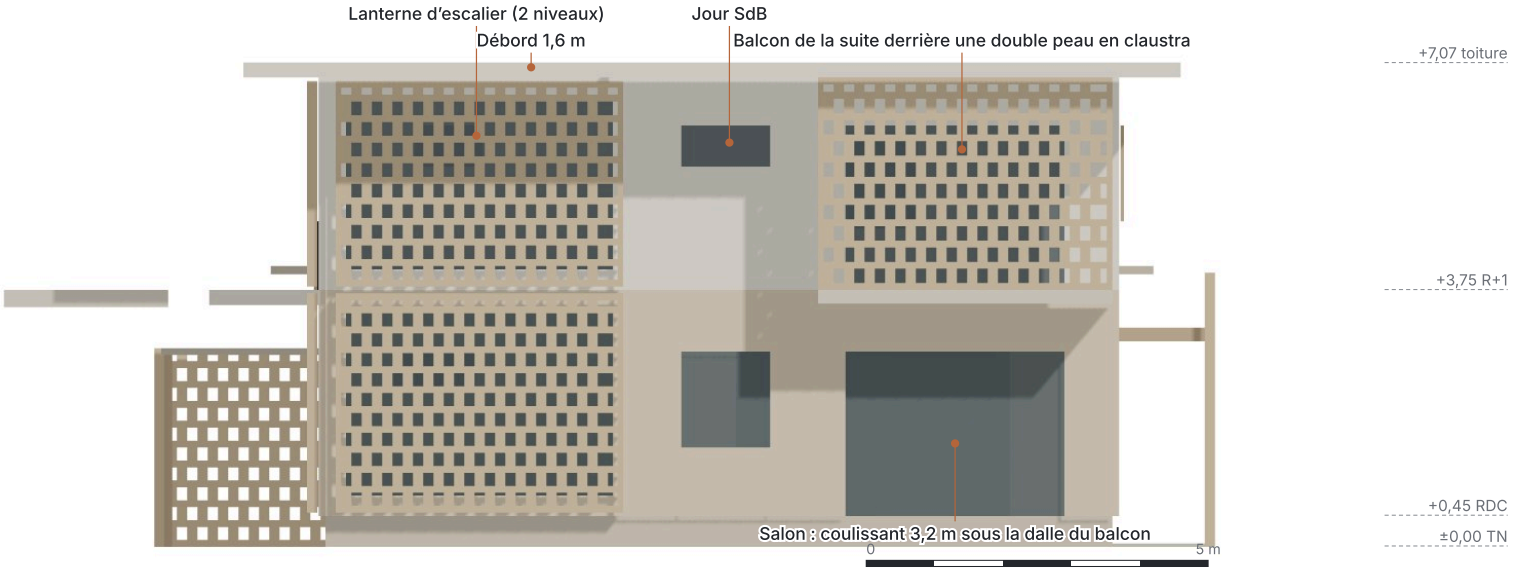


Rues au Nord et à l'Ouest. Au Nord, le soleil ne vient qu'en juin, haut (72° à midi) : le débord de 1,2 m ombre alors entièrement les baies de l'étage. À l'Ouest, le soleil de l'après-midi est rasant (19,5° à 16 h 30 en novembre) : aucun débord ne suffit, d'où la double peau en claustra devant la suite, les arbres de la bande de 3,2 m et des stores en toile ou en bambou pour le coulissant du salon.

Élévations tirées de la maquette 3D du modèle (ouvertures listées dans `facade.py`), clôtures, guérite et arbres masqués ; lumière conventionnelle à 45°.


Alignements. Axes verticaux communs au rez-de-chaussée et à l'étage (claustra d'escalier, baies, jours) ; linteaux à 2,40 m partout ; allèges à 1,00 m pour les fenêtres, 1,80 m pour les jours hauts, 0 pour les baies.

Élévations Sud et Est

Façade Sud, sur le jardin et le locatif

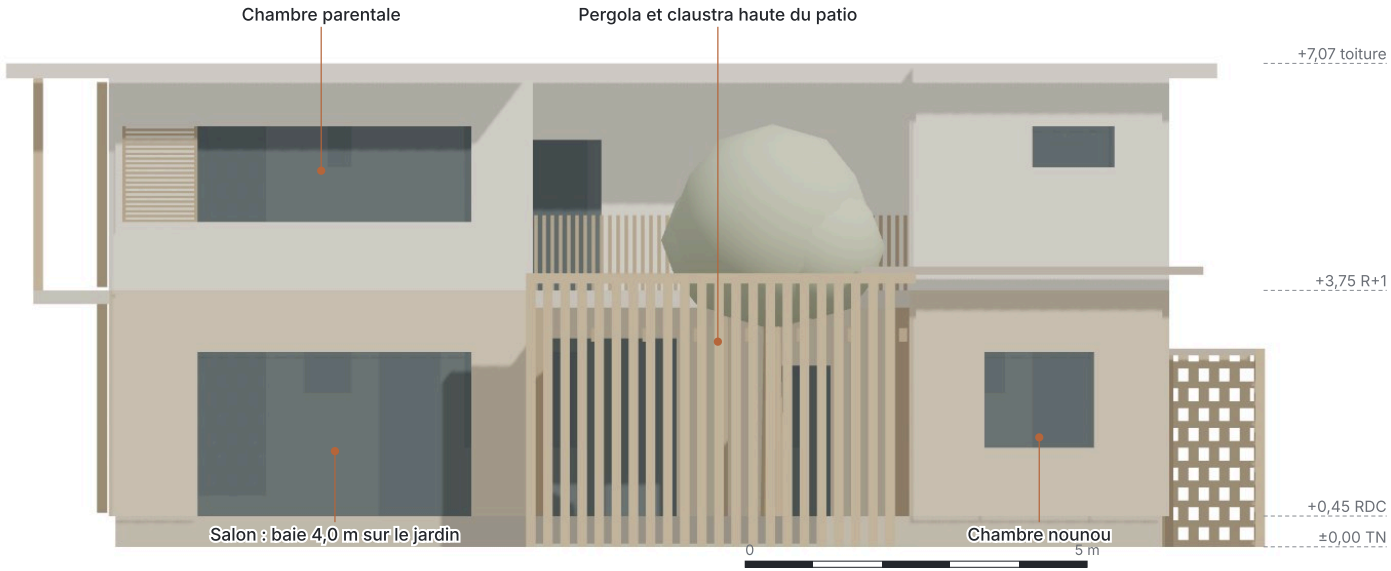

Façade Est, en limite à 1,50 m

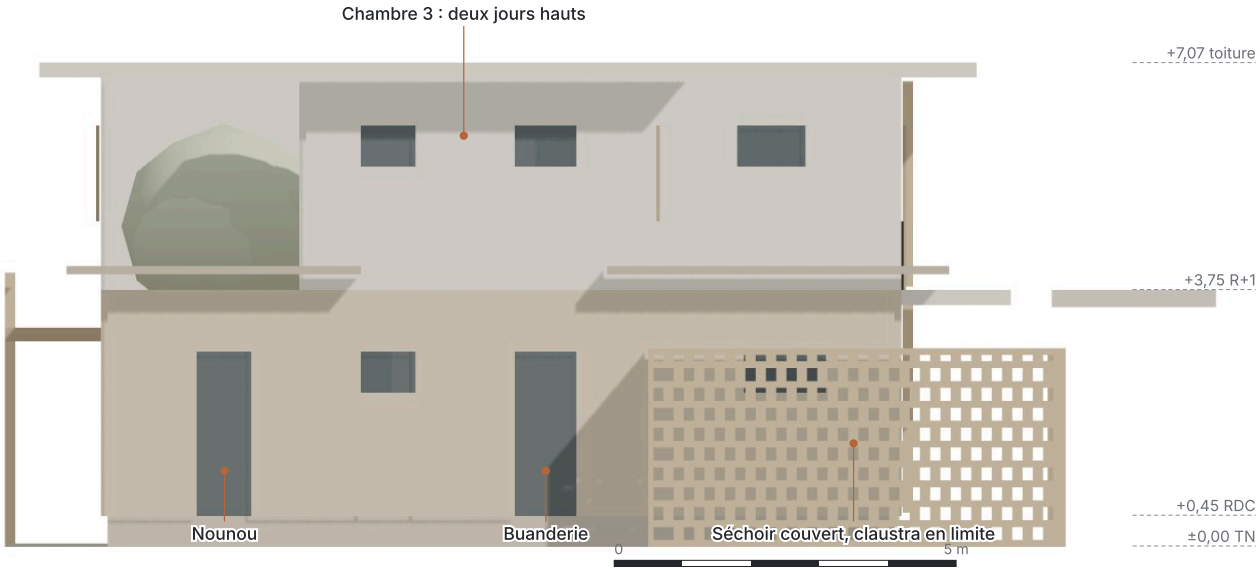

Au Sud, le jardin arrière et le locatif à 5,5 m : la claustra haute de la pergola coupe les vues du locatif vers le patio. À l'Est, la limite séparative est à 1,50 m : seulement des jours hauts (allège à 1,80 m), pour respecter les distances de vues droites, et un claustra en limite au séchoir.


Élévations tirées de la maquette 3D du modèle (ouvertures listées dans `facade.py`), clôtures, guérite et arbres masqués ; lumière conventionnelle à 45°.

Alignements. Axes verticaux communs au rez-de-chaussée et à l'étage (claustra d'escalier, baies, jours) ; linteaux à 2,40 m partout ; allèges à 1,00 m pour les fenêtres, 1,80 m pour les jours hauts, 0 pour les baies.

OPTION C · FAÇADES

L’angle des deux rues et le patio


Perspectives à deux points de fuite (axe de visée horizontal, cadrage par décentrement) : les verticales restent verticales.

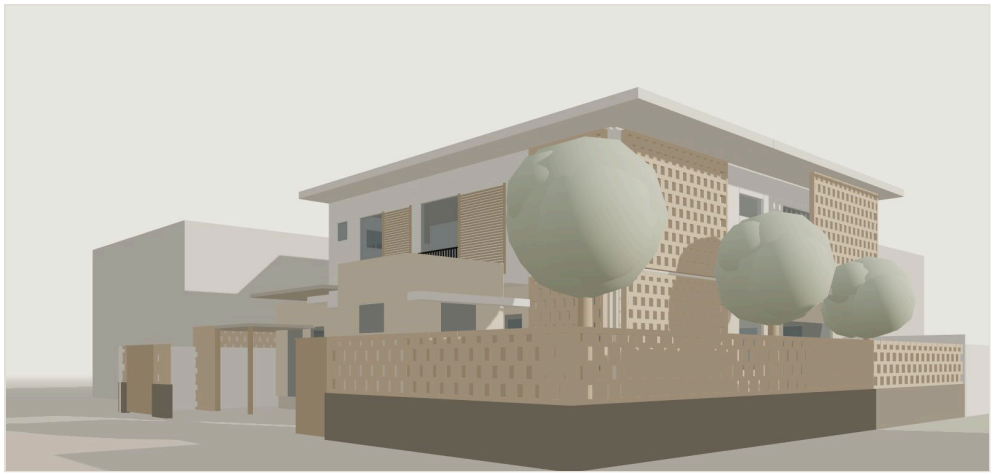

Depuis le carrefour au Nord-Ouest, 16 h 30. La clôture (socle de 1,0 m et claustra en BTC jusqu’à 2,2 m) laisse passer l’air ; au-dessus, la toiture-ombrière, la lanterne d’escalier et la double peau de la suite.



Axonométrie depuis le Nord-Ouest : la dalle de toiture unique, la casquette et le porche au Nord, l’aile de service basse à l’Est, le patio ouvert au cœur.

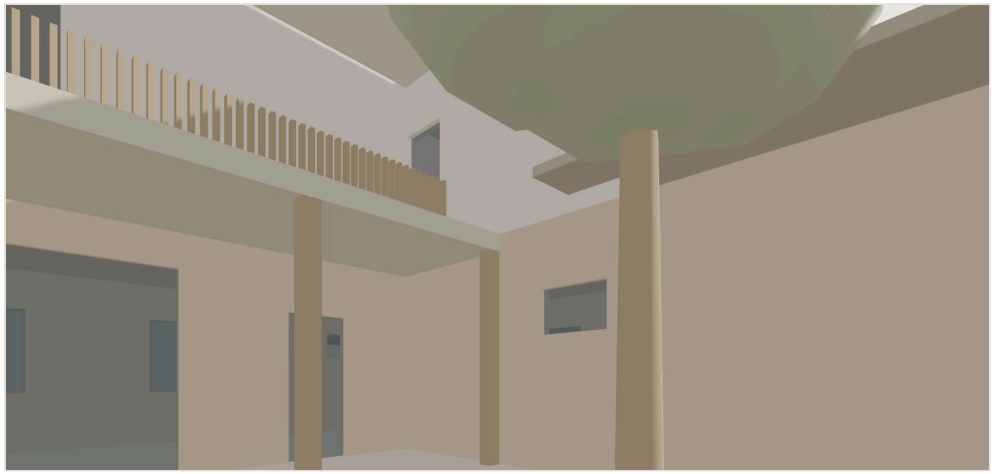

Le patio depuis le jardin Sud, 8 h 30 en novembre : terrasse couverte, poteaux bois, passerelle à lames de l’étage.



Rendu d’ambiance généré par IA (Sume) à partir de la maquette du patio, avant la reprise des façades sur rue ; les façades du patio n’ont pas changé. Image indicative : matières et végétation interprétées.