
01 / Une cour pour douze cles

Variante C recomposee en R+1 - toutes les cotes sont en metres

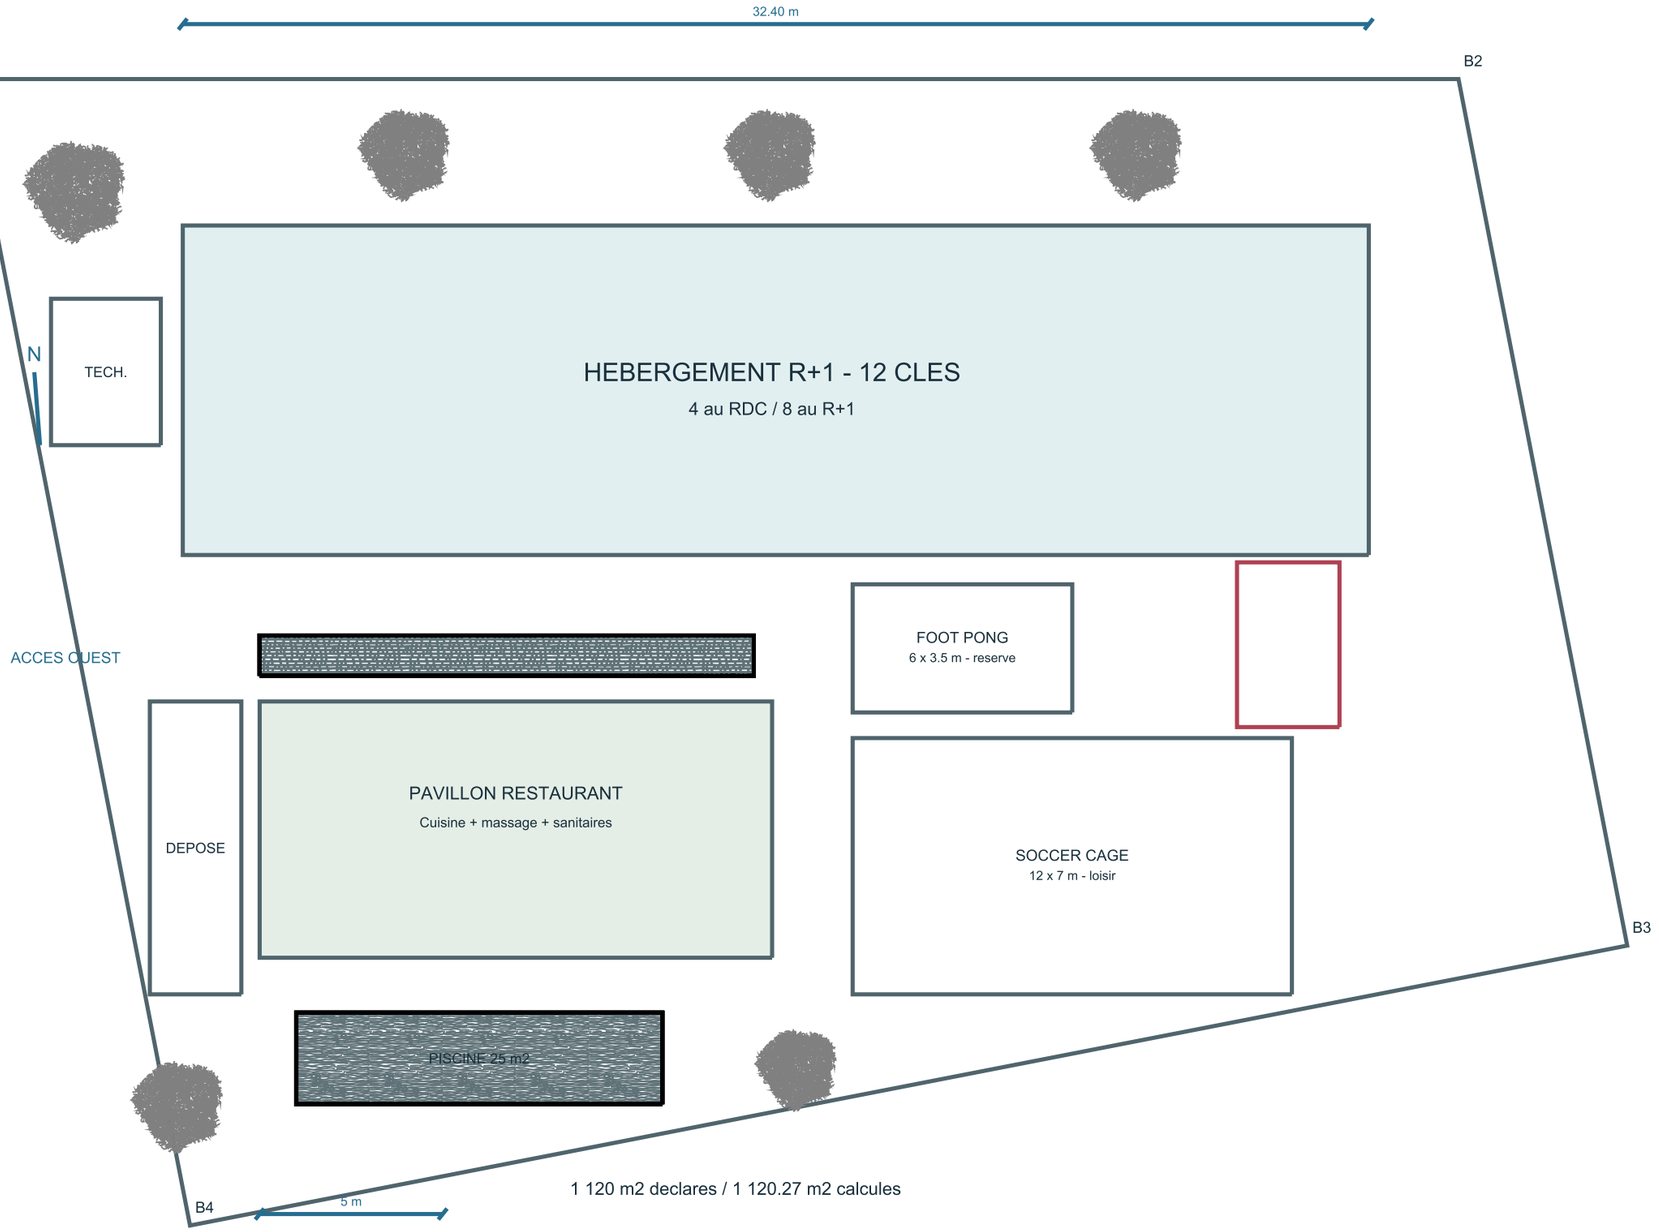

LECTURE DU PLAN

Terrain source du depot : lot 2511, ilot 225. Coordonnees reprises sans deformation.

Hotel : 32.40 x 9.00 m. Pavillon : 14.00 x 7.00 m.

Soccer cage de loisir : 84 m2. Format compact, non terrain de competition.

Foot pong : emprise de 21 m2. Degagements a confirmer selon equipement.

Depose et livraison uniquement. Stationnement client reste a resoudre.

Reculs proposes, non reglementaires. Extension R+3 conditionnee au droit a construire.

02 / Rez-de-chaussee

Variante C recomposee en R+1 - toutes les cotes sont en metres



LECTURE DU PLAN

CH01 a CH04 : 4 cles. Chaque unite : 22.69 m2 nets, salle d eau de 4.40 m2 incluse.

ACC : accueil / lounge, 23.12 m2. SPORT : 23.12 m2. REUN : 23.12 m2.

BOH : lingerie / office / personnel, 23.12 m2. Organisation a detailler.


REST : 52.80 m2, cible 28 couverts. CUIS : 8.61 m2. RES : 8.61 m2.

MASS : 8.48 m2. WC : 8.48 m2.

Rouge : reperes neutres pour blocs manquants. Portes, arbres et eau : blocs Archibooks.

03 / Premier etage

Variante C recomposee en R+1 - toutes les cotes sont en metres

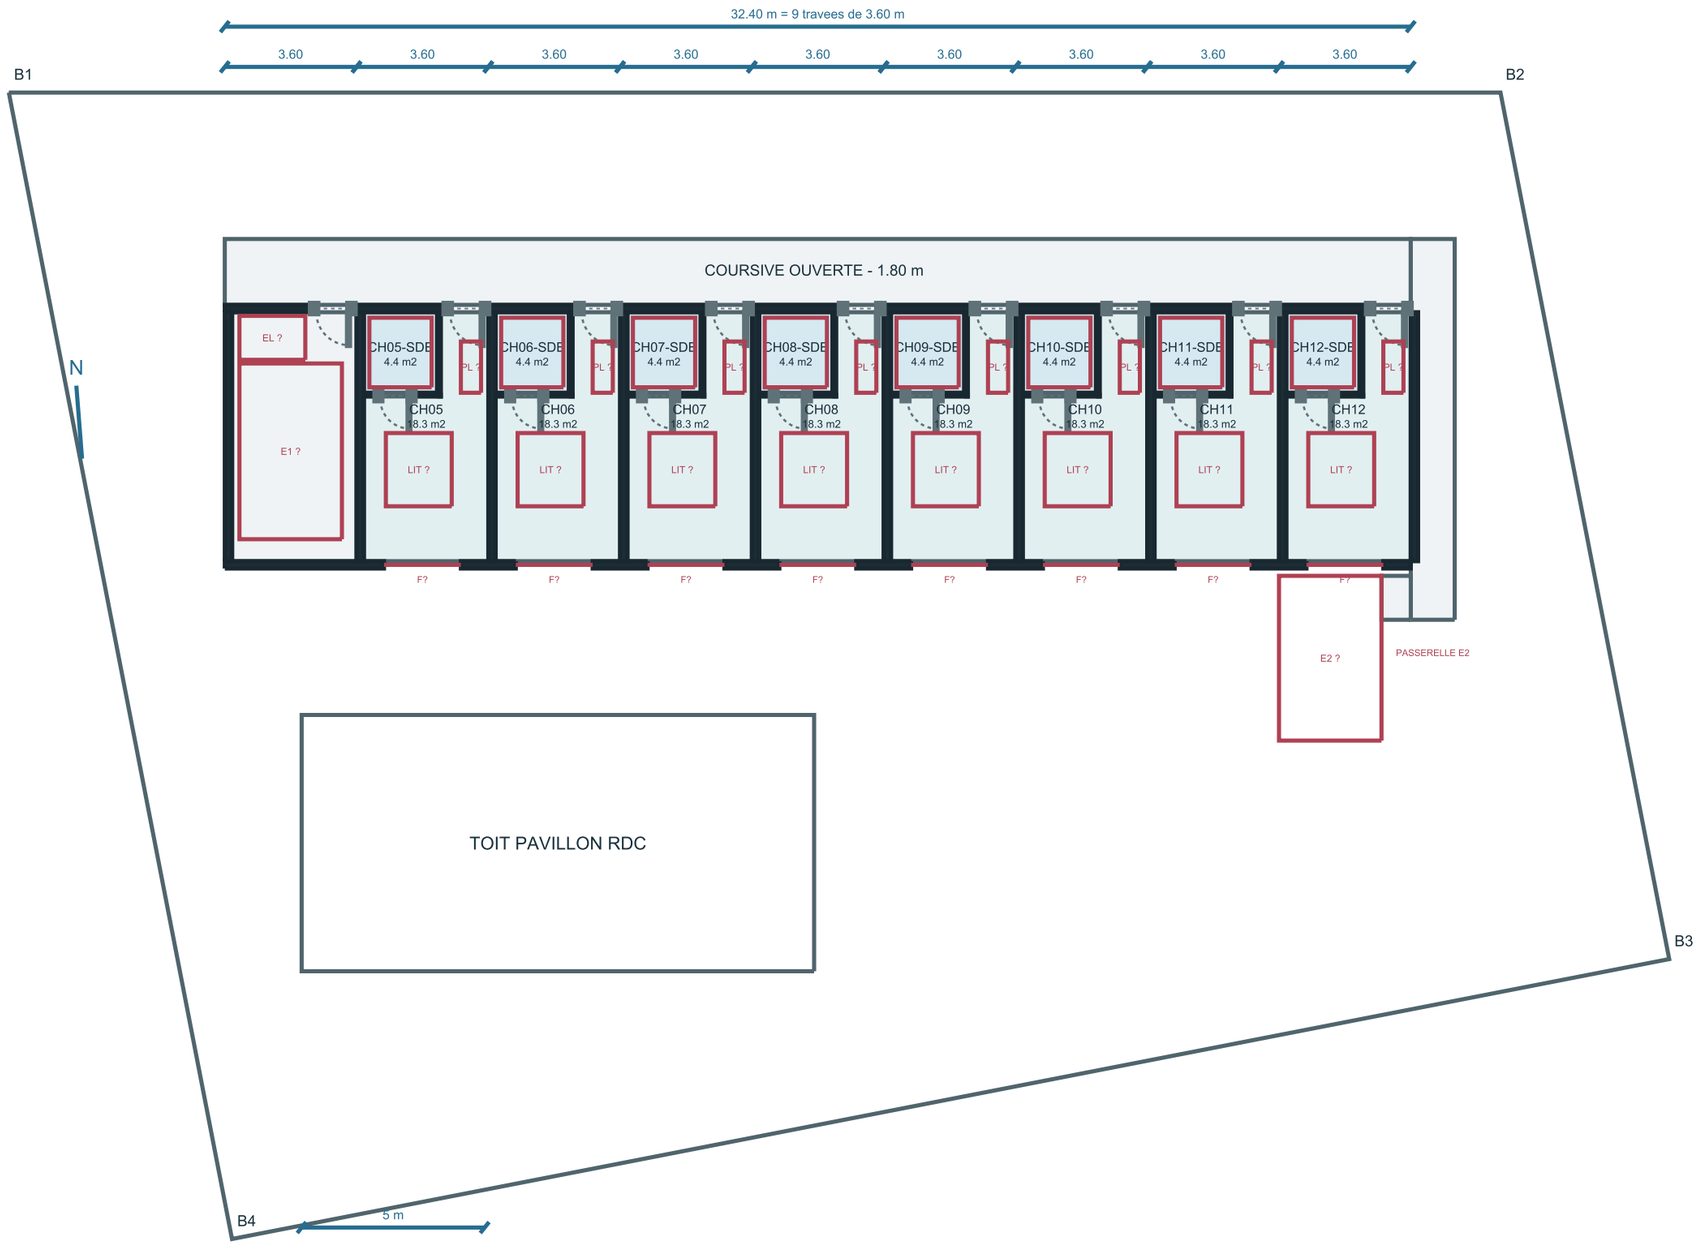

LECTURE DU PLAN

CH05 a CH12 : 8 cles de 22.69 m2 nets chacune.

Coursive : 1.80 m de large. Passerelle est vers E2 : 1.20 m.

E1 et E2 : emprises reservees. Les escaliers droits ne sont pas dessines : bloc absent.


EL : reserve indicative, dimensions et accessibilite a reprendre avec le fournisseur.

F? : baie de fenetre, sans bloc correspondant. LIT?, PL?, SAN? : reperes identifies.

Le nombre de sorties, les paliers et le desenfumage doivent etre valides en APS.

04 / Coupe et evolution

Variante C recomposee en R+1 - toutes les cotes sont en metres

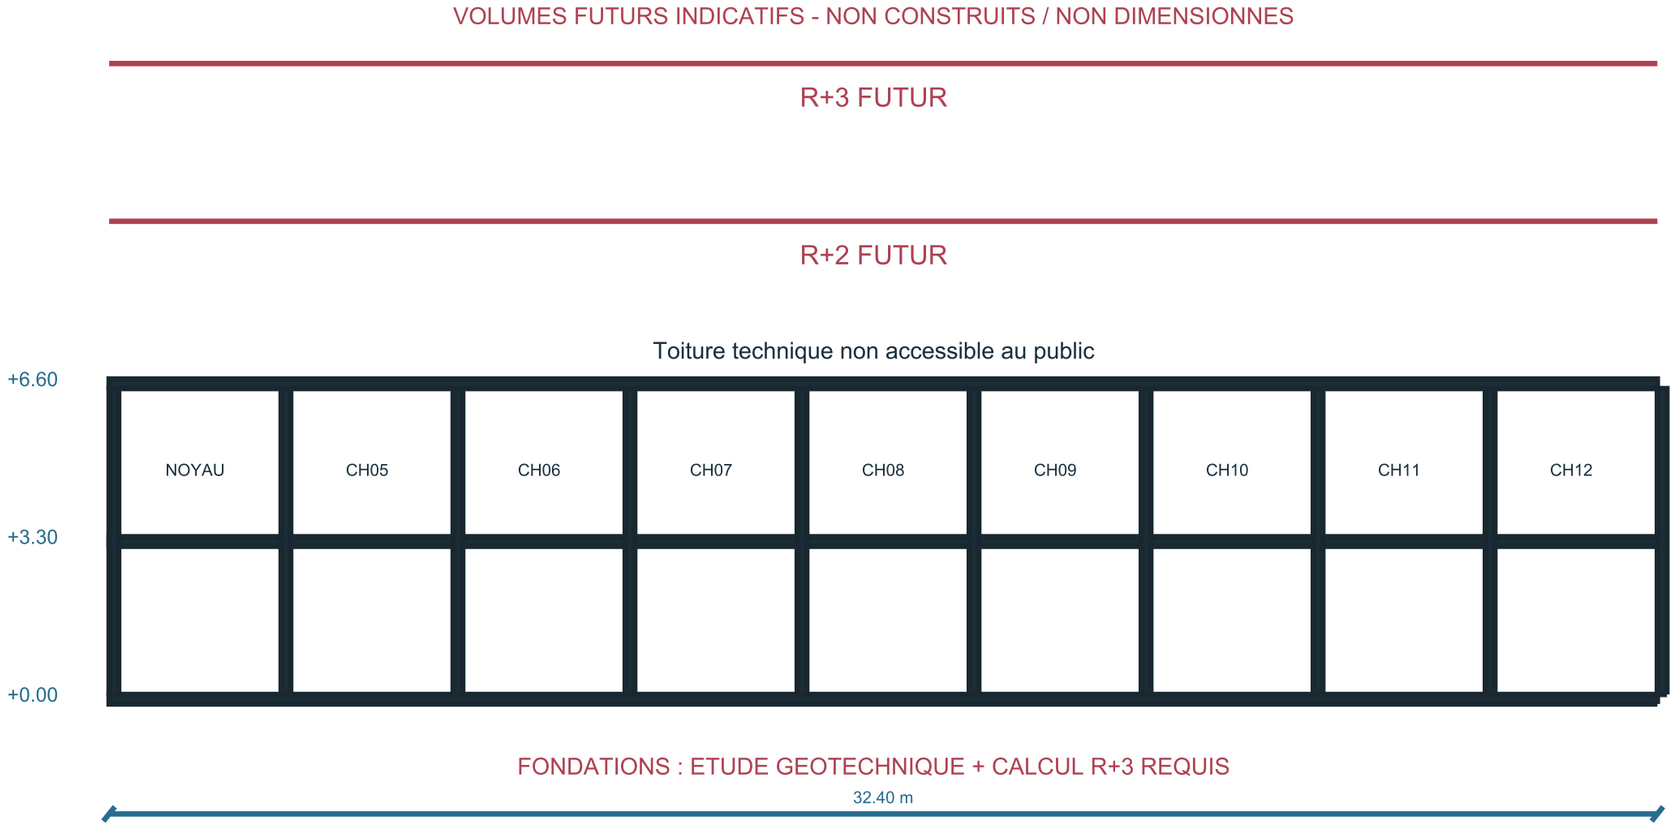

LECTURE DU PLAN

RDC : +0.00. R+1 : +3.30. Toiture : +6.60.

R+2 / R+3 : volumes de principe uniquement, exclus du modele construit.

Trame repetee de 3.60 m ; gaines sanitaires superposees.

Poteaux de 30 x 30 cm : gabarits indicatifs, pas des sections calculees.

Fondations : zones reservees dans IFC, pas de semelles dimensionnees.

Etude sol, charges futures, vent, stabilite, corrosion littorale et fondations a traiter par le BET.

05 / Surfaces et arbitrages

12 unites retenues - le standing reste un objectif qualitatif a confirmer

Terrain declare	1 120.00 m2
Emprise hotel	291.60 m2
Pavillon RDC	98.00 m2
Enveloppes de planchers (2 hotel + pavillon)	681.20 m2
Passerelle et palier E2 supplementaires	13.44 m2
Hebergement net (12 x 22.69)	272.28 m2
Restaurant net / cible de capacite	52.80 m2 / 28 couverts
Massage compact net	8.48 m2
Piscine / soccer cage / foot pong	25 / 84 / 21 m2

La superette et le spa complet sont supprimes.

Les 15 cles ne sont pas retenues : elles augmenteraient les surfaces ou reduiraient les chambres.

Pas de suite premium ni de loggia privative dans cette variante compacte : standing a valider avec le client.

Accessibilite, stationnement, vestiaires du personnel et traitement acoustique restent a developper.

Les surfaces de plancher ci-dessus sont des enveloppes geometriques, pas des surfaces reglementaires.

06 / Enveloppe financiere

Objectif de 250 a 300 M F CFA, honoraires compris - faisabilite non acquise

ALLOCATION CIBLE AU PLAFOND DE 300 M

Batiment R+1 + pavillon, lots techniques et finitions	171 M F CFA
Provision adaptation structure / fondations au R+3	18 M F CFA
Piscine + soccer cage + foot pong	16 M F CFA
VRD, assainissement, eau, energie, cloture, jardin	24 M F CFA
Equipements cuisine et mobilier hotelier	24 M F CFA
Honoraires et etudes	22 M F CFA
Aleas et ajustements	25 M F CFA

TOTAL CIBLE : 300 M F CFA

Ces montants sont des plafonds a consulter, pas des devis ni un estimatif valide. Ils ne certifient pas le maintien du standing.

Enveloppe tous debours recherchee : fiscalite, assurances, raccordements et inclusions fournisseurs a preciser par Mr Adicko. Foncier non compte ; R+2/R+3 futurs exclus.

Alerte : le seul ratio historique du depot (477 279 F CFA/m2, deja divise par deux) applique aux 681.20 m2 donne environ 325 M F CFA avant plusieurs autres postes. Comparaison indicative : le ratio historique porte sur la SU, non sur cette enveloppe brute.

Il faut donc un chiffrage metrique et des offres locales avant de conclure a la compatibilite avec 300 M. Le seuil de 250 M n est pas demontre.

Sources : brief du 31.10.2026 ; ancienne option C du depot ; regles_agents et design_patterns de Supabase capitude ; blocs DWG Archibooks convertis en DXF avec AutoCAD 2023.