
01 / Implantation et programme

Terrain intégralement affecté au projet : 1 120 m². R+1 et 12 unités.

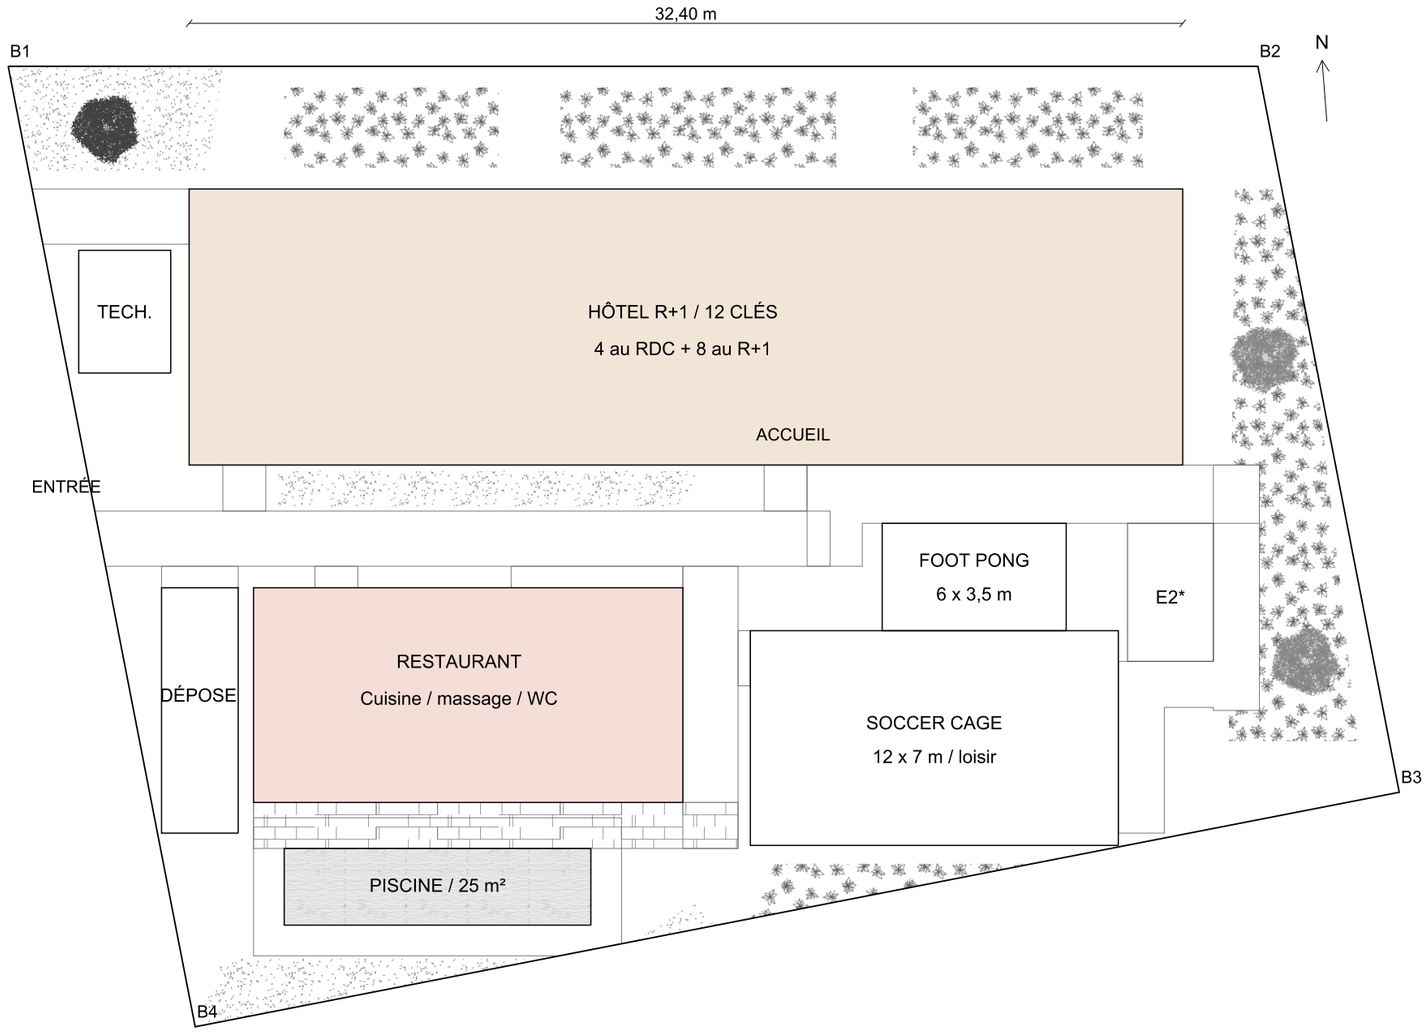

1 120 m² déclarés / 1 120,27 m² calculés

Nord calculé depuis les coordonnées du dépôt.

UN HÔTEL COMPACT

Une barre R+1 de 32,40 x 9,00 m et un pavillon de 14,00 x 7,00 m.

PROGRAMME CONSERVÉ

Piscine, restaurant, sport, réunion, soccer cage et foot pong. Massage compact. Supérette et spa complet supprimés.

SEUILS CLARIFIÉS

Accueil ouvert sur le jardin ; sortie E1 au sud ; foot pong décalé pour dégager l·arrivée.

PRÉPARER LE R+3


Volumes futurs exclus de la phase construite. Structure et fondations à calculer pour les charges futures.

ÉTAT DE L·ÉTUDE

Accès ouest repris du dossier source. Reculs, dépose, stationnement, sécurité et accessibilité à confirmer.

02 / Rez-de-chaussée - hôtel

Aplats pastel par usage. Surfaces nettes ; cotes en mètres.

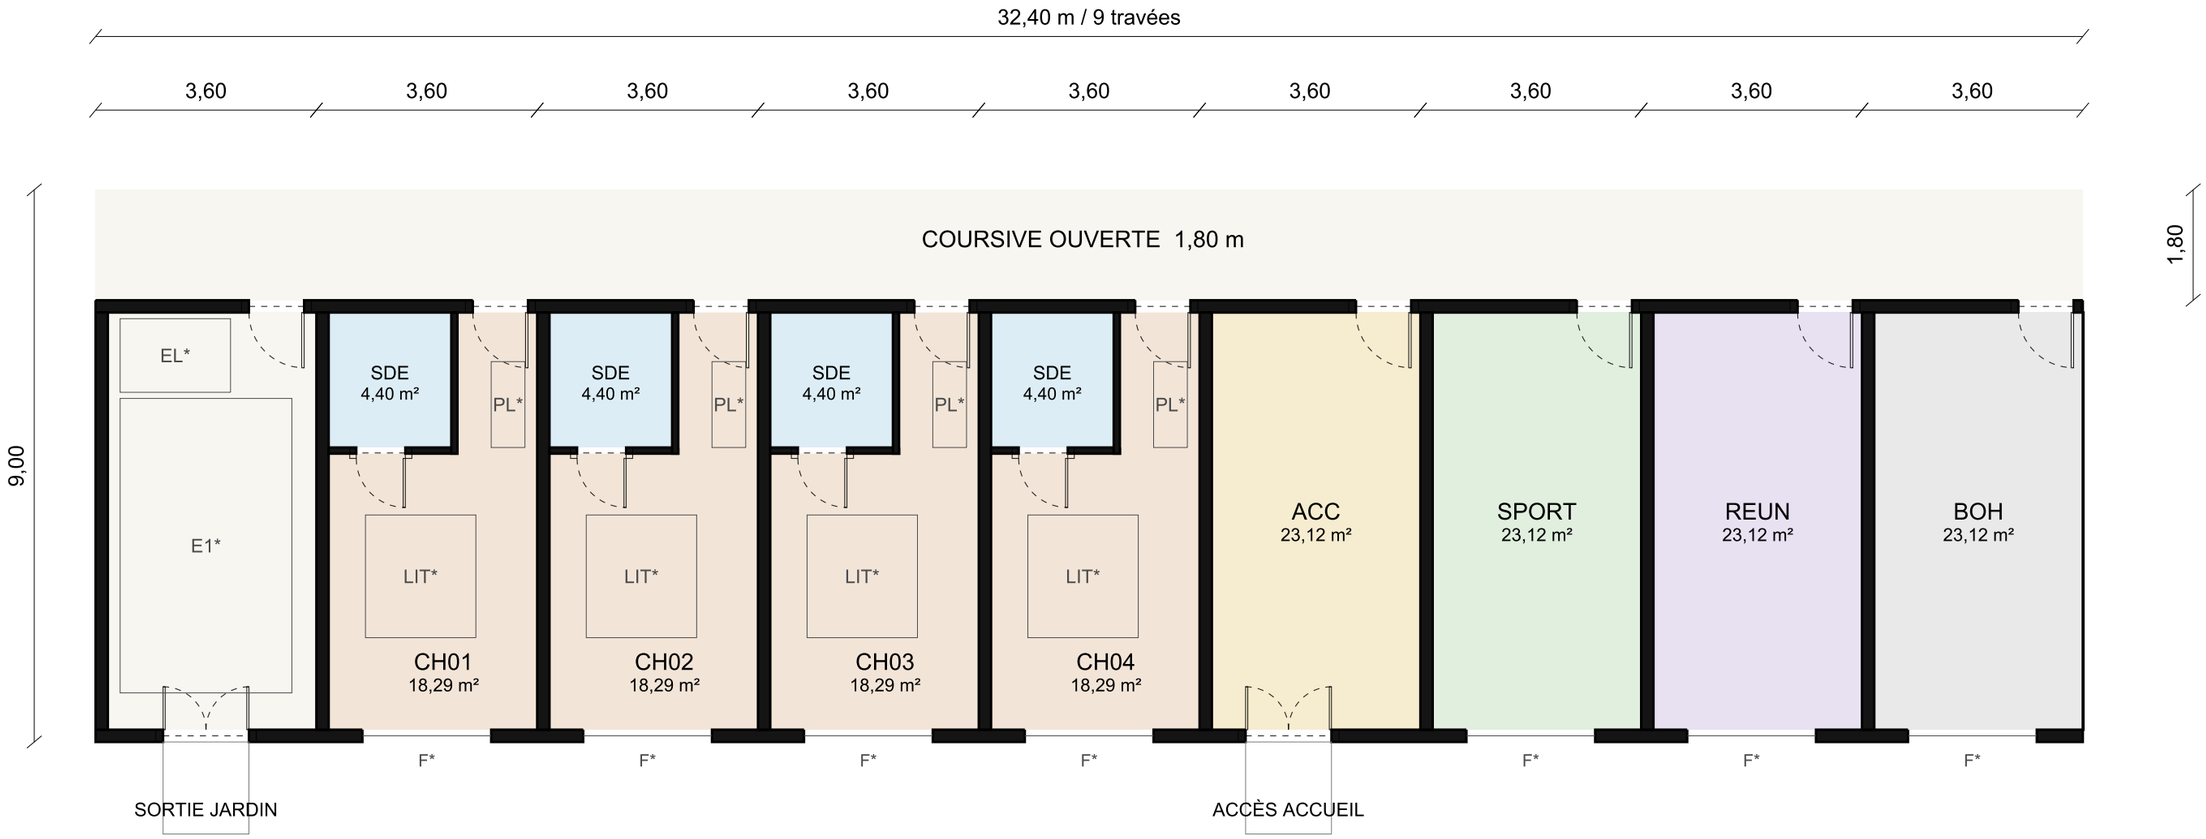

4 chambres + accueil, sport, réunion et office.


* Réservations : escaliers, élévateur, fenêtres et mobilier à compléter.

E2*

Hébergement
Restauration
Sanitaires
Services
Sport
Massage
Réunion
Circulations
Accueil

03 / Premier étage - hôtel

Aplats pastel par usage. Surfaces nettes ; cotes en mètres.

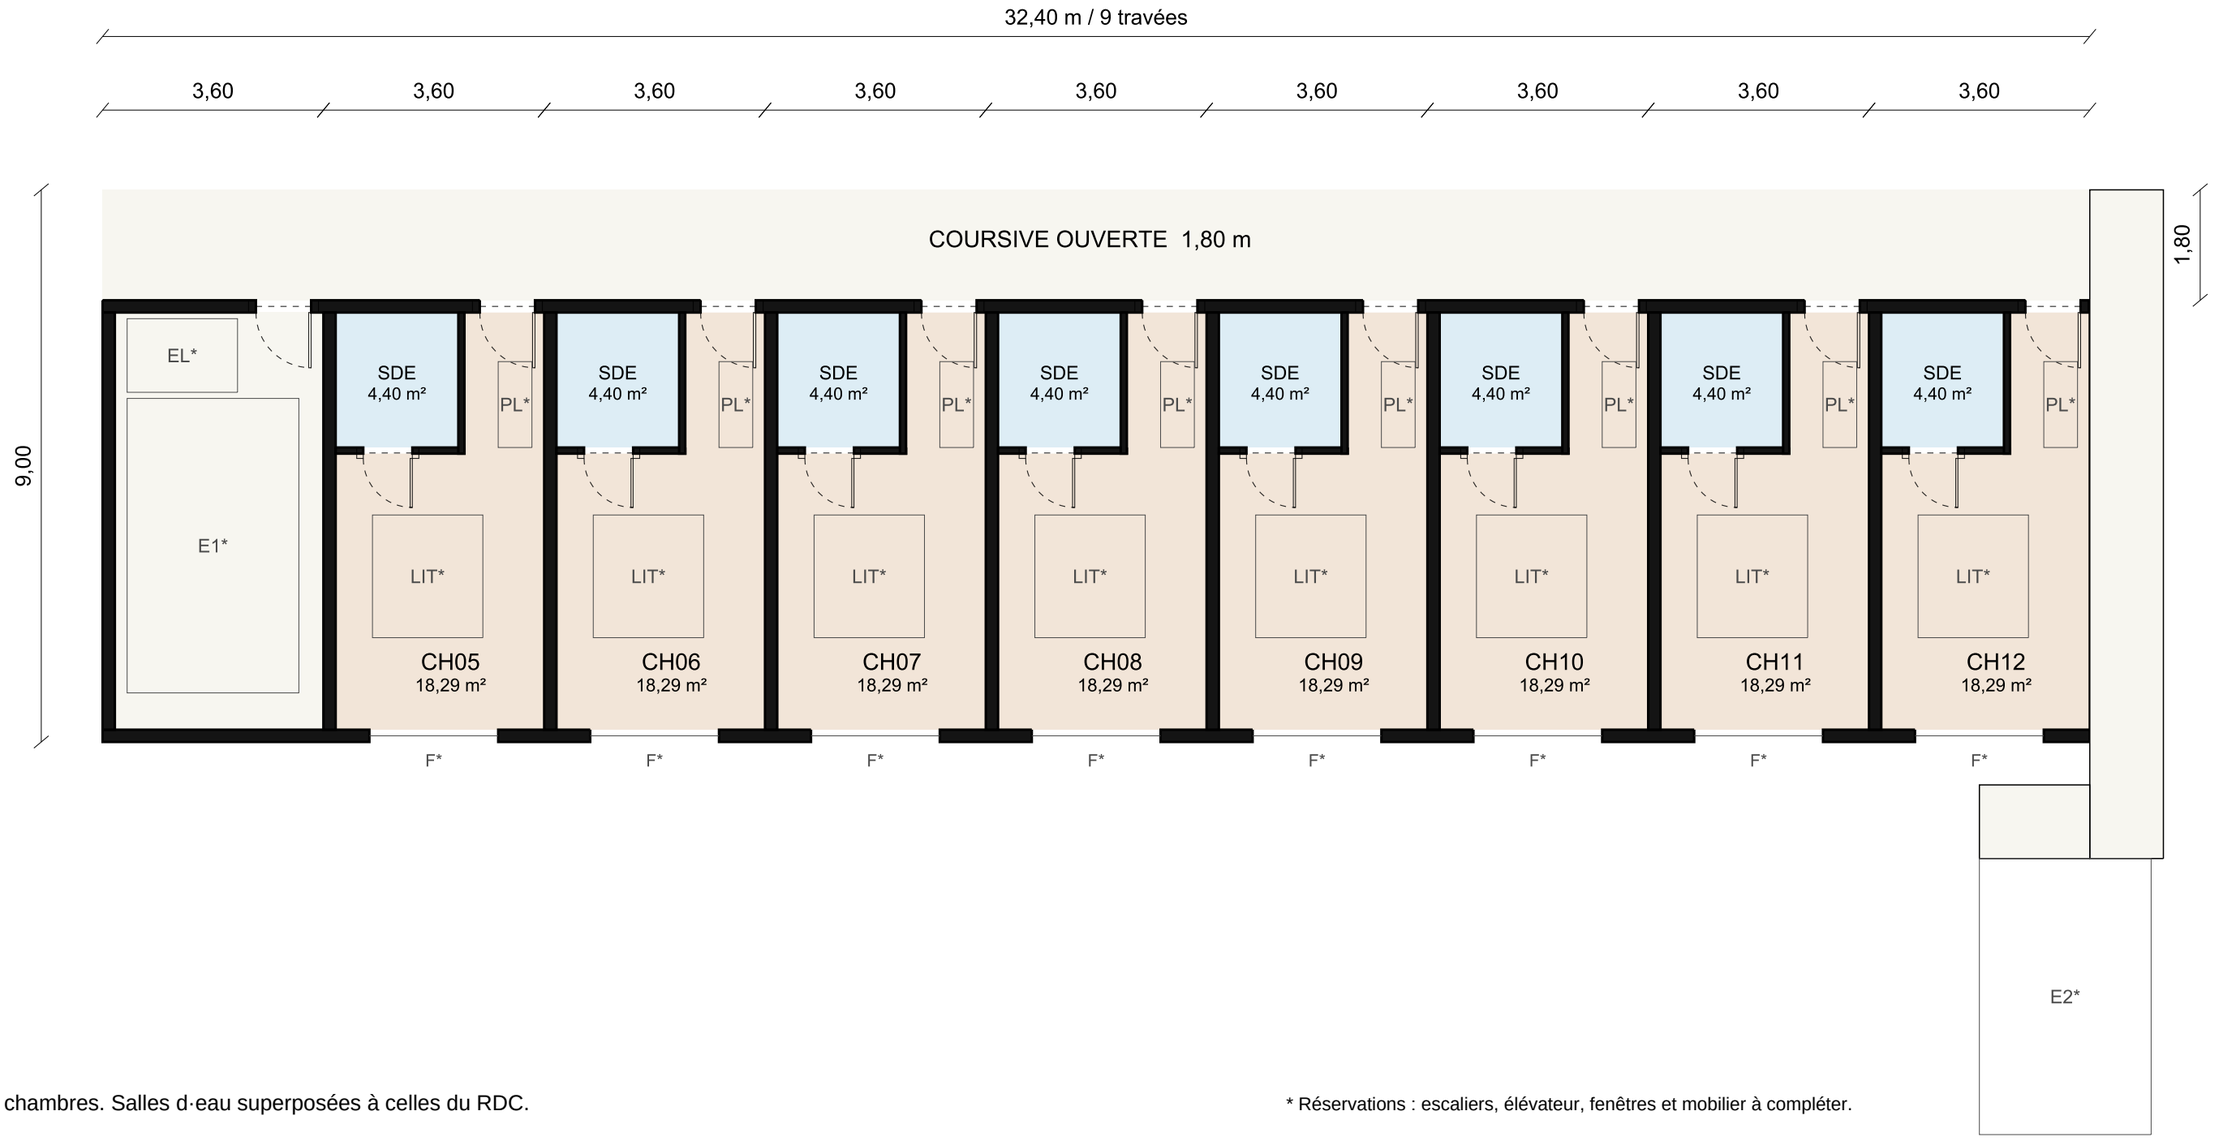


8 chambres. Salles d·eau superposées à celles du RDC.

* Réservations : escaliers, élévateur, fenêtres et mobilier à compléter.


Hébergement
Restauration
Sanitaires
Services
Sport
Massage
Réunion
Circulations
Accueil

04 / Pavillon et chambre type

Restaurant, cuisine, réserve, massage et sanitaires. Chambre de 22,69 m² nets.

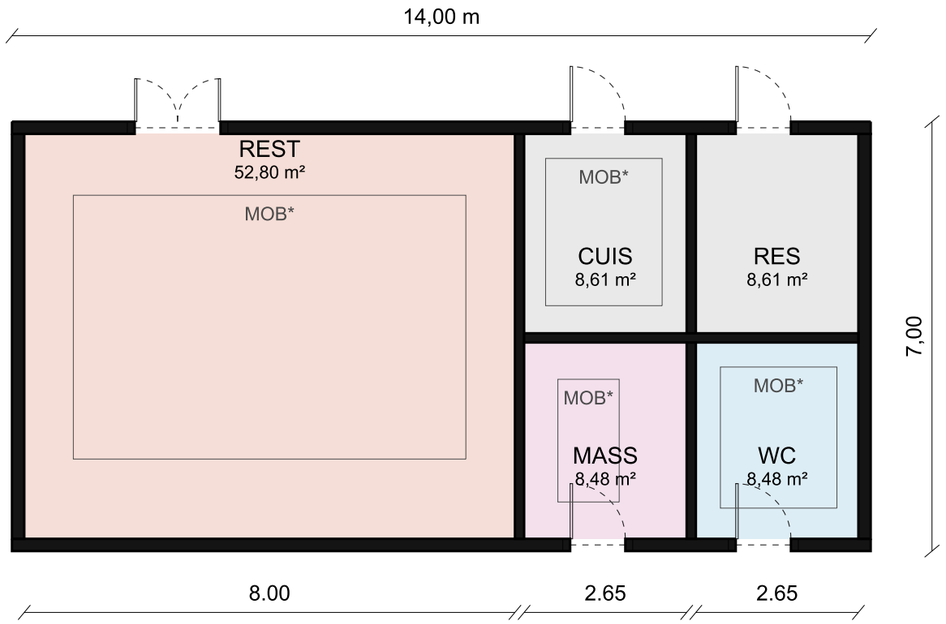


PAVILLON / 1:100

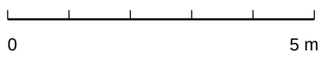

Restaurant : 52,80 m² nets, cible 28 couverts. Cuisine et réserve : 8,61 m² chacune. Massage et WC : 8,48 m² chacun. Implantation du mobilier à développer avec les blocs manquants.


F*, LIT*, PL*, SAN*, MOB* : repères neutres. Aucun équipement absent du catalogue n·est présenté comme une famille validée. Le détail n·est pas une chambre PMR validée.

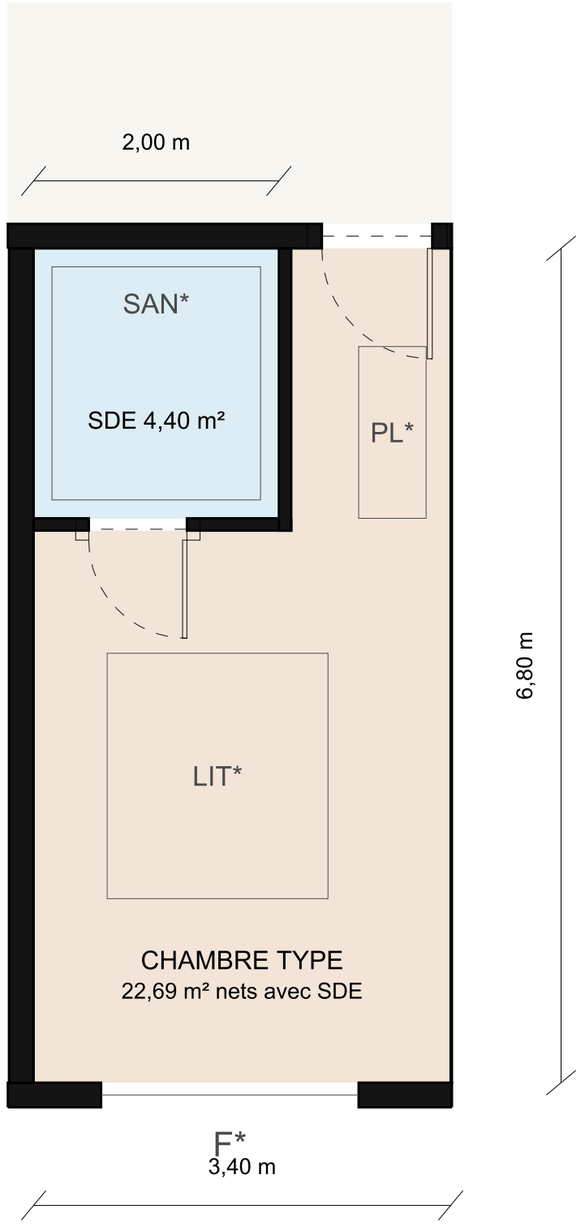

CHAMBRE TYPE / 1:50

05 / Jardin, seuils et parcours

Arrivée, lisières, jardin calme, terrasse, eau et jeux.

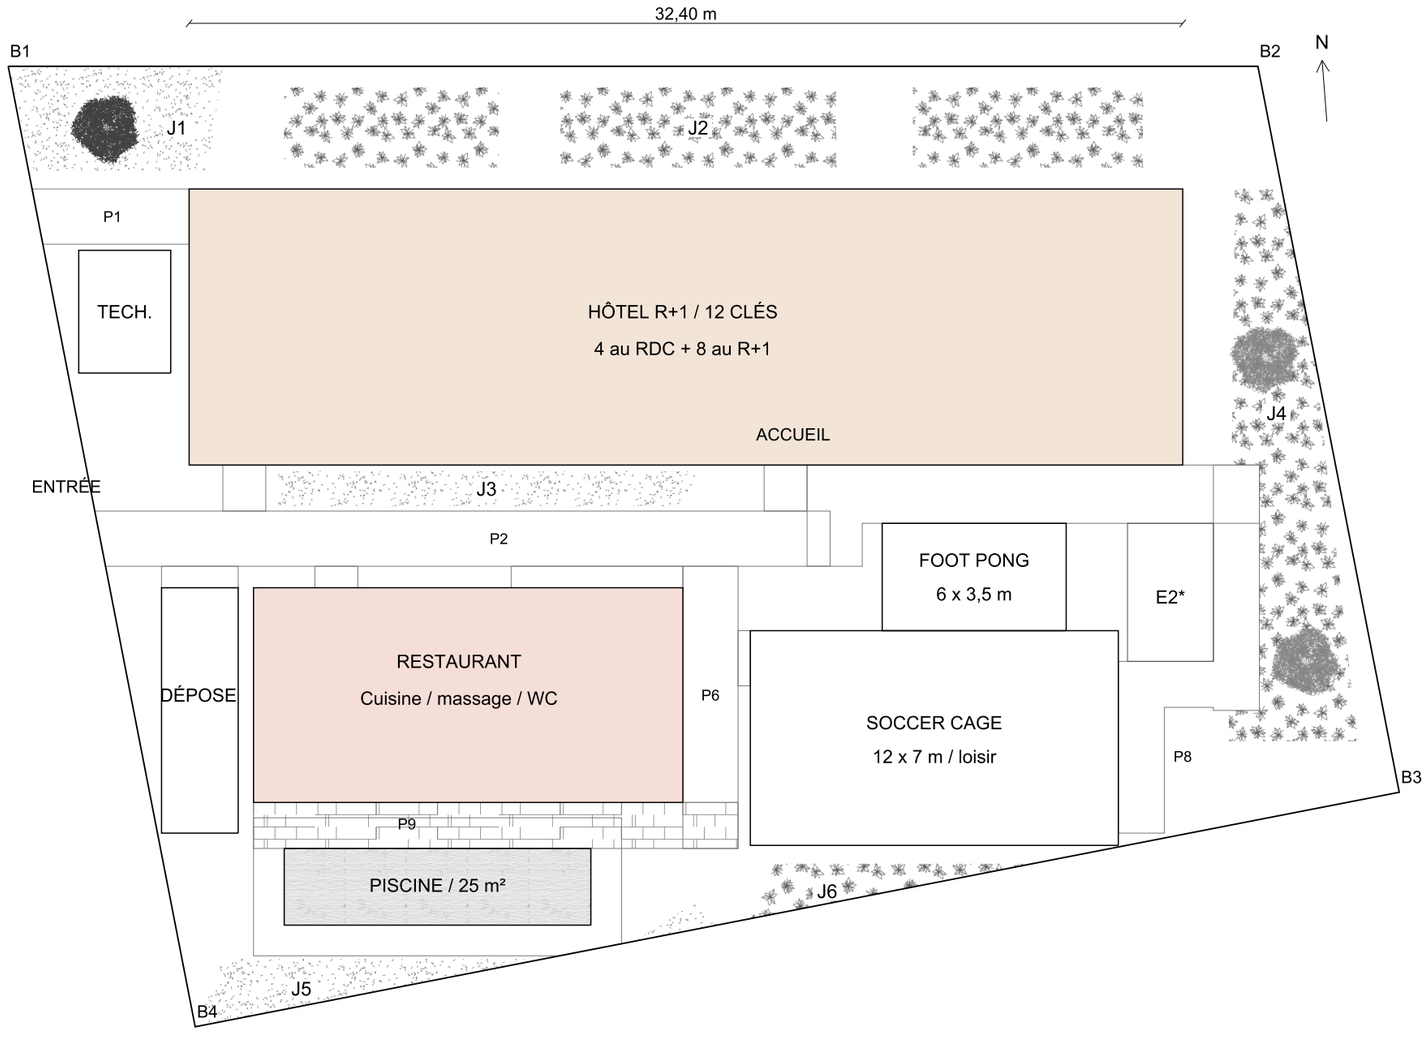

1 120 m² déclarés / 1 120,27 m² calculés

Plantations projetées. Espèces et dimensions adultes à valider.

J1 / SEUIL OUEST

Couvre-sol bas, vues d·entrée dégagées.

J2 / LISIÈRE DE COURSIVE

Massifs bas discontinus ; pas de haie opaque.

J3 / JARDIN ENTRE HÔTEL ET RESTAURANT

Sous-strate basse face aux chambres.

J4 / LISIÈRE EST

Écran discontinu, ventilation et entretien.

J5 / JARDIN DE REPOS AU SUD

Couvre-sol et clairières, surveillance du bassin.

J6 / LISIÈRE DES JEUX

Massif bas, aucune plante épineuse prescrite.

P1 : coursive. P2 : arrivée / accueil. P6 : service. P8 : jeux / sortie E2. P9 : terrasse / bassin.

06 / Coupe de principe et évolution

RDC +0,00 / R+1 +3,30 / toiture +6,60. Deux niveaux futurs à étudier.

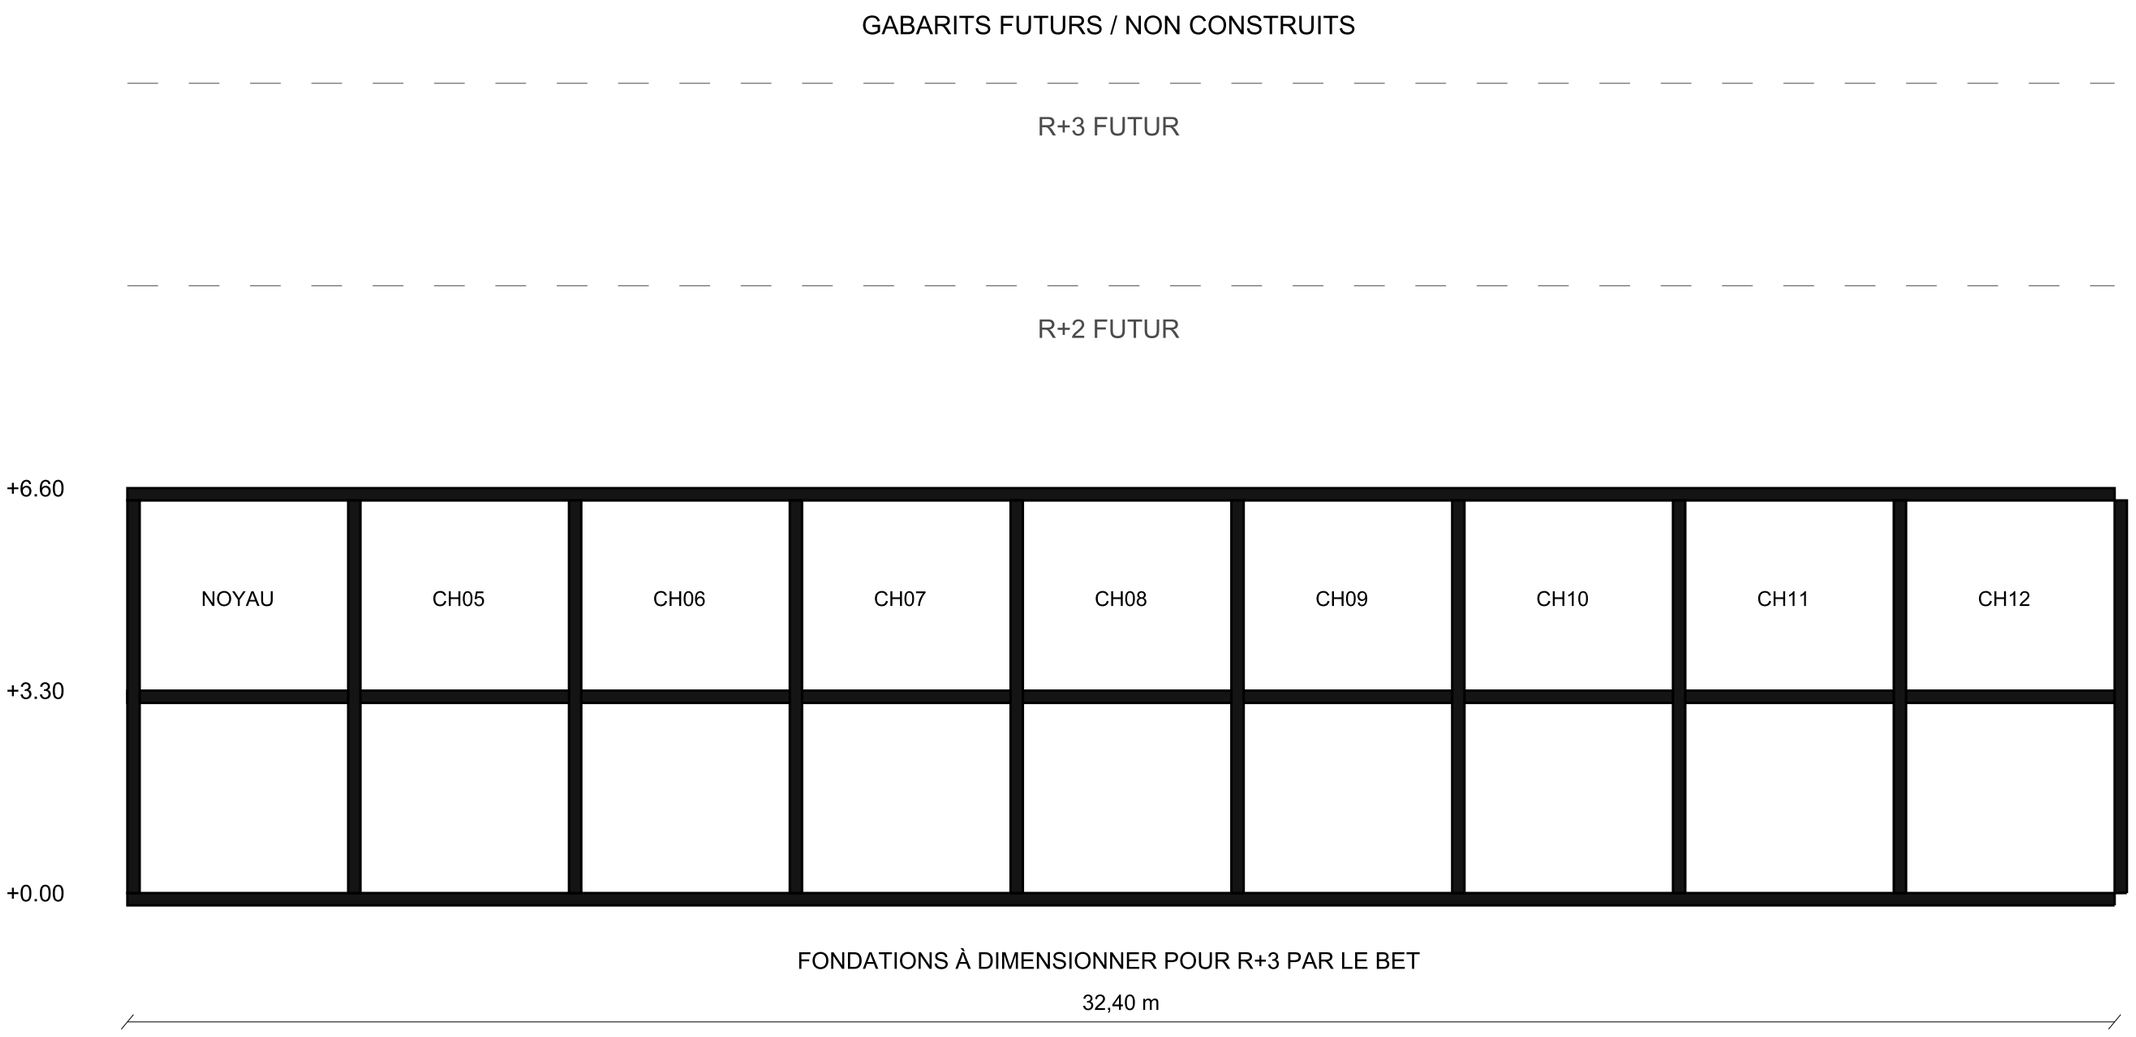


Schéma longitudinal de trame, sans détail d·exécution. R+2 et R+3 sont des gabarits futurs. Fondations, contreventement et sections porteuses restent à dimensionner par le BET après étude de sol.

0 5 m