

Villa à patio et deux maisons duplex

LOT 1728 · RIVIERA PALMERAIE, ABIDJAN · ESQUISSE, OPTION C V5 · 10.11.2026



Vue aérienne (imagerie publique, antérieure) : contour du lot estimé, angle Nord-Ouest de l'îlot



Clôture sur la rue Ouest



Rue Ouest vers le Sud



Le lot vu depuis le voisin Est

PARCELLE


20 × 33 m, 660 m² ; villa sur 360 m² au Nord, locatif sur 300 m² au Sud

RUES


rue Nord (accès villa) et rue Ouest (duplex), en latérite, non revêtues

CONTEXTE

maisons R+1 / R+2 en béton brut ; en face, sur la rue Ouest, maisons de ville à toits rouges

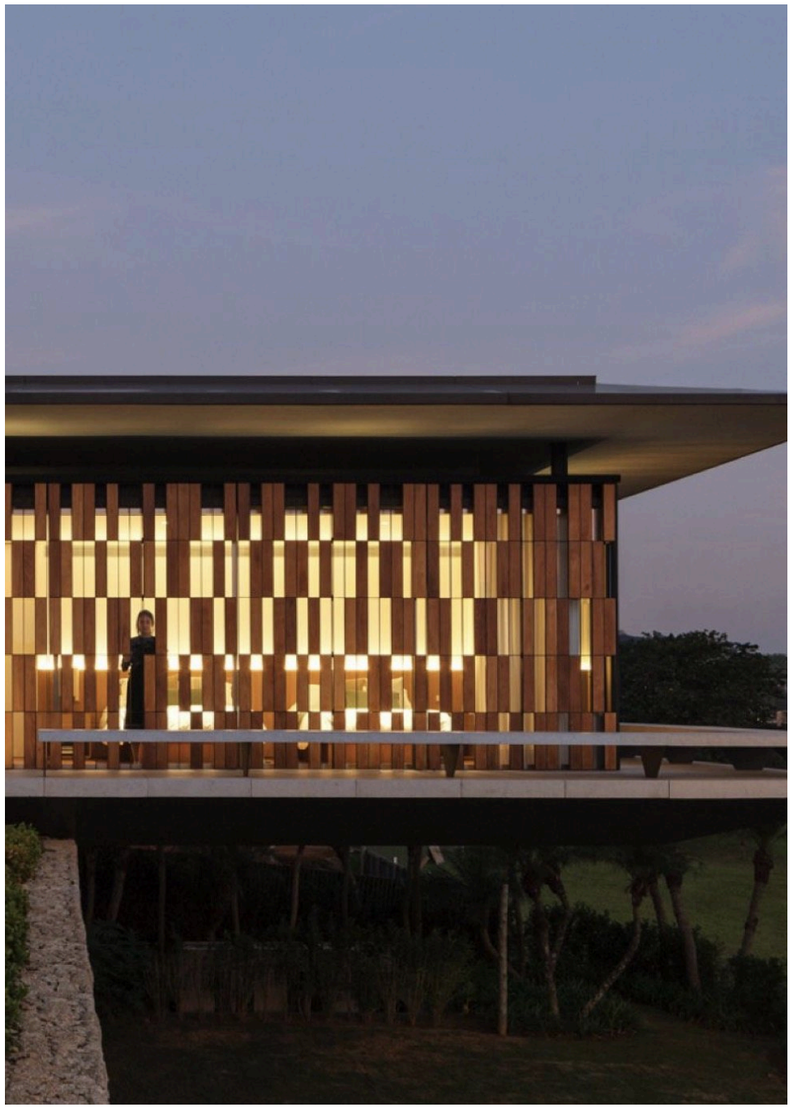

Référence 1 du client : lames de bois en damier, toiture mince

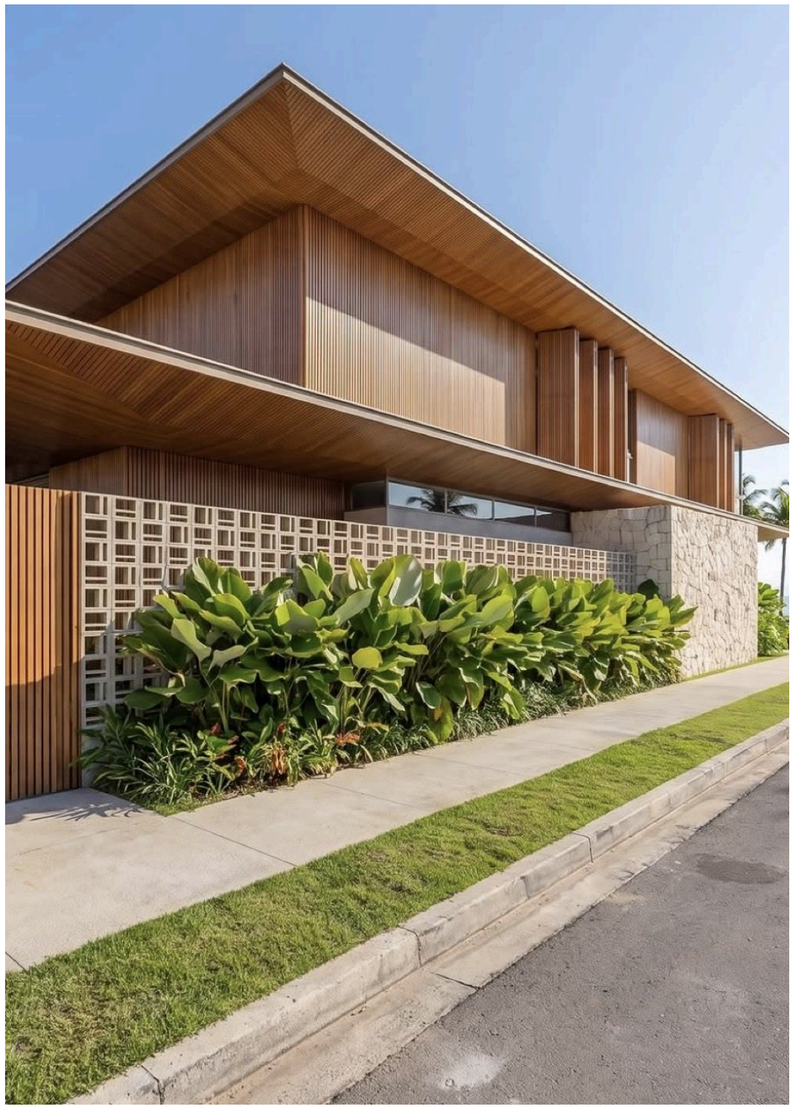

Référence 2 du client : bardage, grands débords, claustra béton

V1

peau de lames en damier, toiture plate mince

V2

bardage et brise-soleil, toit en croupe à sous-face bois

COMMUN

socle en moellons, claustra béton, patio planté (Casa Lineal, Palinda Kannangara)



Vue d’ambiance, variante 1 : villa et duplex sous une même écriture

HORIZONTALES

±0,00, +3,30, +6,60, couverture +9,00 ; linteaux 2,40

VERTICALES


baies de l’étage au droit de celles du RDC, sur les axes

MATIÈRES

socle en moellons, étage dans une même peau bois, poteaux acier noirs

LIMITES

mur végétalisé de 3,50 m entre villa et duplex

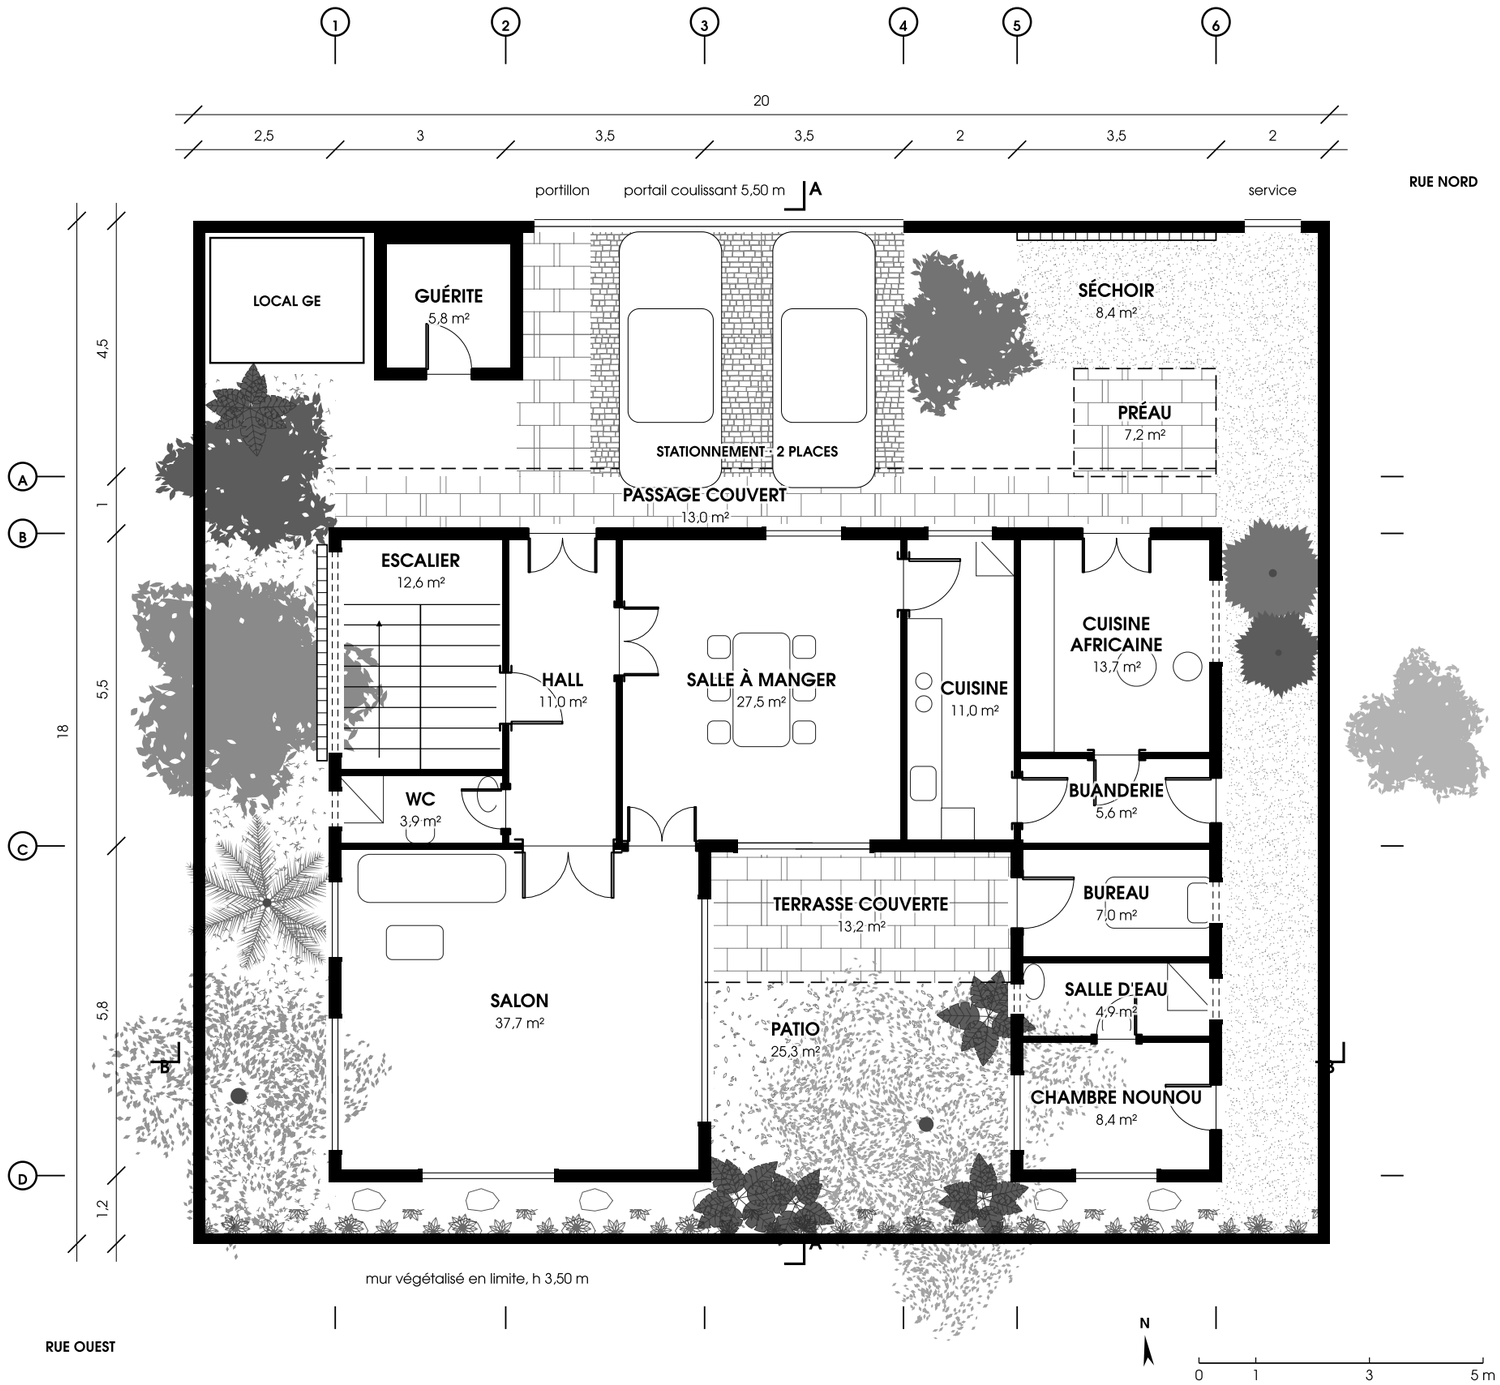

CLOS
149,0 m²

TRAME
2,5 · 3 · 3,5 · 3,5 · 2 · 3,5 · 2 m


MARKUP
cuisine sur l'axe 5, porte vers la terrasse supprimée, 2 places, bassins supprimés

PLAN DU REZ-DE-CHAUSSÉE / échelle graphique, 1:100 env. en A3

CLOS
126,0 m²

PLAN
en L : salon familial et chambres 1, 2 sur la rue, chambre principale au fond

PEAU
lames de bois sur les quatre faces de l'étage

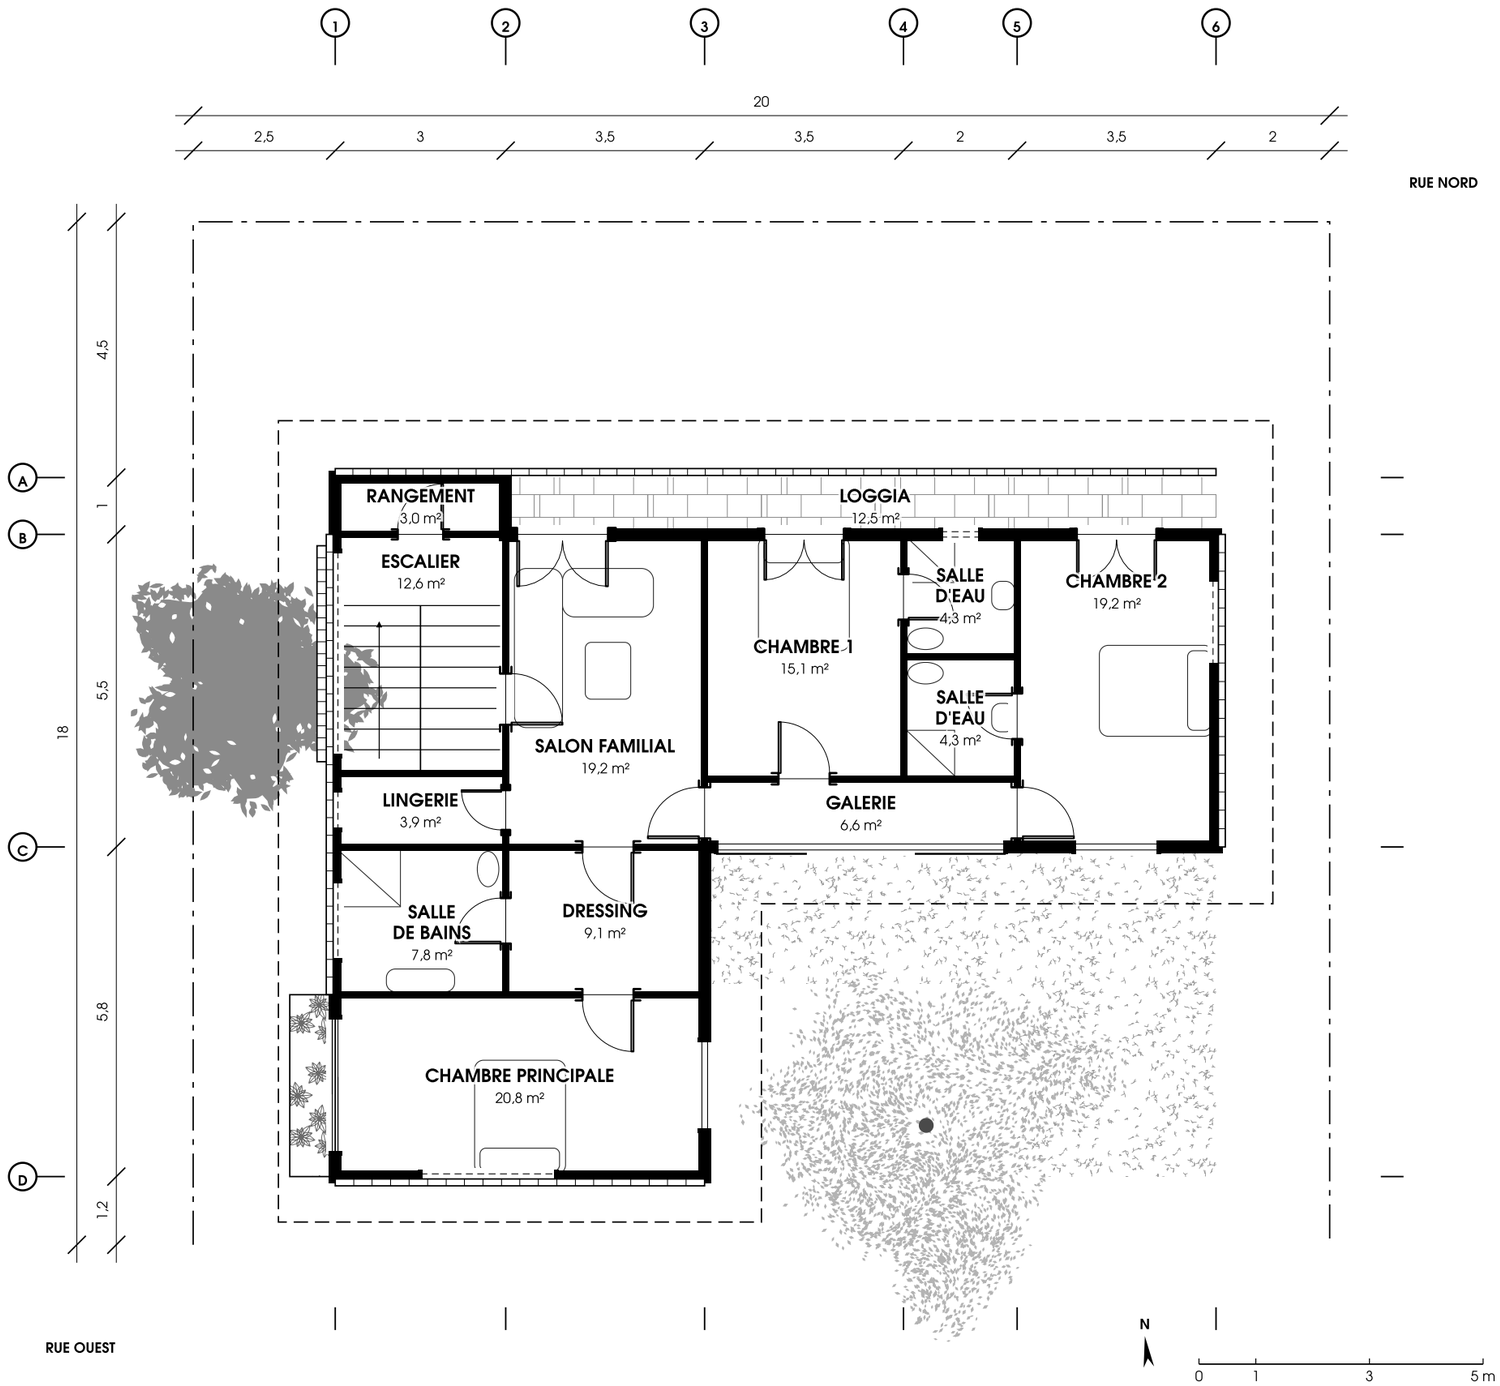

PLAN DE L'ÉTAGE / échelle graphique, 1:100 env. en A3




TOIT-TERRASSE
110,3 m², couvert à +9,00

JARDINIÈRE
plantation basse, sans retombées

TIRETS
rive de la couverture V1

PLAN DU NIVEAU HAUT / échelle graphique, 1:100 env. en A3

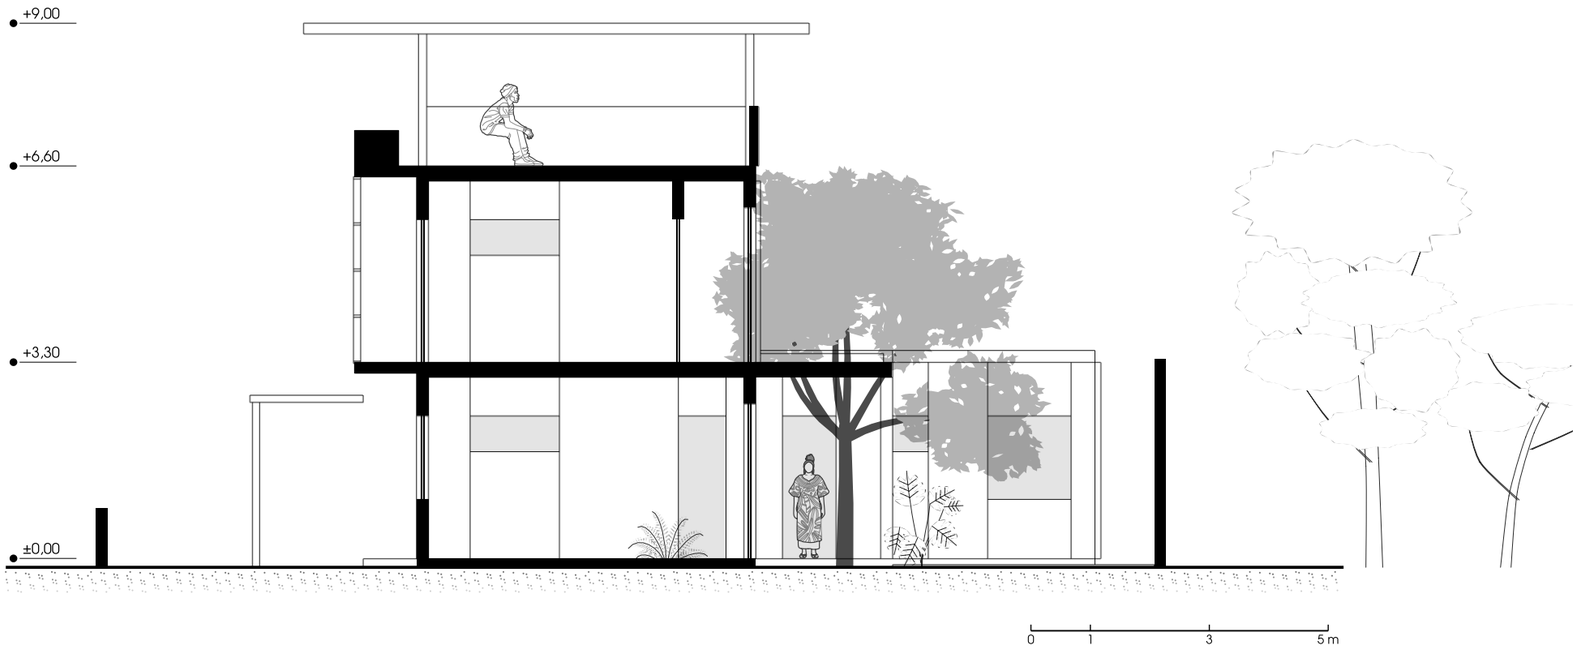


COUPE AA / Nord-Sud, salle à manger, chambre 1, patio, mur végétalisé

NIVEAUX


±0,00 · +3,30 · +6,60 · +9,00 (cotes du client)

BASSINS

supprimés

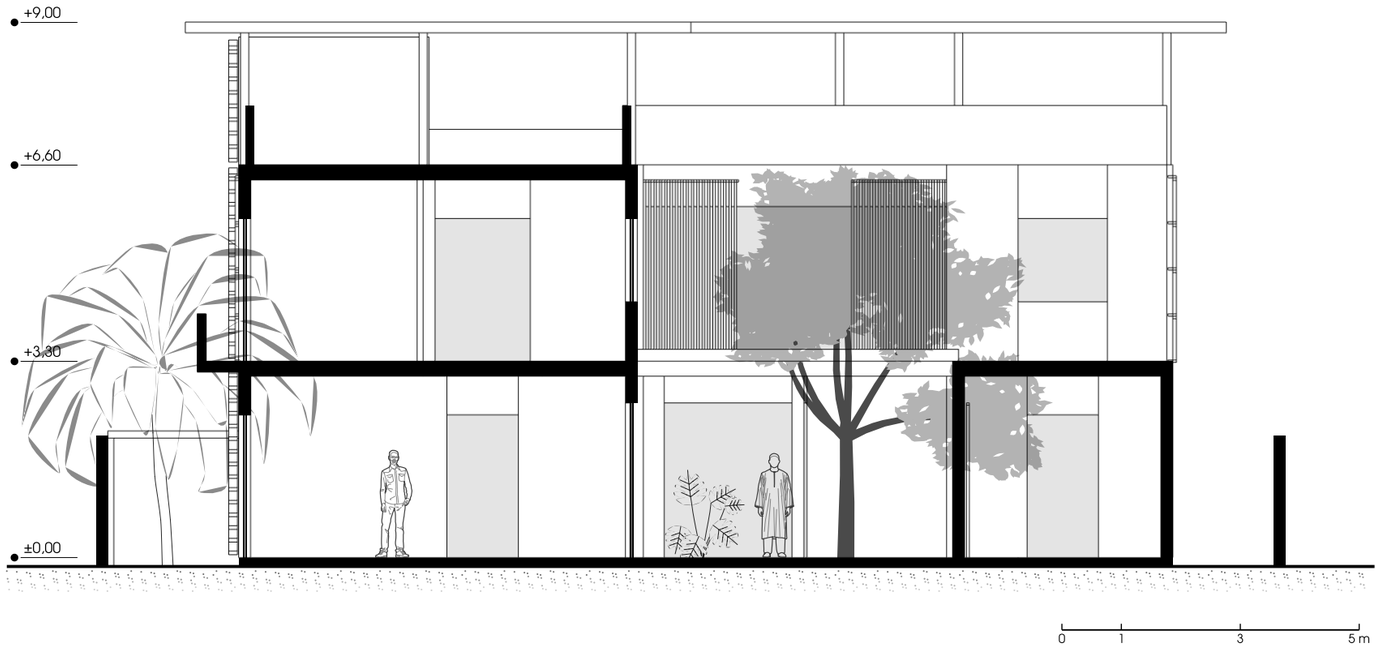

COUPE BB / Est-Ouest, salon, chambre principale, patio, chambre nounou

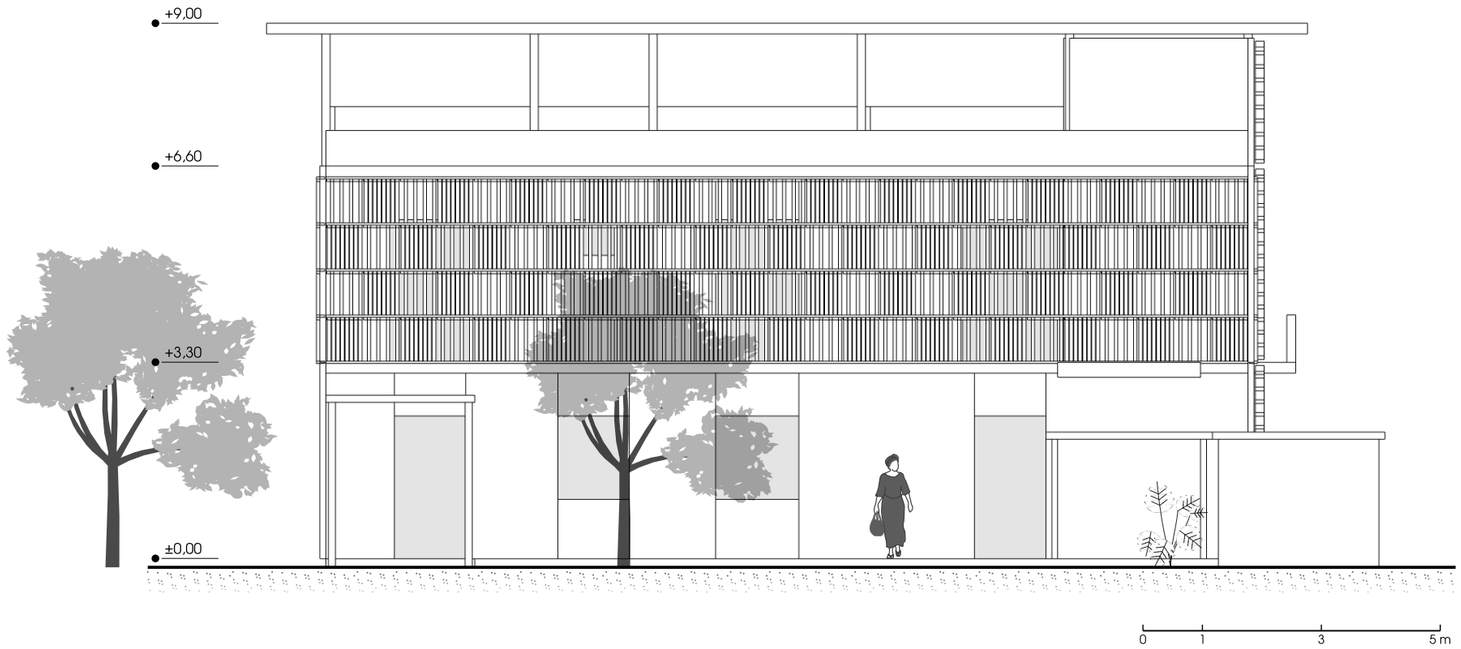

ÉLÉVATION NORD, V1 / lames de bois en damier



ÉLÉVATION NORD, V2 / bardage et brise-soleil

AXES

6,5 · 10,75 · 13,5 · 16,25

GUÉRITE


à la hauteur de la clôture, 2,30 m




ÉLÉVATION OUEST, V1 / sur la rue : villa à gauche, duplex à droite




ÉLÉVATION OUEST, V2 / même trame, même couverture

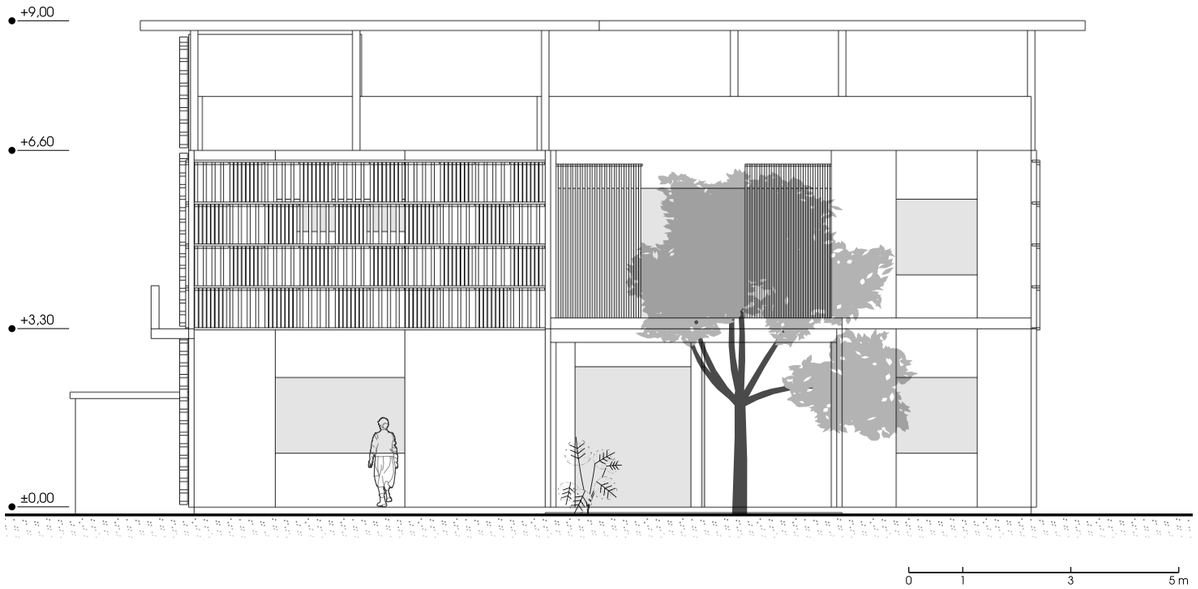


ÉLÉVATION SUD, V1 / sur le mur végétalisé

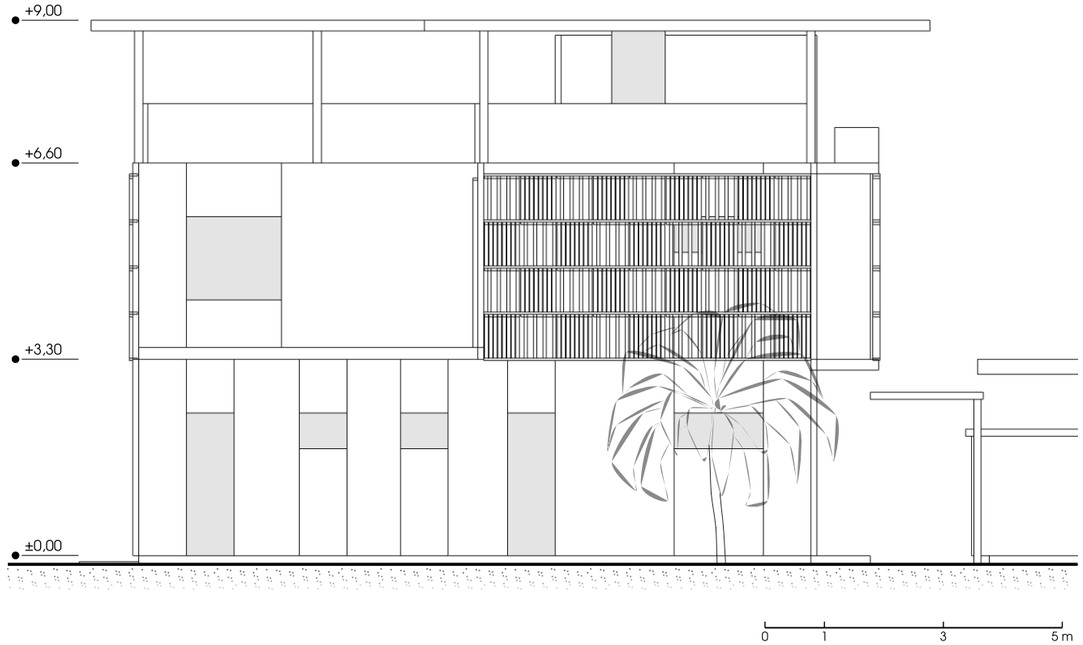

ÉLÉVATION EST, V1 / passage de service

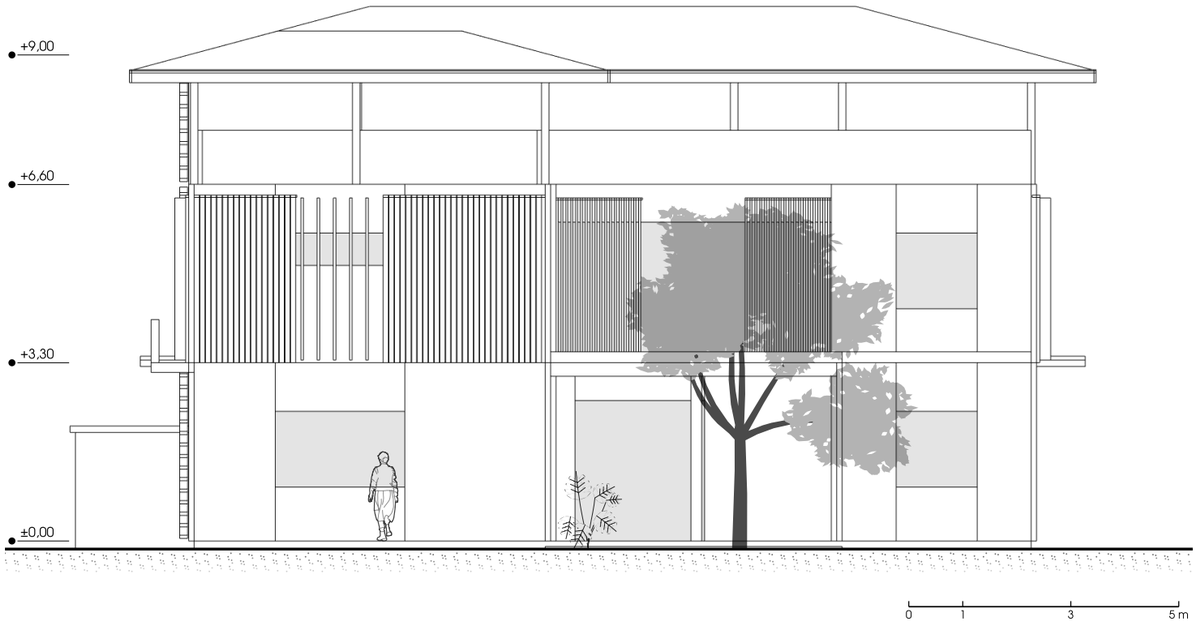


ÉLÉVATION SUD, V2

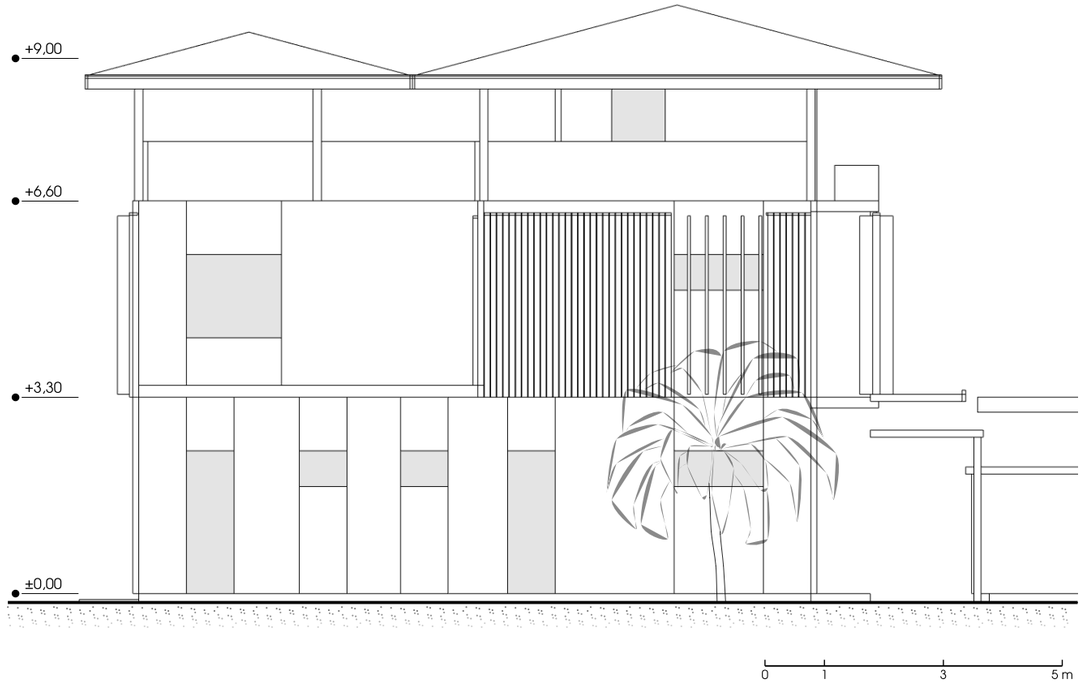


ÉLÉVATION EST, V2


1 · COUPE VERTICALE, FAÇADE NORD, V1 : LAMES EN DAMIER

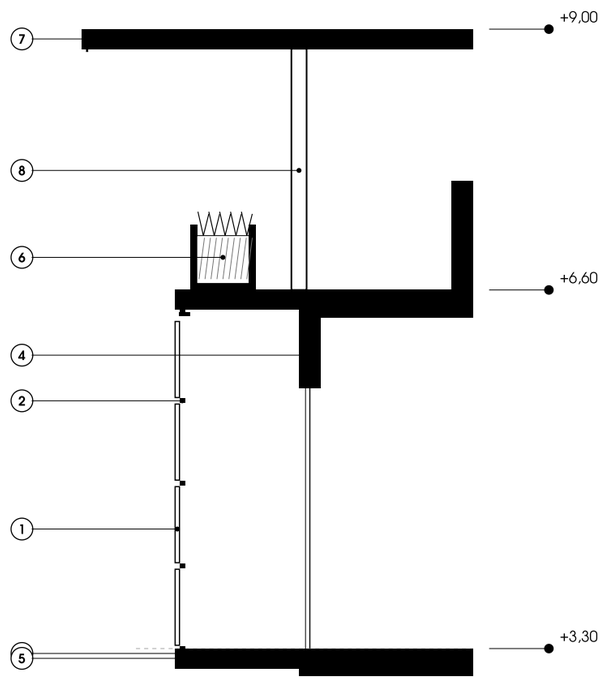

2 · COUPE VERTICALE, FAÇADE NORD, V2 : BARDAGE, BRISE-SOLEIL, DÉBORDS

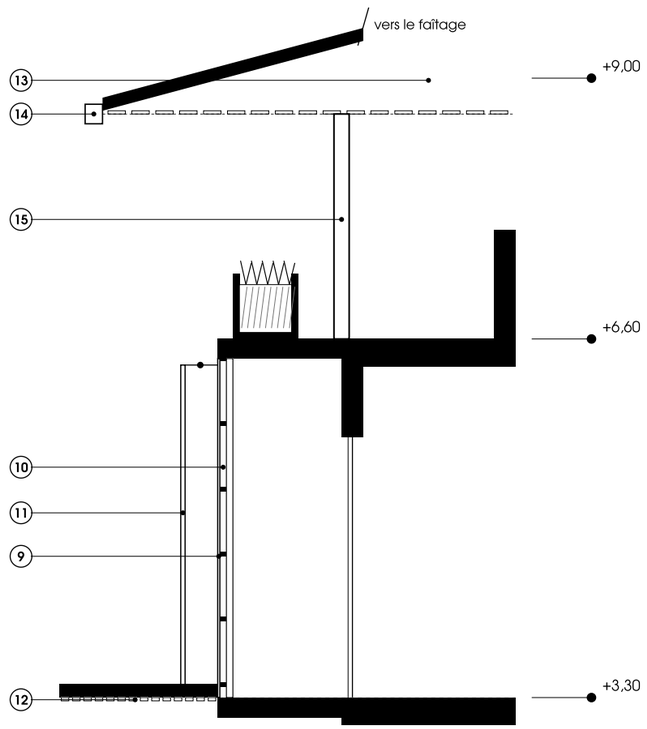


3 · PLAN DE LA PEAU V1 : PANNEAUX DENSE ET OUVERT ALTERNÉS, MODULE 0,62 M

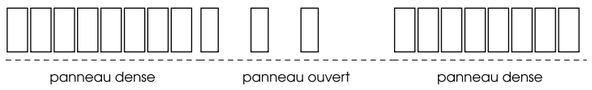

Lames iroko 65 × 140 mm au pas de 75 mm (dense) et 55 × 140 mm au pas de 160 mm (ouvert) ; les rangs sont décalés d'un module d'un niveau à l'autre (damier) ; traverses acier en tirets.

4 · PLAN DE LA PEAU V2 : BARDAGE ET BRISE-SOLEIL PIVOTANTS

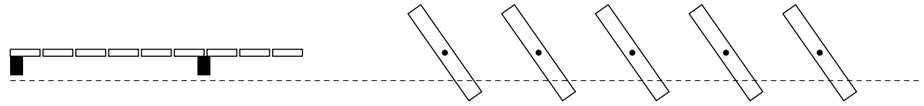

Bardage iroko 22 × 95 mm à joint de 10 mm sur tasseaux 40 × 60 ; brise-soleil 50 × 340 mm sur axe inox tous les 300 mm, groupés dans l'axe des baies (représentés ouverts à 35°).

NOMENCLATURE

1. Claustra de lames de bois dur (iroko), panneaux de 0,62 m en damier, 4 rangs par étage
2. Traverse acier 40 × 40 thermolaquée noire, filante tous les 0,76 m
3. Équerre de fixation en nez de dalle, acier galvanisé chevillé
4. Baie de la chambre ou du salon familial sur la loggia de 1,00 m
5. Nez de dalle mince de 18 cm, béton blanc, même cote sur la villa et les duplex
6. Jardinière en rive de toiture : plantation basse, étanchéité, drainage, goutte-à-goutte
7. Couverture plate mince de 18 cm, débord de 1,0 à 1,5 m, goutte d'eau ; descentes en façade
8. Poteau acier Ø 140 noir sur platine, sur les axes de la trame
9. Bardage iroko 22 × 95, joint creux de 10 mm
10. Tasseaux 40 × 60 traités classe 4, lame d'air ventilée
11. Ossature secondaire acier entre nez de dalle ; brise-soleil pivotants 50 × 340 sur axe inox
12. Auvent bas à +3,30 sur la rue, sous-face en lames de bois
13. Toit en croupe à 15°, bac acier isolé, sous-face ventilée en lames de bois
14. Chéneau et descente d'eaux pluviales en façade, aucune eau vers le patio
15. Poteau acier Ø 140 noir

Principes d'esquisse, à valider par le BET structure et l'entreprise (sections, fixations, essences, classes d'emploi).

DÉTAILS DE FAÇADE / principes constructifs, sans échelle



Vue d’ambiance · rue Nord, V1, à la tombée de la nuit



Vue d’ambiance · rue Nord, V2, après la pluie



Vue d’ambiance · angle des deux rues, V1



Vue d’ambiance · angle des deux rues, V2, saison des pluies



Vue d’ambiance · le patio depuis la terrasse couverte




Vue d’ambiance · le toit-terrasse couvert, V2

MAISONS
2 duplex de 153,0 m², 8,5 m de façade

TRAME
3 · 8,5 · 8,5 m ; 3 · 6,5 · 2,5 · 3 m

STATIONNEMENT
2 places longitudinales dans la bande Ouest, portails sur la rue

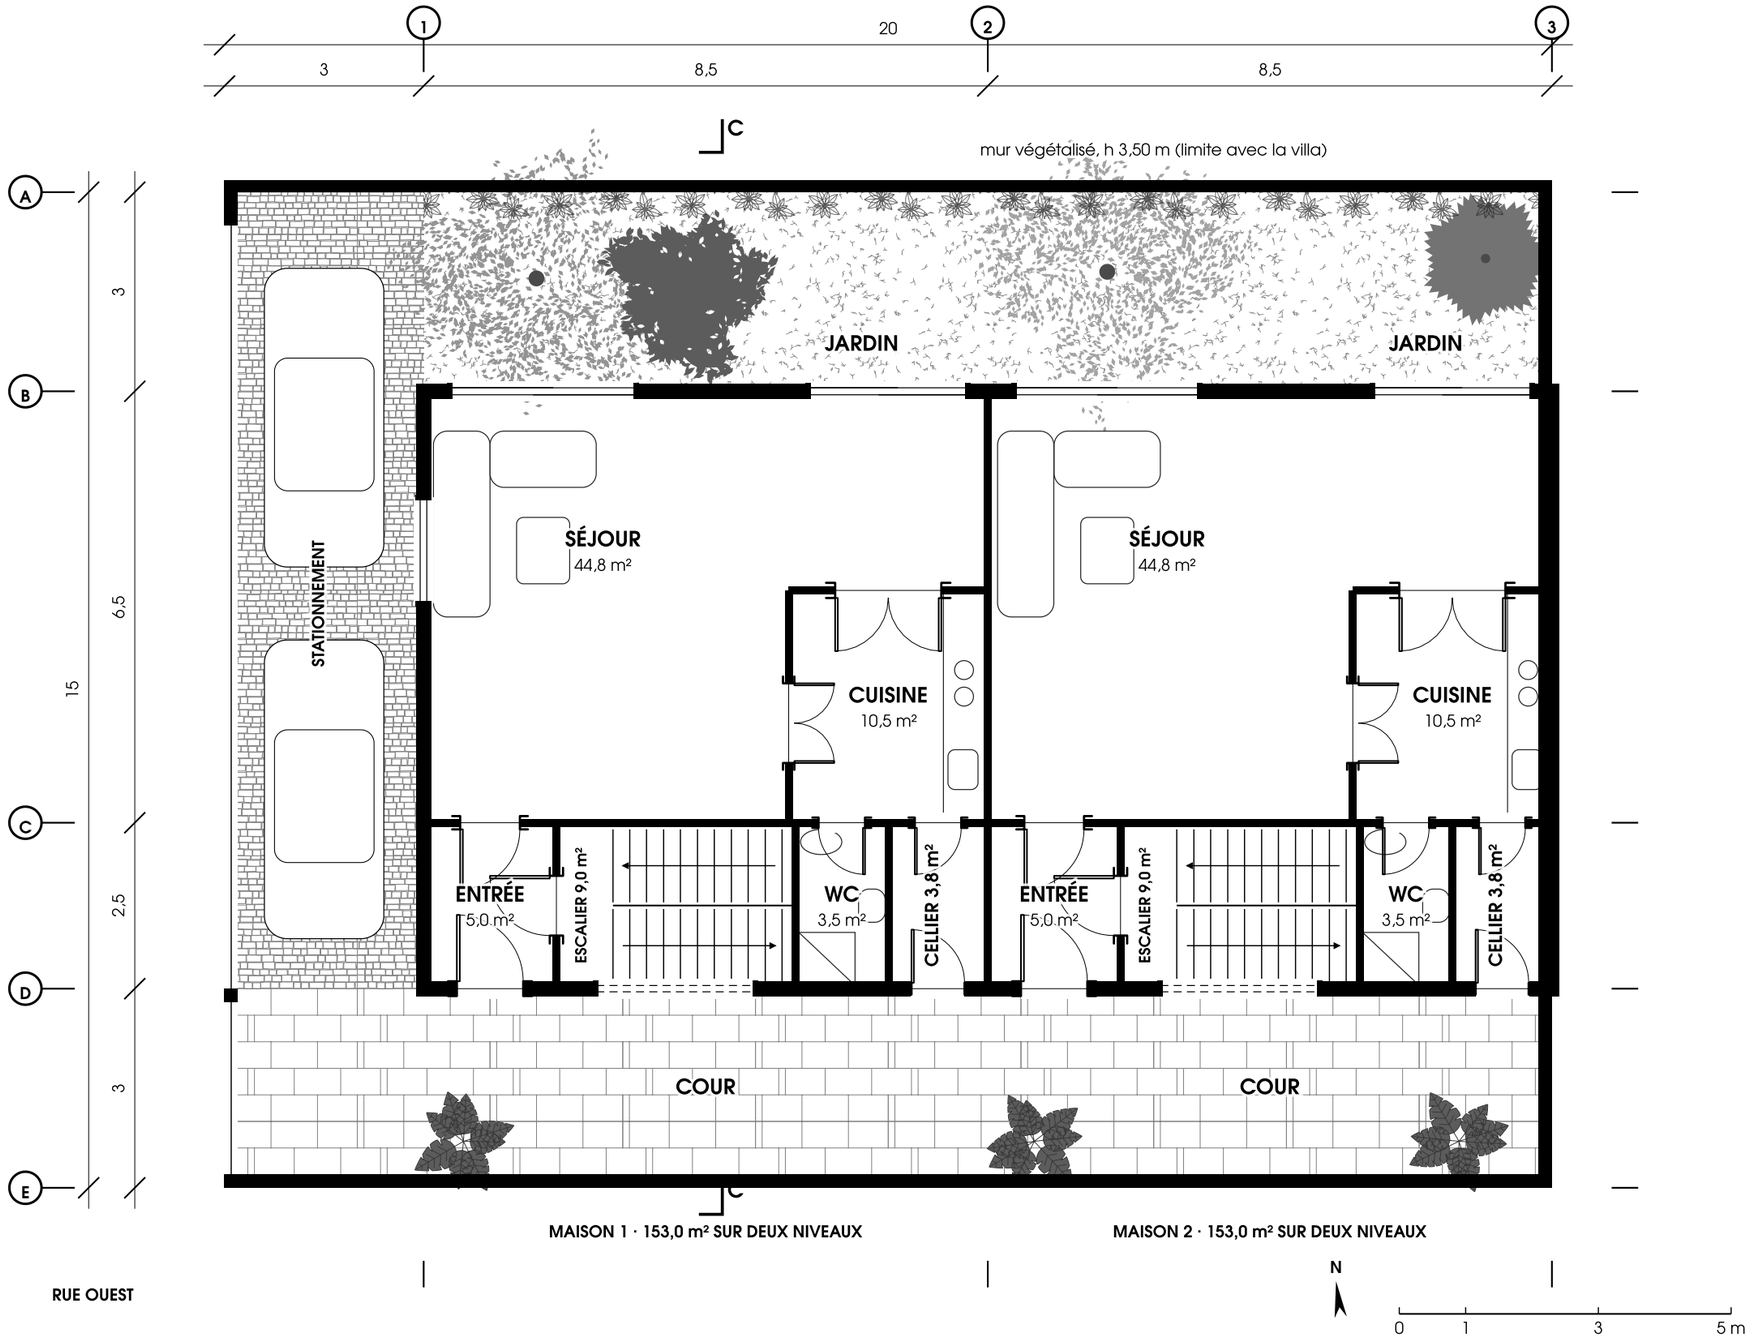


PLAN DU REZ-DE-CHAUSSÉE / échelle graphique

ÉTAGE

chambre principale avec dressing et salle de bains, chambre 2, salle d'eau

PEAU


la même que la villa

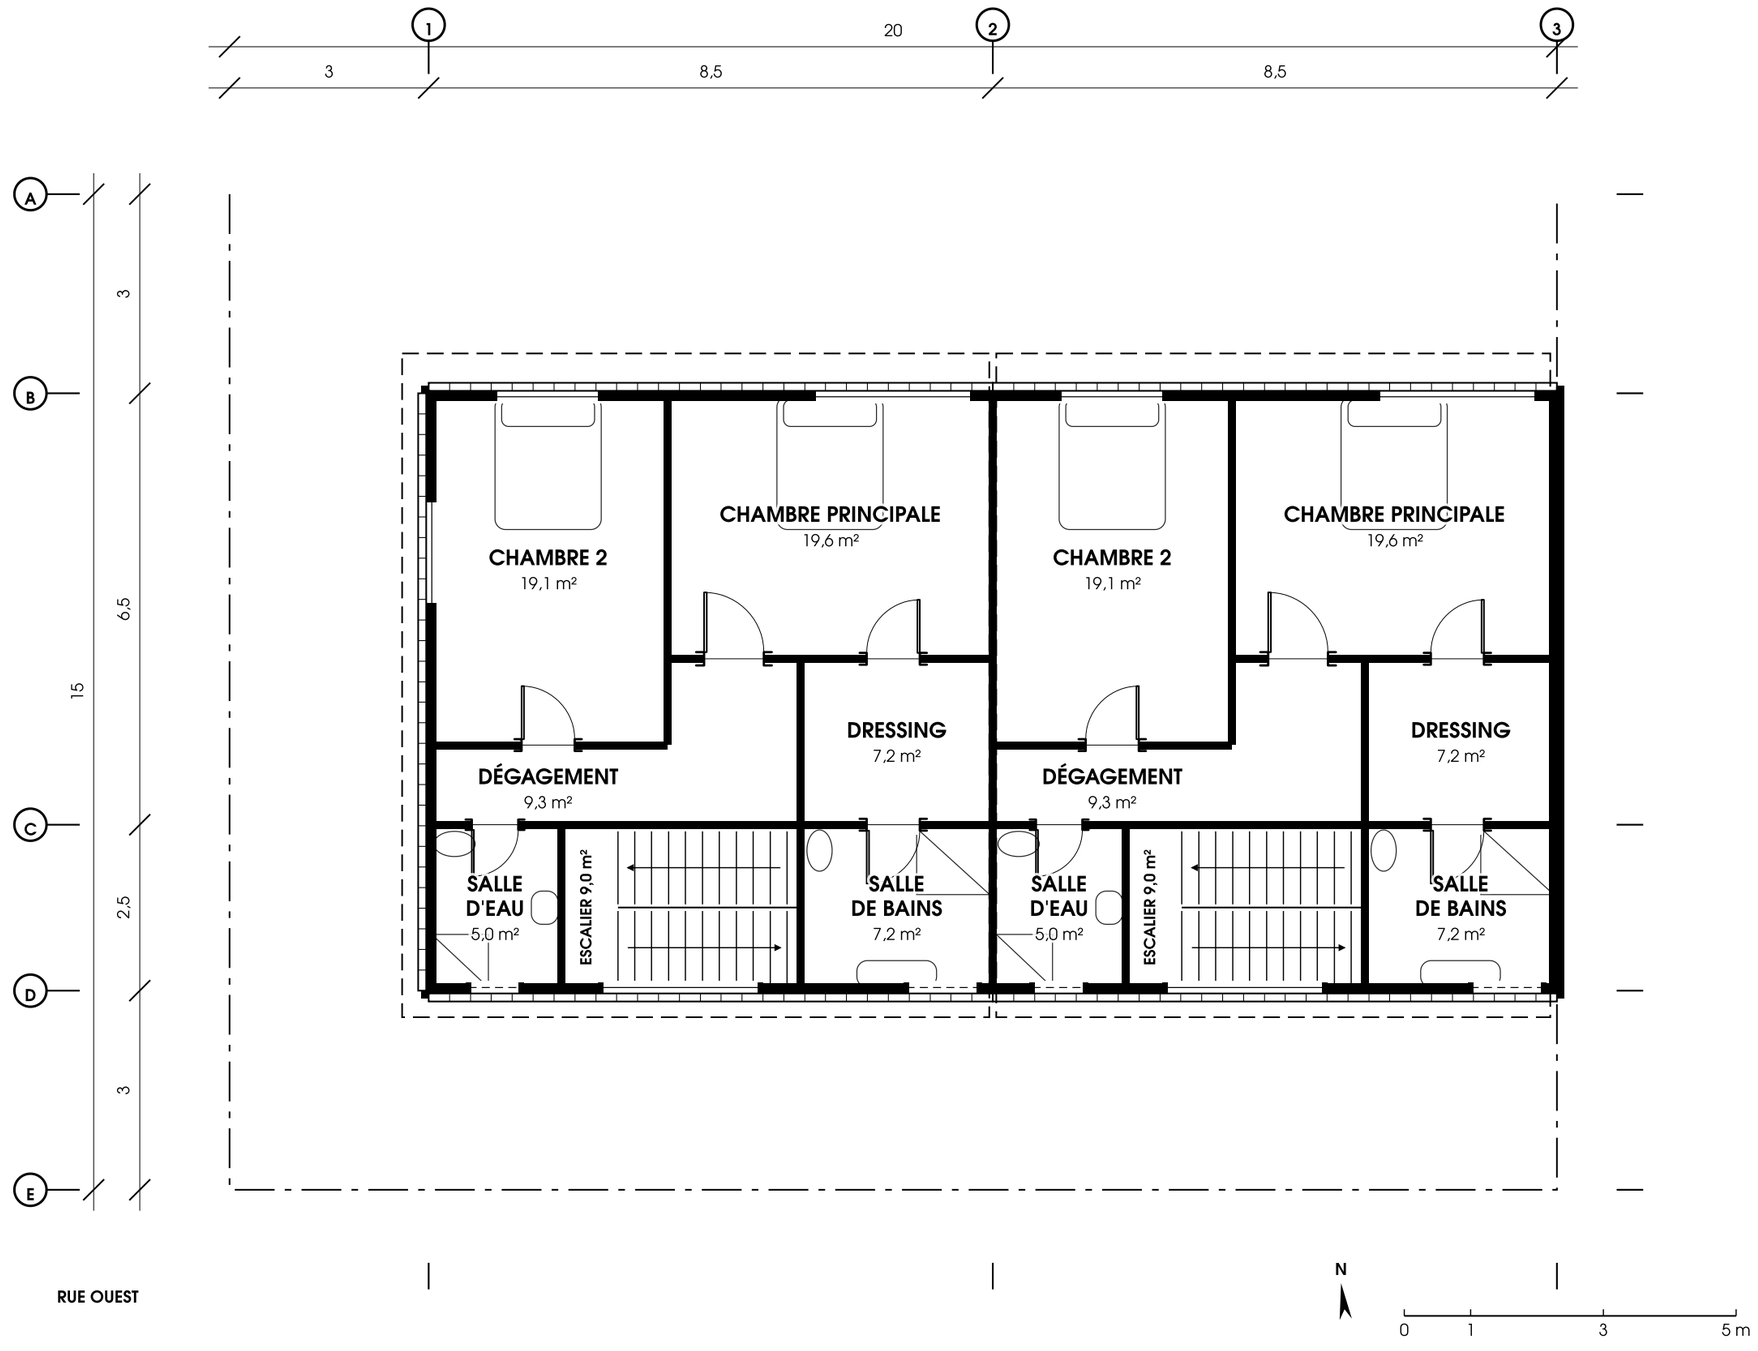


PLAN DE L'ÉTAGE / échelle graphique

TOIT-TERRASSE
67,5 m² par maison, couvert à +9,00


COUVERTURE
la même que la villa

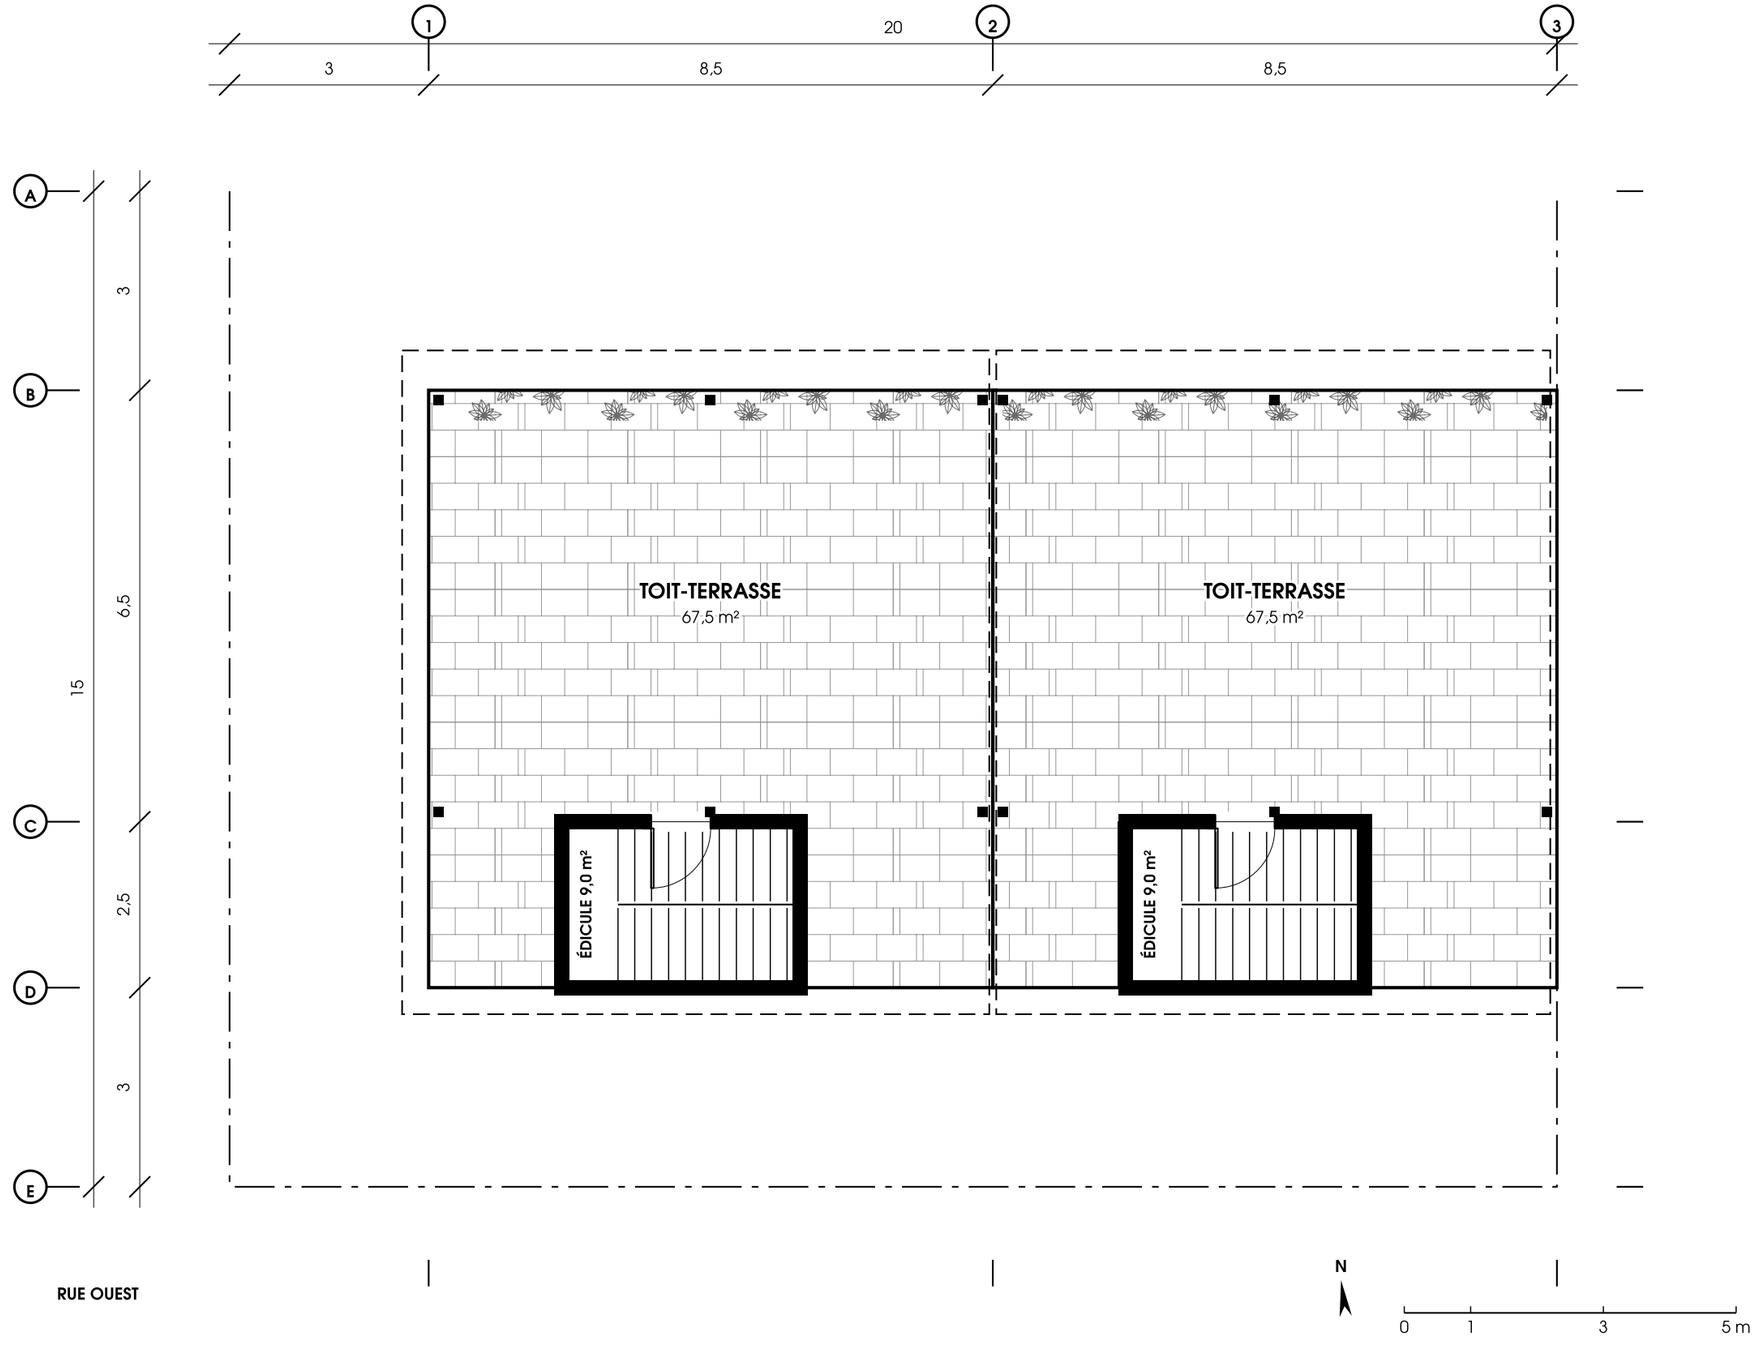

PLAN DU NIVEAU HAUT / échelle graphique

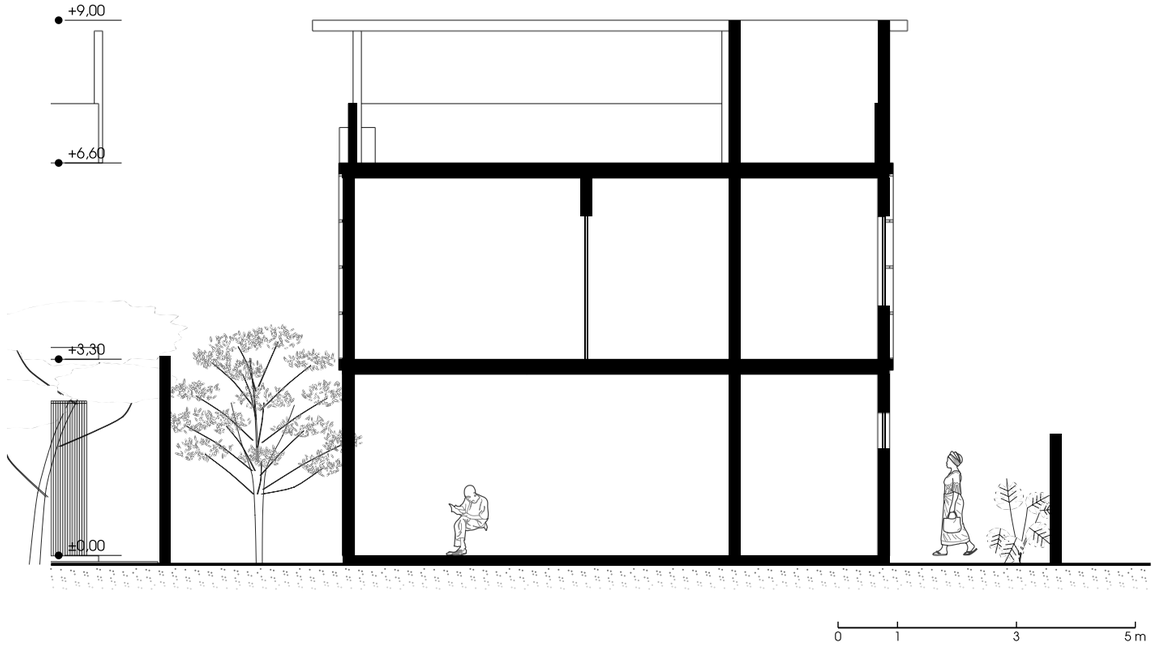

COUPE CC / Nord-Sud sur la maison 1

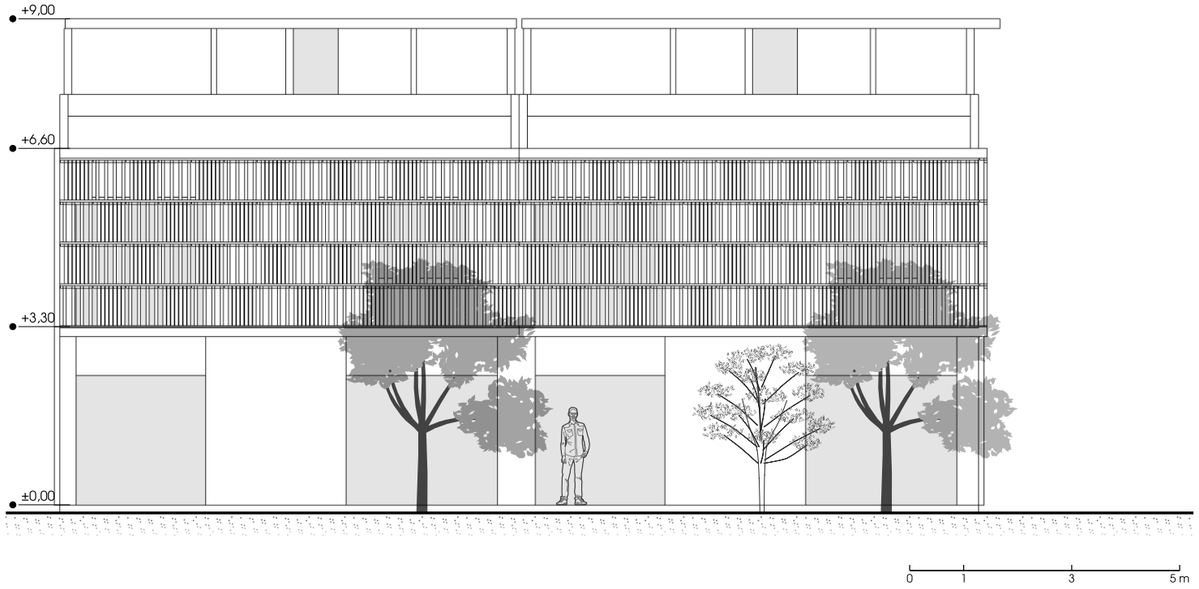

ÉLÉVATION NORD DES DUPLEX, V1 / sur les jardins



Vue d'ambiance · les duplex depuis la rue Ouest, V1



Vue d'ambiance · les duplex depuis la rue Ouest, V2

SURFACES

CALCULÉES SUR LE MODÈLE

PIÈCE	M²
REZ-DE-CHAUSSÉE	
Guérite	5,8
Local ge (hors clos)	5,9
Passage couvert (hors clos)	13,0
Escalier	12,6
Wc	3,9
Hall	11,0
Salle à manger	27,5
Cuisine	11,0
Cuisine africaine	13,7
Buanderie	5,6
Salon	37,7
Terrasse couverte (hors clos)	13,2
Patio (hors clos)	25,3
Bureau	7,0
Salle d'eau	4,9
Chambre nounou	8,4
Préau (hors clos)	7,2
Séchoir (hors clos)	8,4
Surface close	149,0
ÉTAGE	
Rangement	3,0
Loggia (hors clos)	12,5
Escalier	12,6
Lingerie	3,9
Salon familial	19,2
Chambre 1	15,1
Salle d'eau	8,6
Galerie	6,6
Chambre 2	19,2
Salle de bains	7,8
Dressing	9,1
Chambre principale	20,8
Jardinière (hors clos)	2,6
Surface close	125,9
NIVEAU HAUT	
Édicule	12,6
Toit-terrasse (hors clos)	110,3
Jardinière (hors clos)	15,5
TOTAL CLOS VILLA	**275,0 m²**

PIÈCE	M²
REZ-DE-CHAUSSÉE	
Séjour	44,8
Cuisine	10,5
Entrée	5,0
Escalier	9,0
Wc	3,5
Cellier	3,8
Jardin (hors clos)	25,5
Cour (hors clos)	25,5
Stationnement (hors clos)	36,0
Allée piétonne (hors clos)	9,0
Surface close	76,5
ÉTAGE	
Chambre 2	19,1
Chambre principale	19,6
Dressing	7,2
Dégagement	9,3
Escalier	9,0
Salle d'eau	5,0
Salle de bains	7,2
Surface close	76,5
NIVEAU HAUT	
Édicule	9,0
Toit-terrasse (hors clos)	67,5
TOTAL CLOS MAISON 1	**153,0 m²**

VILLA, CLOS

275,0 m²

VILLA, EMPRISE

143,2 m²

DUPLEX, CLOS

2 × 153,0 = 306,0 m²

LOYER DUPLEX

600 000 FCFA / mois, hypothèse

DÉSIGNATION	SOURCE	QTÉ	PU HT	TOTAL HT
REZ-DE-CHAUSSÉE				
Guérite	Réserve / buanderie / cellier	5,8 m²	250 000	1 440 000
Local ge	Réserve / buanderie / cellier	5,9 m²	250 000	1 485 000
Passage couvert	Terrasse couverte / galerie	13,0 m²	175 000	2 275 000
Escalier	Escalier	12,6 m²	300 000	3 780 000
Wc	Salles d'eau / SdB / WC	3,9 m²	750 000	2 925 000
Hall	Circulations (hall, dégagements, palier)	11,0 m²	275 000	3 025 000
Salle à manger	Séjour / SAM / salon	27,5 m²	300 000	8 250 000
Cuisine	Cuisine	11,0 m²	425 000	4 675 000
Cuisine africaine	Cuisine africaine (carrelée, ventilée)	13,7 m²	425 000	5 801 250
Buanderie	Réserve / buanderie / cellier	5,6 m²	250 000	1 400 000
Salon	Séjour / SAM / salon	37,7 m²	300 000	11 310 000
Terrasse couverte	Terrasse couverte / galerie	13,2 m²	175 000	2 310 000
Patio	Cour de service / séchoir / patio	25,3 m²	42 500	1 075 250
Bureau	Chambres	7,0 m²	300 000	2 100 000
Salle d'eau	Salles d'eau / SdB / WC	4,9 m²	750 000	3 675 000
Chambre nounou	Chambres	8,4 m²	300 000	2 520 000
Préau	Terrasse couverte / galerie	7,2 m²	175 000	1 268 750
Séchoir	Cour de service / séchoir / patio	8,4 m²	42 500	357 000
ÉTAGE				
Rangement	Dressing / placards	3,0 m²	425 000	1 275 000
Loggia	Balcon d'étage	12,5 m²	225 000	2 812 500
Escalier	Escalier	12,6 m²	300 000	3 780 000
Lingerie	Dressing / placards	3,9 m²	425 000	1 657 500
Salon familial	Séjour / SAM / salon	19,2 m²	300 000	5 775 000
Chambre 1	Chambres	15,1 m²	300 000	4 515 000
Salle d'eau	Salles d'eau / SdB / WC	8,6 m²	750 000	6 450 000
Galerie	Circulations (hall, dégagements, palier)	6,6 m²	275 000	1 815 000
Chambre 2	Chambres	19,2 m²	300 000	5 775 000
Salle de bains	Salles d'eau / SdB / WC	7,8 m²	750 000	5 850 000
Dressing	Dressing / placards	9,1 m²	425 000	3 867 500
Chambre principale	Chambres	20,8 m²	300 000	6 240 000
Jardinière	Balcon d'étage	2,6 m²	225 000	576 000
NIVEAU HAUT				
Édicule	Escalier	12,6 m²	300 000	3 780 000
Toit-terrasse	Toit-jardin accessible	110,3 m²	175 000	19 311 250
Jardinière	Espaces verts (aménagement)	15,5 m²	10 000	155 000
AMÉNAGEMENTS EXTÉRIEURS ET VRD				
Parking, allée et aire de livraison pavés (pavés drainants)	base ÷ 2	55,0 m2	42 500	2 337 500
Jardins plantés (terre végétale, gazon, arbres d'ombrage)	base ÷ 2	70,0 m2	10 000	700 000
Bâche à eau + surpresseur	base ÷ 2	1,0 ens	2 023 538	2 023 538
Réfection clôture existante + portail coulissant + portillon	prix de marché	1,0 ens	3 000 000	3 000 000
Mur séparatif villa / locatif (h 2,5 m) + claustras de la cour de service	prix de marché	8,0 ml	60 000	480 000
Assainissement autonome (fosse + puisard) + branchements CIE / SODECI	prix de marché	1,0 ens	3 500 000	3 500 000
Traitement anti-termites du sol + remblai de plateforme	prix de marché	160,0 m2	8 000	1 280 000
Grilles de défense RDC et étage + moustiquaires	prix de marché	70,0 m2	45 000	3 150 000
Chauffe-eau solaires + attentes climatisation (par logement)	prix de marché	2,5 u	900 000	2 250 000
Cuisine africaine : hotte d'extraction, évier double bac, cage à bouteilles de gaz	prix de marché	1,0 ens	900 000	900 000
PLUS-VALUES DU PARTI				
Menuiseries bois persiennées (jalousies) / écrans coulissants en lattes	prix de marché	12,0 m2	120 000	1 440 000
Claustras en terre cuite / BTC ajourée (cour de service, façades Ouest, coursive)	prix de marché	32,0 m2	30 000	960 000
Débords de toiture et casquettes (hors clos)	prix de marché	15,0 m2	60 000	900 000
Patio : arbre (frangipanier), massifs, éclairage (bassins supprimés, markup)	prix de marché	1,0 ens	2 200 000	2 200 000
Patio : caniveau grillé périphérique + exutoire	prix de marché	1,0 ens	1 200 000	1 200 000
Peau de l'étage en lames de bois dur traité, sur toutes les faces (V1 damier ; V2 bardage et brise-soleil)	prix de marché	110,0 m2	85 000	9 350 000
Claustra en blocs de béton ajourés (clôture sur rue, lanterne d'escalier)	prix de marché	30,0 m2	32 000	960 000
Plus-value parement en moellons de granite (RDC sur rues, guérite, socle de clôture)	prix de marché	100,0 m2	28 000	2 800 000
Plus-value béton brut coffré planches (nez de dalle, corniches à goutte d'eau, porche)	prix de marché	60,0 m2	15 000	900 000
Toiture végétalisée extensive (substrat 15 cm, drainage, étanchéité anti-racines) + jardinières de rive	prix de marché	33,5 m2	25 000	837 500
Écrans en lattes de bois de la passerelle et stores bambou sous débords Ouest	prix de marché	1,0 ens	900 000	900 000
Couverture du toit-terrasse à +9,00 sur poteaux acier, sous-face bois (V1 toiture plate mince, V2 croupe)	prix de marché	150,0 m2	70 000	10 500 000
Jardinière continue en rive de toiture (plantation basse, sans retombées ; goutte-à-goutte)	prix de marché	15,5 ml	75 000	1 162 500
Mur végétalisé de 3,50 m en limite villa / locatif (treillis inox, jardinières, arrosage)	prix de marché	70,0 m2	55 000	3 850 000
Garde-corps des toits-terrasses (acrotère 1,0 m + lisse)	prix de marché	45,0 ml	35 000	1 575 000
Local GE + niche compteurs (dalle, claustra, porte)	prix de marché	1,0 ens	1 200 000	1 200 000
TOTAL TRAVAUX HT				**193 663 038**
Honoraires architecte (conception + suivi)		8,00 %		15 493 043
BET structure / fluides		2,00 %		3 873 261
Étude géotechnique		1,50 %		2 904 946
Bureau de contrôle		1,35 %		2 614 451
Assurances (TRC / dommages)		1,20 %		2 323 956
Imprévus (stade esquisse)		10,00 %		19 366 304
TOTAL HT				**240 238 999**
TVA		18 %		43 243 020
TOTAL TTC				**283 482 019**

ESTIMATIF

DÉSIGNATION	SOURCE	QTÉ	PU HT	TOTAL HT
REZ-DE-CHAUSSÉE				
Séjour (× 2)	Séjour-cuisine (locatif)	89,5 m²	275 000	24 612 500
Cuisine (× 2)	Kitchenette / bande humide	21,0 m²	425 000	8 925 000
Entrée (× 2)	Dégagement / placard / bureau	10,0 m²	200 000	2 000 000
Escalier (× 2)	Escalier	18,0 m²	300 000	5 400 000
Wc (× 2)	Salle d'eau (locatif)	7,0 m²	500 000	3 500 000
Cellier (× 2)	Dégagement / placard / bureau	7,5 m²	200 000	1 500 000
Jardin (× 2)	Espaces verts (aménagement)	51,0 m²	10 000	510 000
Cour	Parking et allées pavés	51,0 m²	42 500	2 167 500
Stationnement	Parking et allées pavés	36,0 m²	42 500	1 530 000
Allée piétonne	Parking et allées pavés	9,0 m²	42 500	382 500
ÉTAGE				
Chambre 2 (× 2)	Chambre / alcôve (locatif)	38,2 m²	250 000	9 540 000
Chambre principale (× 2)	Chambre / alcôve (locatif)	39,2 m²	250 000	9 800 000
Dressing (× 2)	Dressing / placards	14,5 m²	425 000	6 162 500
Dégagement (× 2)	Dégagement / placard / bureau	18,6 m²	200 000	3 728 000
Escalier (× 2)	Escalier	18,0 m²	300 000	5 400 000
Salle d'eau (× 2)	Salle d'eau (locatif)	10,0 m²	500 000	5 000 000
Salle de bains (× 2)	Salle d'eau (locatif)	14,5 m²	500 000	7 250 000
NIVEAU HAUT				
Édicule (× 2)	Escalier	18,0 m²	300 000	5 400 000
Toit-terrasse (× 2)	Toit-jardin accessible	135,0 m²	175 000	23 625 000
AMÉNAGEMENTS EXTÉRIEURS ET VRD				
Parking, allée et aire de livraison pavés (pavés drainants)	base ÷ 2	75,0 m2	42 500	3 187 500
Jardins plantés (terre végétale, gazon, arbres d'ombrage)	base ÷ 2	51,0 m2	10 000	510 000
Bâche à eau + surpresseur	base ÷ 2	1,0 ens	2 023 538	2 023 538
Réfection clôture existante + portail coulissant + portillon	prix de marché	1,0 ens	3 000 000	3 000 000
Assainissement autonome (fosse + puisard) + branchements CIE / SODECI	prix de marché	1,2 ens	3 500 000	4 200 000
Traitement anti-termites du sol + remblai de plateforme	prix de marché	160,0 m2	8 000	1 280 000
Grilles de défense RDC et étage + moustiquaires	prix de marché	45,0 m2	45 000	2 025 000
Chauffe-eau solaires + attentes climatisation (par logement)	prix de marché	2,0 u	900 000	1 800 000
PLUS-VALUES DU PARTI				
Peau de l'étage en lames de bois dur traité, sur toutes les faces (V1 damier ; V2 bardage et brise-soleil)	prix de marché	133,0 m2	85 000	11 305 000
Plus-value béton brut coffré planches (nez de dalle, corniches à goutte d'eau, porche)	prix de marché	30,0 m2	15 000	450 000
Couverture du toit-terrasse à +9,00 sur poteaux acier, sous-face bois (V1 toiture plate mince, V2 croupe)	prix de marché	178,0 m2	70 000	12 460 000
Jardinière continue en rive de toiture (plantation basse, sans retombées ; goutte-à-goutte)	prix de marché	17,0 ml	75 000	1 275 000
Garde-corps des toits-terrasses (acrotère 1,0 m + lisse)	prix de marché	52,0 ml	35 000	1 820 000
TOTAL TRAVAUX HT				**171 769 038**
Honoraires architecte (conception + suivi)			8,00 %	13 741 523
BET structure / fluides			2,00 %	3 435 381
Étude géotechnique			1,50 %	2 576 536
Bureau de contrôle			1,35 %	2 318 882
Assurances (TRC / dommages)			1,20 %	2 061 228
Imprévus (stade esquisse)			10,00 %	17 176 904
TOTAL HT				**213 079 492**
TVA			18 %	38 354 309
TOTAL TTC				**251 433 801**

22 SUITE

VILLA
travaux 193,7 M HT · 283,5 M TTC

DUPLEX
travaux 171,8 M HT · 251,4 M TTC

À ARBITRER
variante de façade V1 ou V2 ; stationnement longitudinal des duplex ; loyer à confirmer

À VÉRIFIER
R+1 maximum : le niveau couvert à +9,00 est un toit-terrasse ouvert, à faire valider

HORS DOSSIER
esquisse, estimatif Excel et business plan 01 à 03 : versions précédentes